
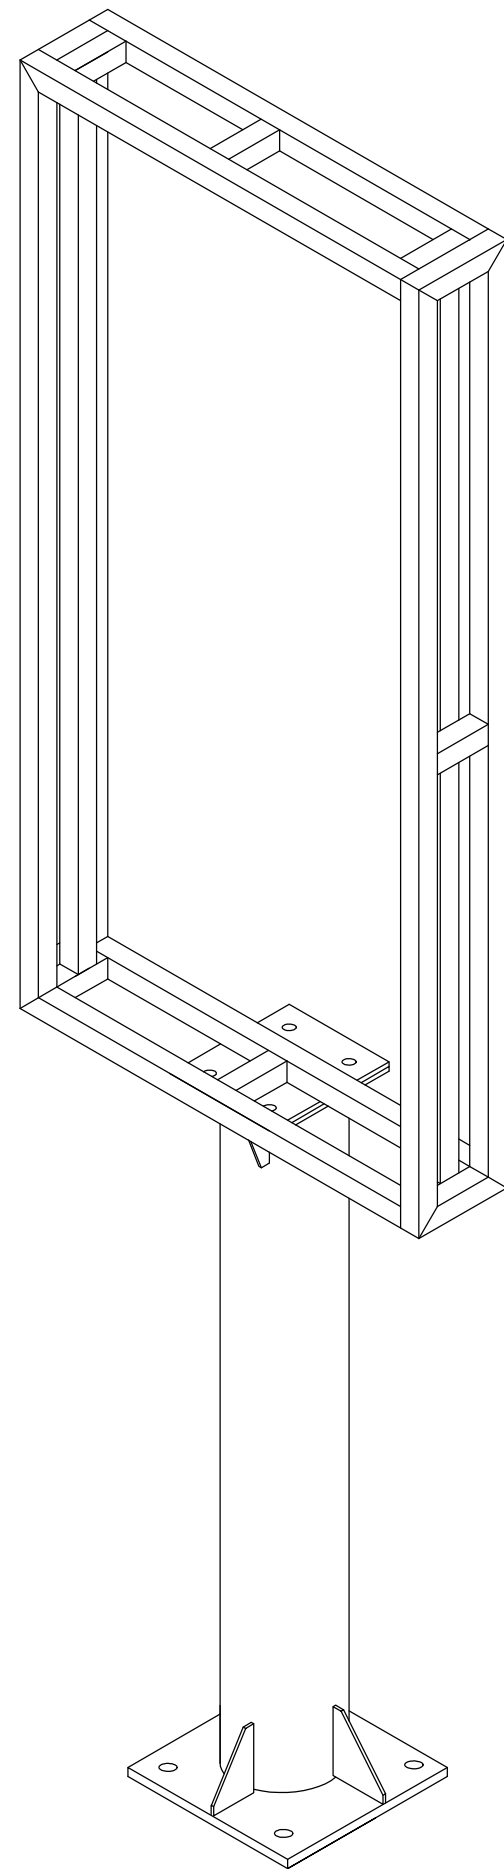
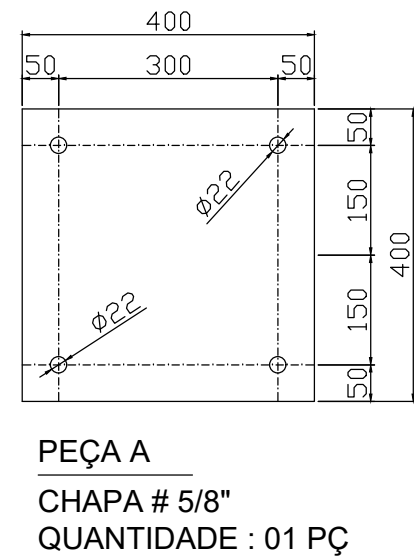
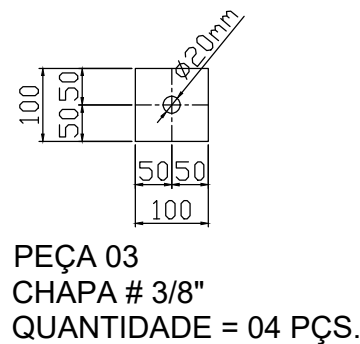
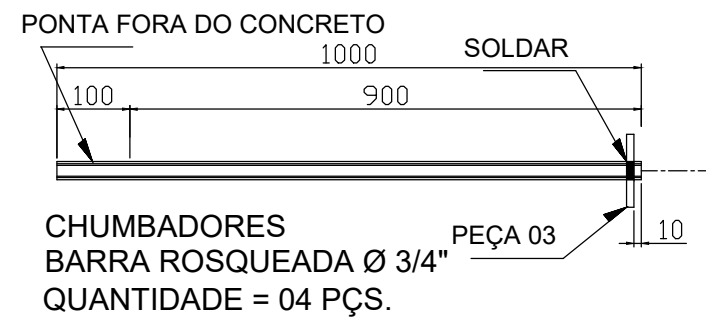
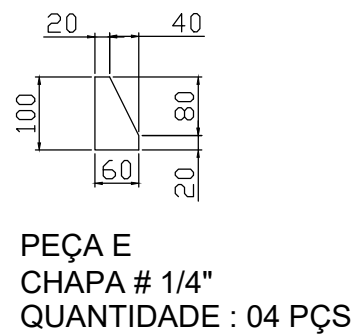
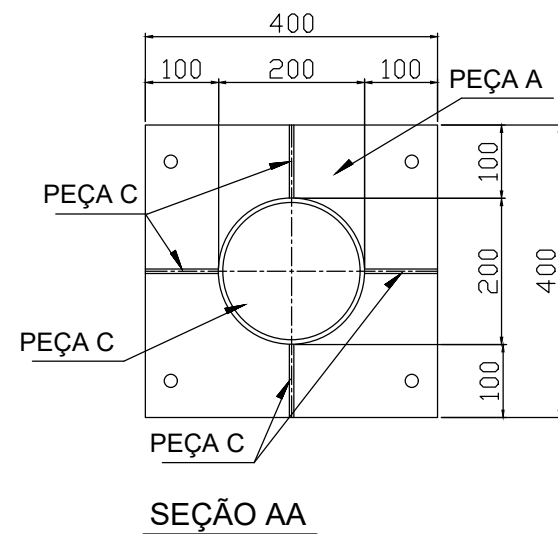
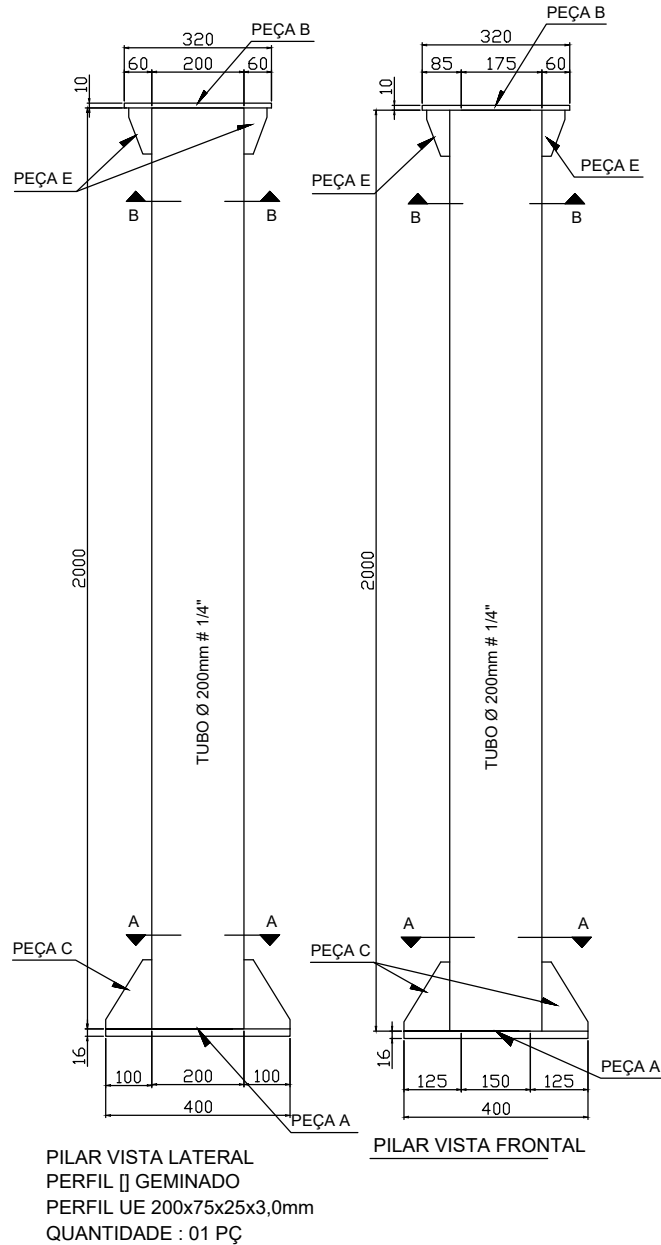
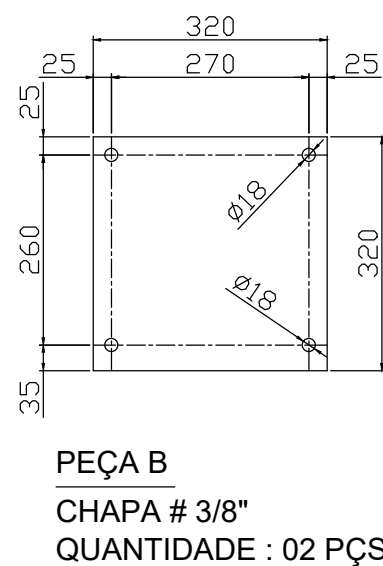
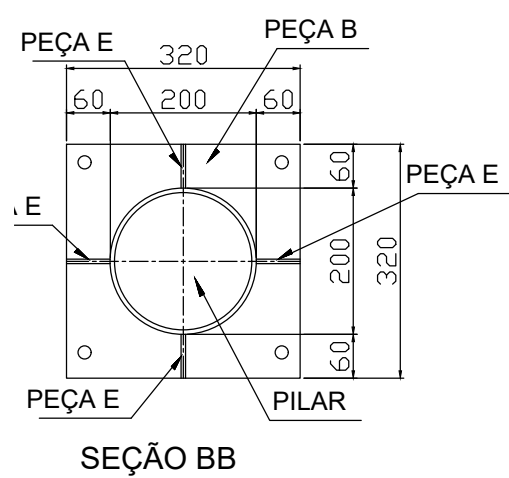
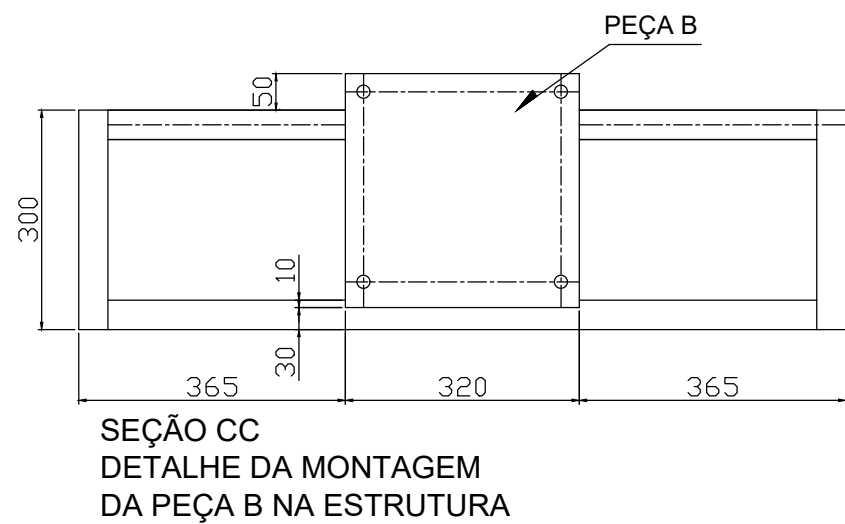
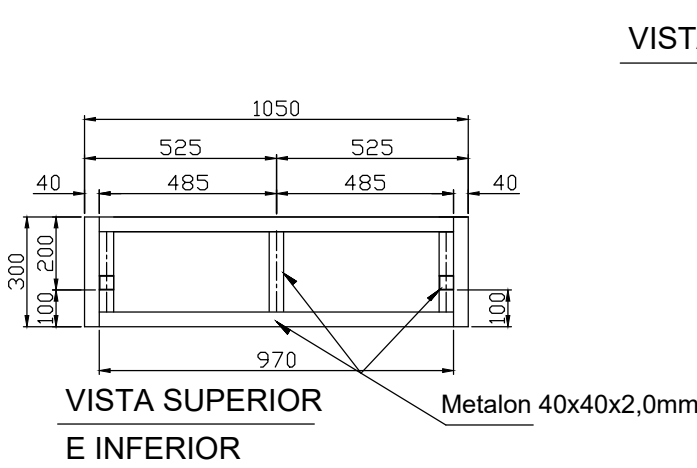


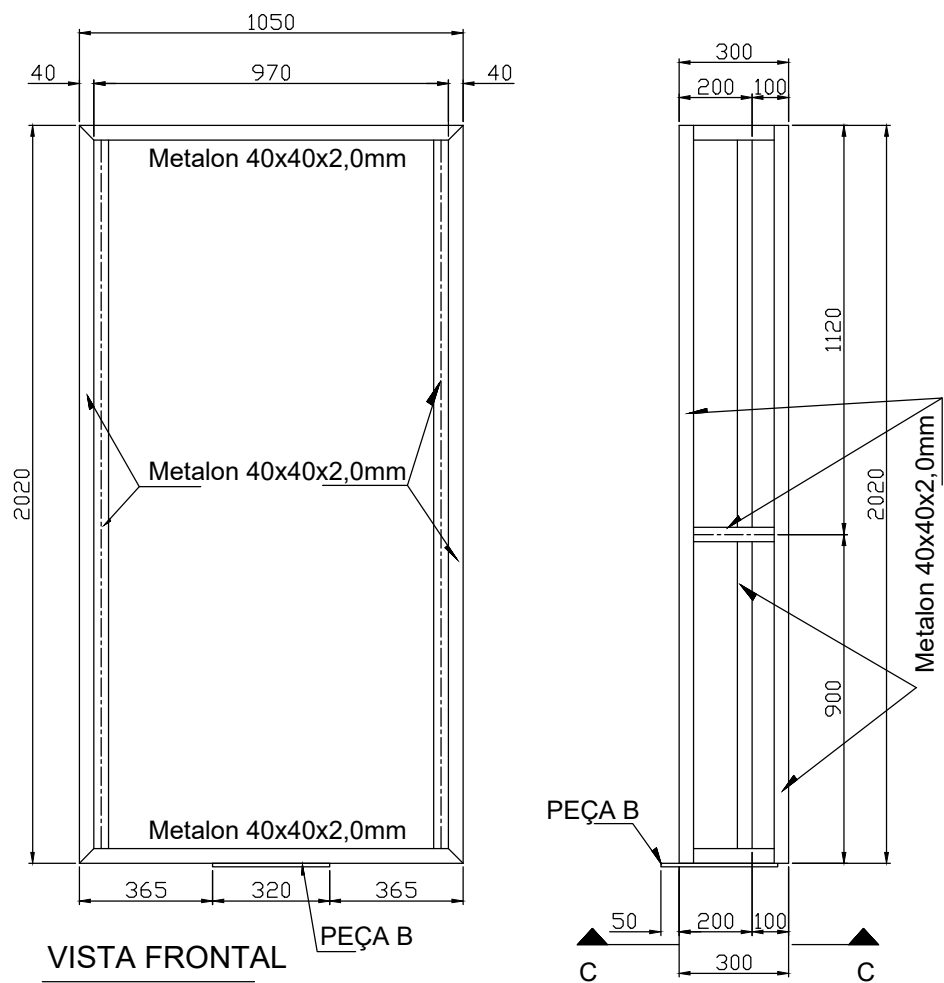

| LISTA DE MATERIAIS                                |                                      |        |       |                  |              |             |
|---------------------------------------------------|--------------------------------------|--------|-------|------------------|--------------|-------------|
| Cliente: ANDERSON KARCZMARSKI                     |                                      |        |       | DATA: 28/07/2023 |              |             |
| Obra: PAINEL 1x2 GB RENTAL OUTDOOR PILAR 2 METROS |                                      |        |       |                  |              |             |
|                                                   | ESTRUTURA METÁLICA                   |        |       |                  |              |             |
| POS.                                              | DESCRIÇÃO                            | COMPR. | UNID. | QUANT.           | PESO UNIT.   | PESO TOTAL. |
| 1                                                 | METALON 40x40x2,0mm                  | 6000mm | PÇS   | 04               | 2,41 KG      | 57,84 KG    |
| 2                                                 | CHAPA # 5/8" x 400 mm (PEÇA A)       | 400mm  | PÇS   | 01               | 125,40 KG/M2 | 20,00 KG    |
| 3                                                 | CHAPA # 3/8" x 320 mm (PEÇA B)       | 320mm  | PÇS   | 02               | 74,48 KG/M2  | 15,25 KG    |
| 4                                                 | CHAPA # 1/4" x 100 mm (PEÇA C)       | 150mm  | PÇS   | 04               | 49,40 KG/M2  | 3,00 KG     |
| 5                                                 | CHAPA # 1/4" x 60 mm (PEÇA E)        | 100mm  | PÇS   | 04               | 49,40 KG/M2  | 1,18 KG     |
| 6                                                 | TUBO Ø 200mm PAREDE # 1/4" (PILAR)   | 2000mm | PÇS   | 01               | 31,00 KG/M   | 62,00 KG    |
| 7                                                 | CHAPA # 14 x 400 mm (GABARITO)       | 400mm  | PÇS   | 01               | 16,00 KG/M2  | 2,50 KG     |
| 8                                                 | BARRA ROSQUEADA Ø 3/4" (CHUMBADORES) | 1000mm | PÇS   | 04               | 2,24 KG/M    | 9,0 KG      |
| 9                                                 | CHAPA # 3/8" x 100 mm (PEÇA 03)      | 100mm  | PÇS   | 04               | 74,50 KG/M2  | 3,00 KG     |
| 10                                                | PARAFUSO SEXTAVADO Ø 5/8"(COMPLETO)  | 2"     | PÇS   | 04               | ////         | ////        |
| 11                                                | PORCA SEXTAVADA Ø 5/8"               | ////   | PÇS   | 08               | ////         | ////        |
| 12                                                | ARRUELA LISA Ø 5/8"                  | ////   | PÇS   | 08               | ////         | ////        |
| 13                                                |                                      |        |       |                  |              |             |
| PESO TOTAL GERAL :                                |                                      |        |       |                  |              | 173,74 KG   |

NOTAS: MEDIDAS EM MILIMETRO;

|    |           |       |       |          |
|----|-----------|-------|-------|----------|
| 2  |           |       |       |          |
| 1  |           |       |       |          |
| 0  | INICIAL   | F.G.S |       | 28/07/23 |
| N° | DESCRIÇÃO | DES.  | RESP. | DATA     |

LED EXPERT

PROJETO SOMENTE PARA ORÇAMENTO  
NÃO UTILIZAR PARA FABRICAÇÃO

|                                       |    |       |                  |             |                  |
|---------------------------------------|----|-------|------------------|-------------|------------------|
| OBRA                                  |    |       | Data:            | Desenhista: |                  |
| PAINEL 1 x 2 GB RENTAL OUTDOOR        |    |       | 28-07-2023       | FABIAN      |                  |
| CONTÉM: PROJETO DE ESTRUTURA METÁLICA |    |       |                  |             |                  |
| ESCALA                                | SE | R.T.: | N° LED EXPERT:   |             | FORMATO: REVISÃO |
| IND.                                  | -- | --    | 157-2023-07-FL01 |             | A2 00            |