
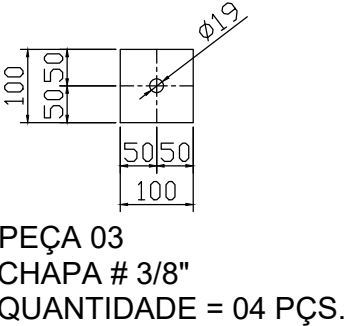
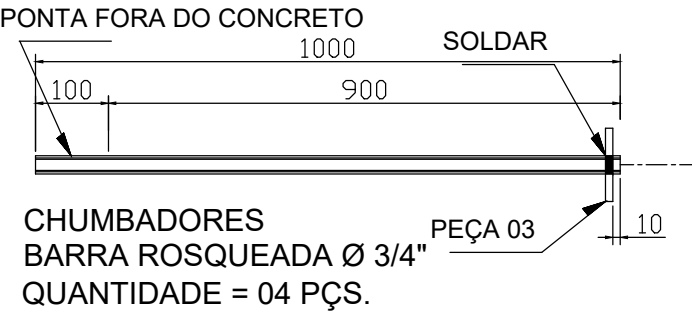


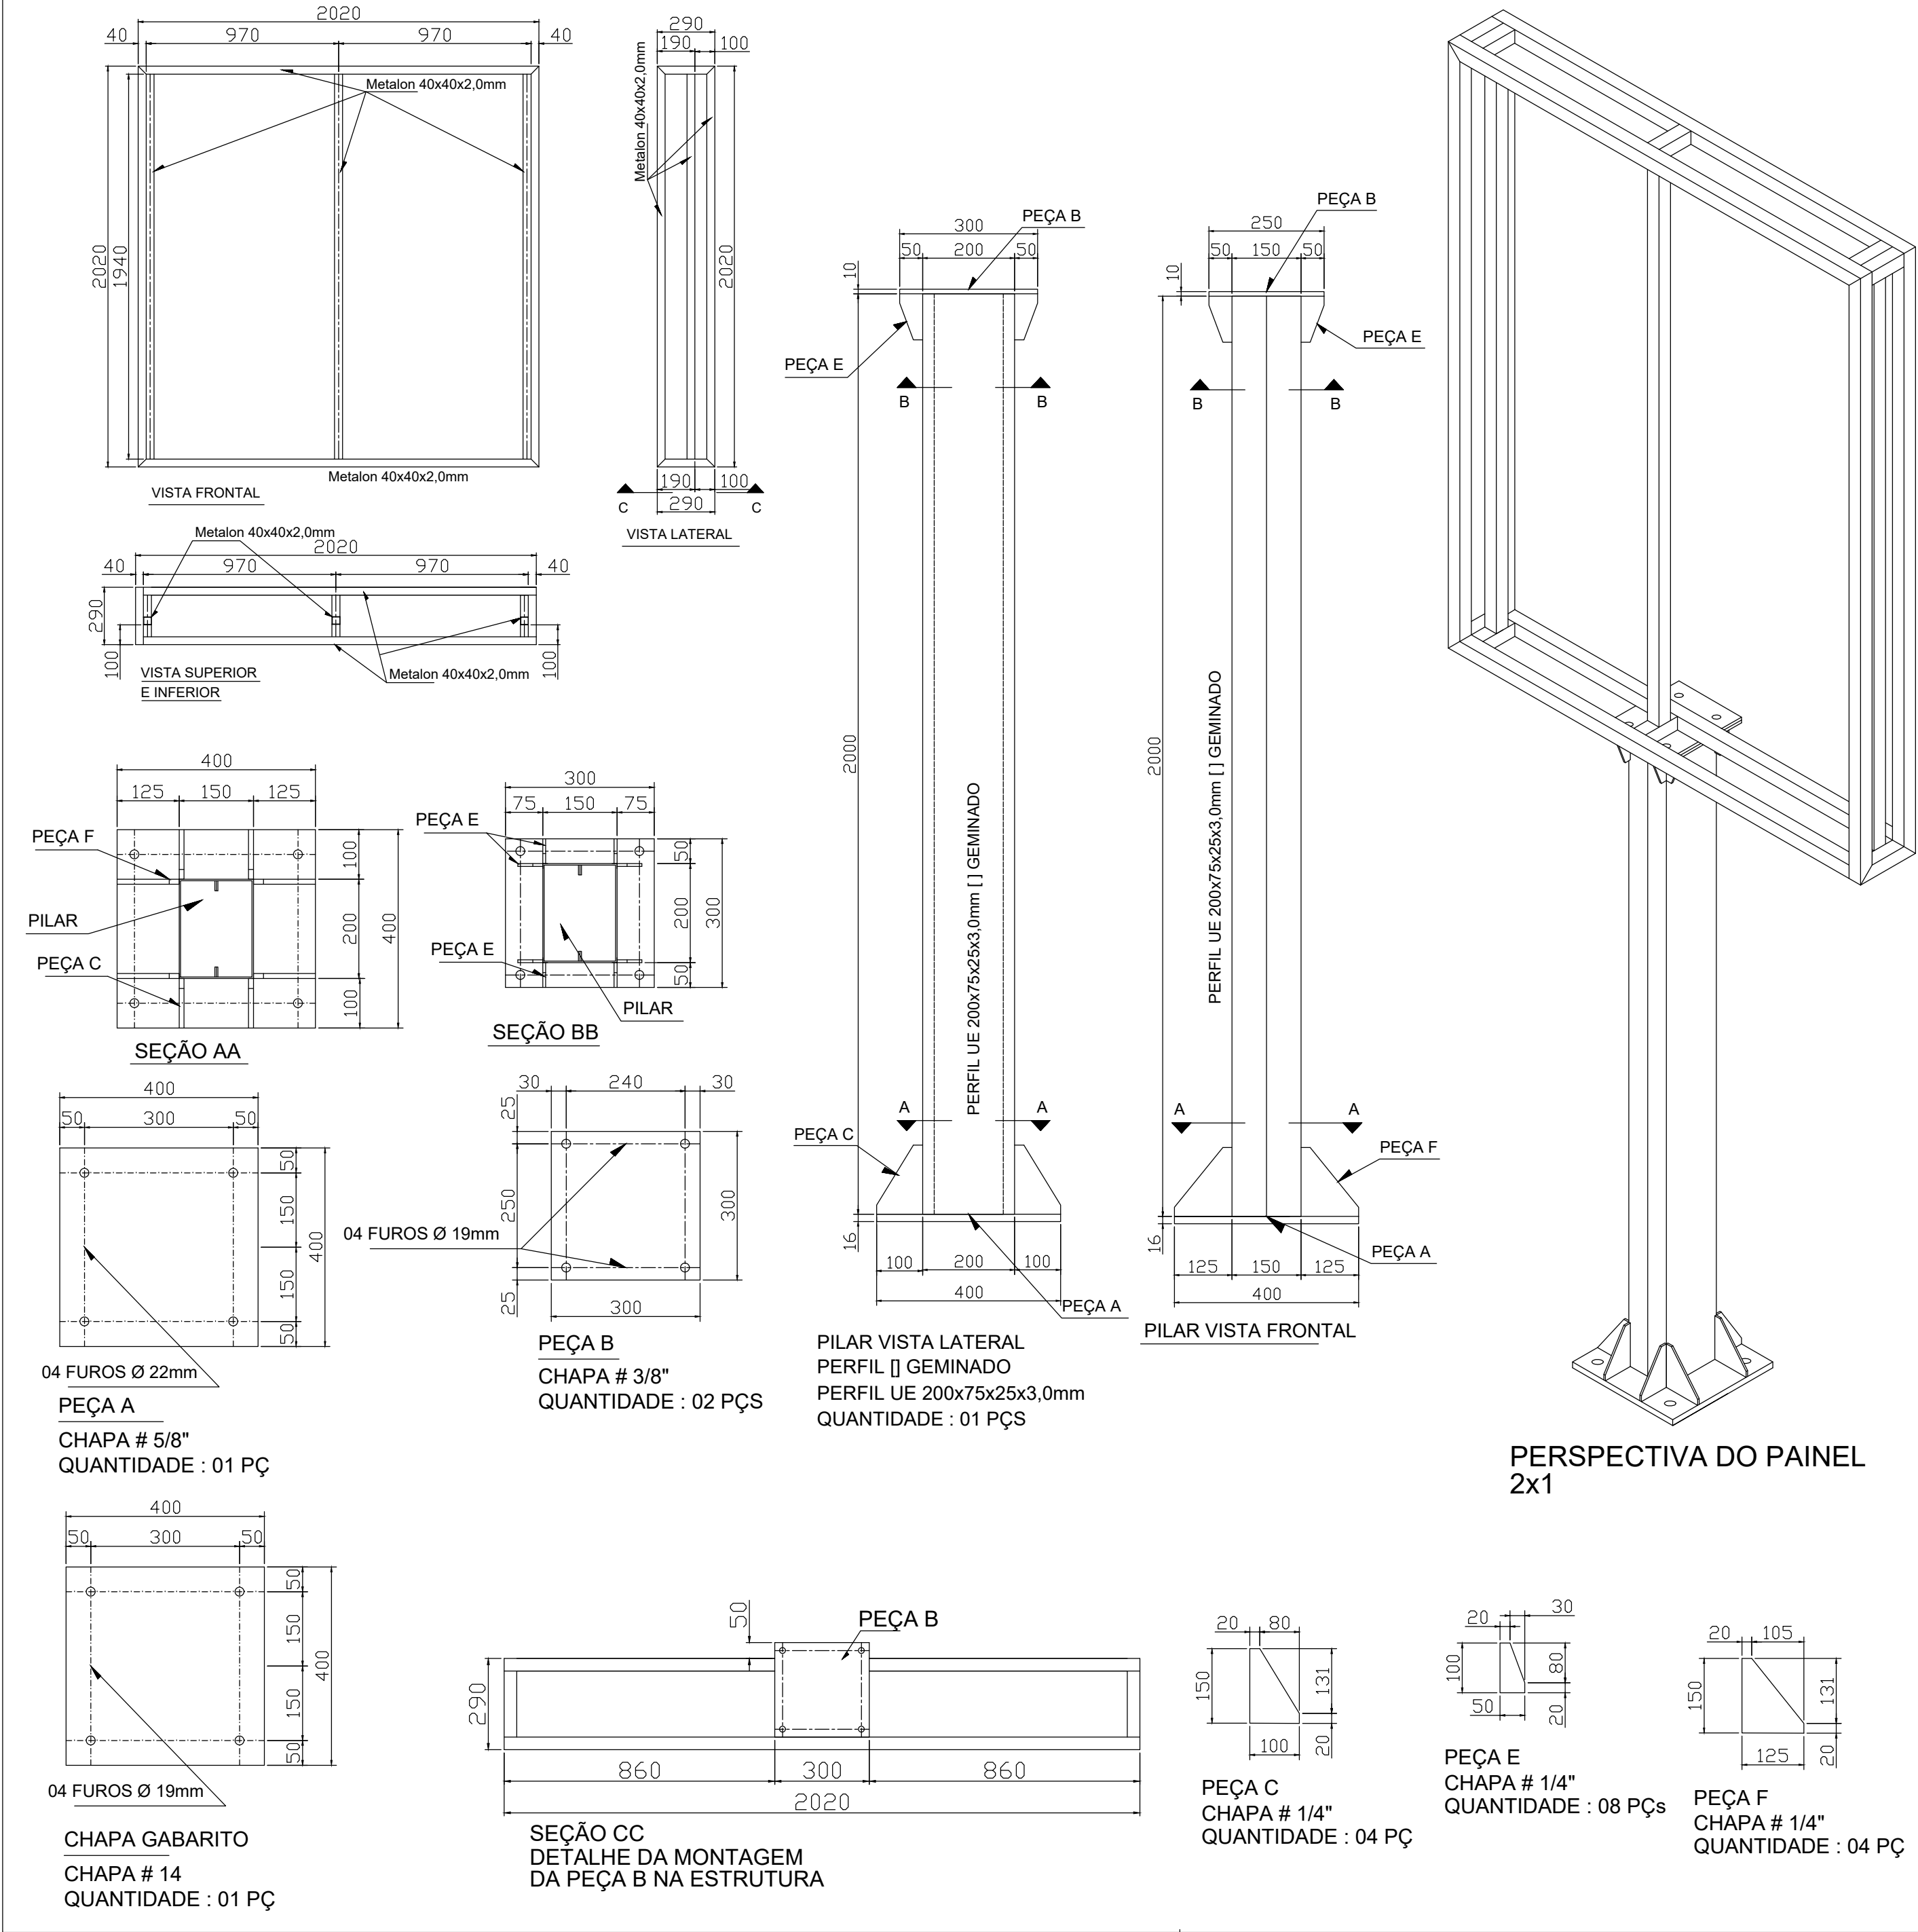

LISTA DE MATERIAIS						
Cliente: THIAGO				DATA: 21/09/2023		
Obra: PAINEL 2x2 OUTDOOR GB RENTAL- PILAR 2,0 METROS						
	ESTRUTURA METÁLICA					
POS.	DESCRIÇÃO	COMPR.	UNID.	QUANT.	PESO UNIT.	PESO TOTAL
1	METALON 40x40x2,0mm	6000mm	PÇS	05	2,41 KG/M	72,30 KG
2	CHAPA # 5/8" x 400 mm (PEÇA A)	400mm	PÇS	01	125,40 KG/M2	20,00 KG
3	CHAPA # 3/8" x 300 mm (PEÇA B)	300mm	PÇS	02	74,48 KG/M2	13,40 KG
4	CHAPA # 1/4" x 100 mm (PEÇA C)	150mm	PÇS	04	49,40 KG/M2	3,00 KG
5	CHAPA # 1/4" x 50 mm (PEÇA E)	100mm	PÇS	08	49,40 KG/M2	2,00 KG
6	CHAPA # 1/4" x 125 mm (PEÇA F)	150mm	PÇS	04	49,40 KG/M2	3,70 KG
7	PERFIL UE 200x75x25x3,0mm (PILAR)	2000mm	PÇS	02	9,00 KG/M	36,00 KG
8	CHAPA # 14 x 400 mm (GABARITO)	400mm	PÇS	01	16,00 KG/M2	2,56 KG
9	BARRA ROSQUEADA ø 3/4" (CHUMBADORES)	1000mm	PÇS	04	2,24 KG/M	9,00 KG
10	CHAPA # 3/8" x 100mm (PEÇA 03)	100mm	PÇS	04	74,48 KG/M2	3,00 KG
11	PARAFUSO SEXTAVADO ø 5/8"(COMPLETO)	2"	PÇS	04	////	////
12	PORCA SEXTAVADA ø 3/4"	////	PÇS	08	////	////
13	ARRUELA LISA ø 3/4"	////	PÇS	04	////	////
PESO TOTAL GERAL :						164,96 KG

NOTAS: MEDIDAS EM MILIMETRO;

4				
3				
2				
1				
0	INICIAL	F.G.S		21/09/23
N°	DESCRIÇÃO	DES.	RESP.	DATA

LED EXPERT

PROJETO SOMENTE PARA ORÇAMENTO
NÃO UTILIZAR PARA FABRICAÇÃO

OBRA			Data:	Desenhista:	
PAINEL 2 x 2 GB RENTAL OUTDOOR			21-09-2023	FABIAN	
CONTÉM:					
PROJETO DE ESTRUTURA METÁLICA – PILAR 2,0 METROS					
ESCALA	SE	R.T.:	N° LED EXPERT:		FORMATO: REVISÃO
IND.	--	--	193-2023-09-FL-01		A2 00