

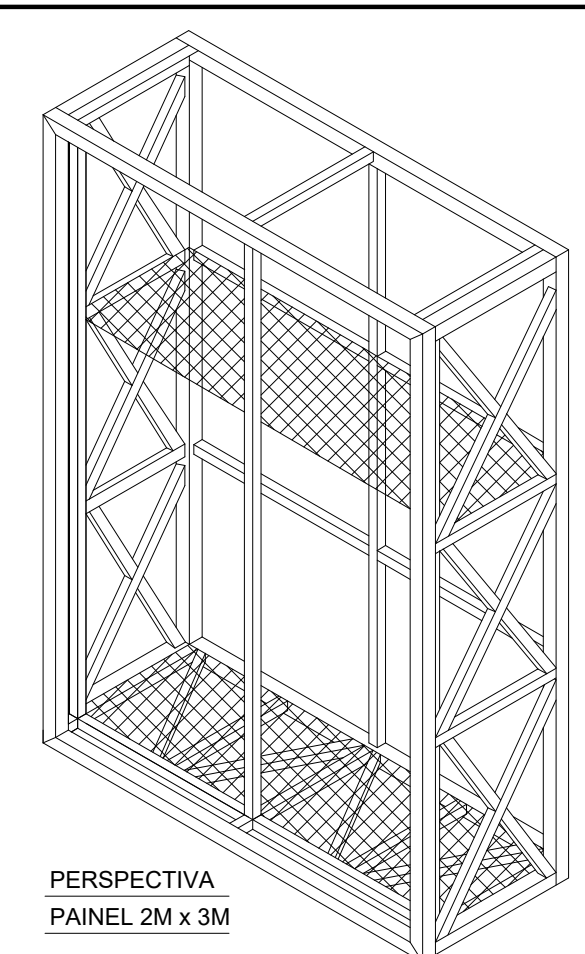


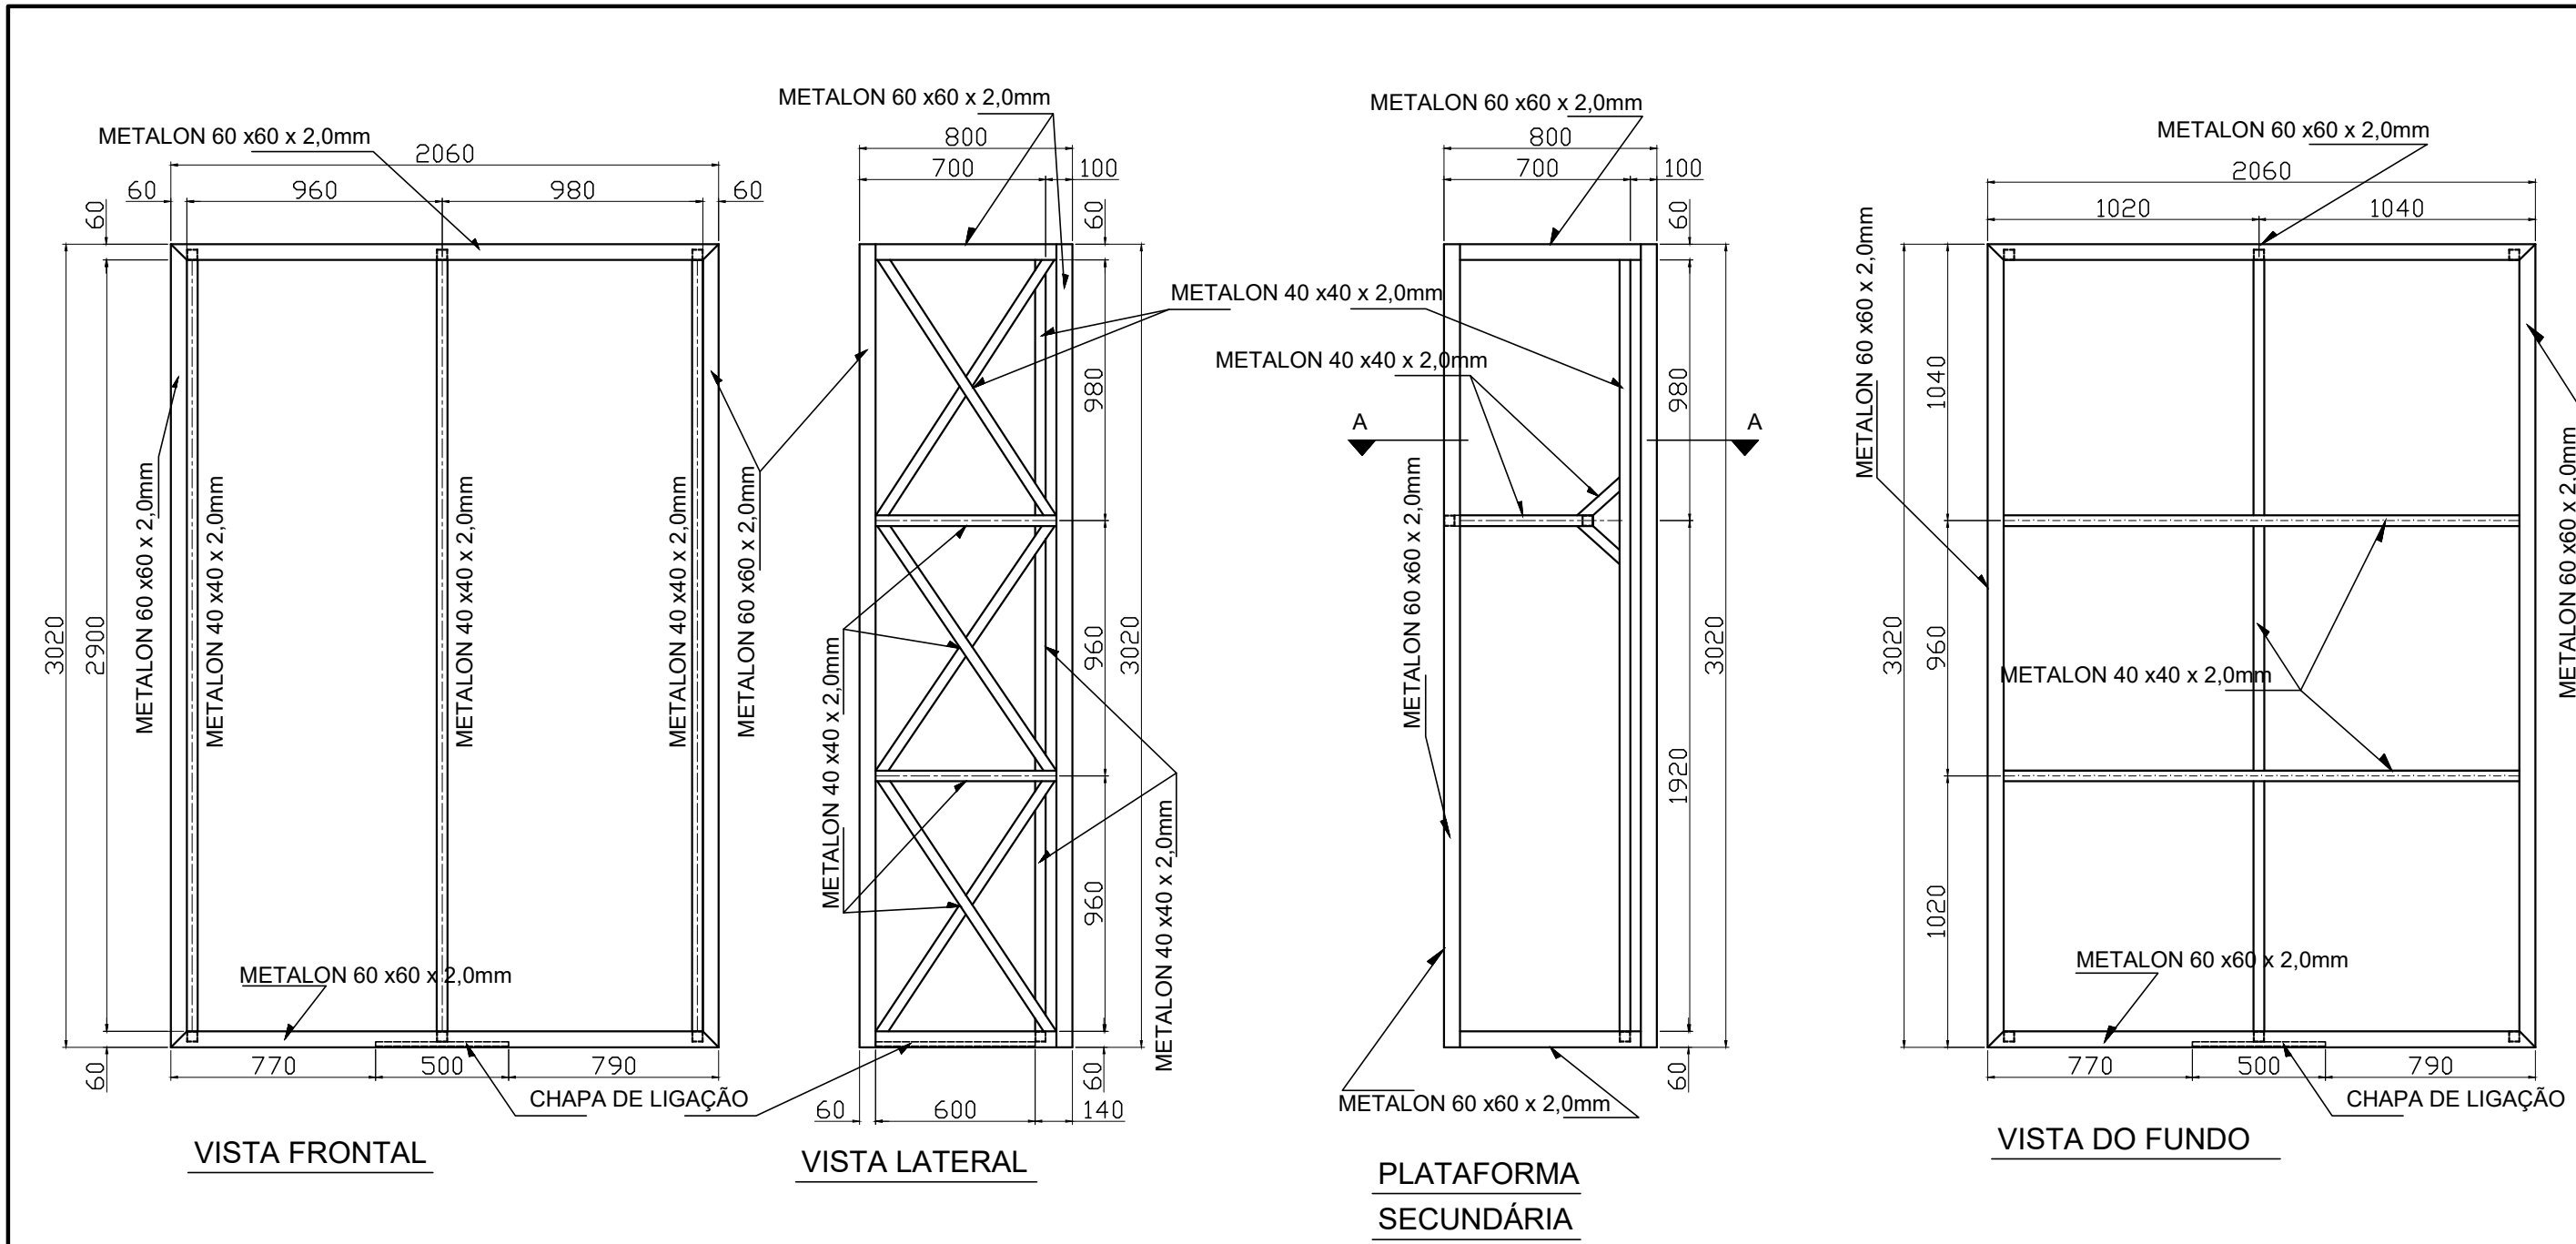

LISTA DE MATERIAIS							
Cliente: RAPHAEL				DATA: 21/03/2023			
Obra: PAINEL 2x4 GB RENTAL OUTDOOR							
	ESTRUTURA METÁLICA						
	DESCRIÇÃO	COMPR.	UNID.	QUANT.	PESO UNIT.	PESO TOTAL	
01	METALON 60x60x2,0mm	6000mm	PÇS	04	3,61 KG/M	86,64 KG	
02	METALON 40x40x2,0mm	6000mm	PÇS	09	2,41 KG/M	130,14 KG	
03	CHAPA EXPANDIDA # 1/8" x 600mm(PISO 01)	1940mm	PÇS	01	4,2 KG/M2	4,88 KG	
04	CHAPA EXPANDIDA # 1/8" x 530mm(PISO 02)	1940mm	PÇS	01	4,2 KG/M2	4,31 KG	
05	CHAPA # 3/8" x 200mm (PEÇA A)	250mm	PÇS	04	74,5 KG/M2	14,90 KG	
06	CHAPA # 1/4" x 150mm (PEÇA B)	250mm	PÇS	08	49,39 KG/M2	14,80 KG	
07	CHAPA # 3/8" x 150mm (PEÇA C)	250mm	PÇS	04	74,5 KG/M2	11,17 KG	
08	FERRO REDONDO Ø 3/4" (CHUMBADOR)	1000mm	PÇS	08	2,24 KG/M	18,00 KG	
09	CHAPA # 3/8" x 100mm (PEÇA 03)	100mm	PÇ	08	74,5 KG/M2	5,96 KG	
10	CHAPA # 5/8" x 500mm (BASE)	500mm	PÇ	01	125,44 KG/M2	31,36 KG	
11	CHAPA # 1/2" x 500mm (LIGAÇÃO)	600mm	PÇS	02	98,00 KG/M2	58,80 KG	
12	CHAPA # 14 x 500mm (GABARITO)	500mm	PÇ	01	16,00 KG/M2	4,00 KG	
13	VIGA W 200x19,3 (PILAR)	2000mm	PÇS	02	19,30 KG/M	77,20 KG	
PESO TOTAL GERAL :					462,16 KG		




NOTAS: MEDIDAS EM MILIMETRO;				
4				
3				
2				
1				
0	INICIAL	F.G.S		21/03/23
N°	DESCRIÇÃO	DES.	RESP.	DATA

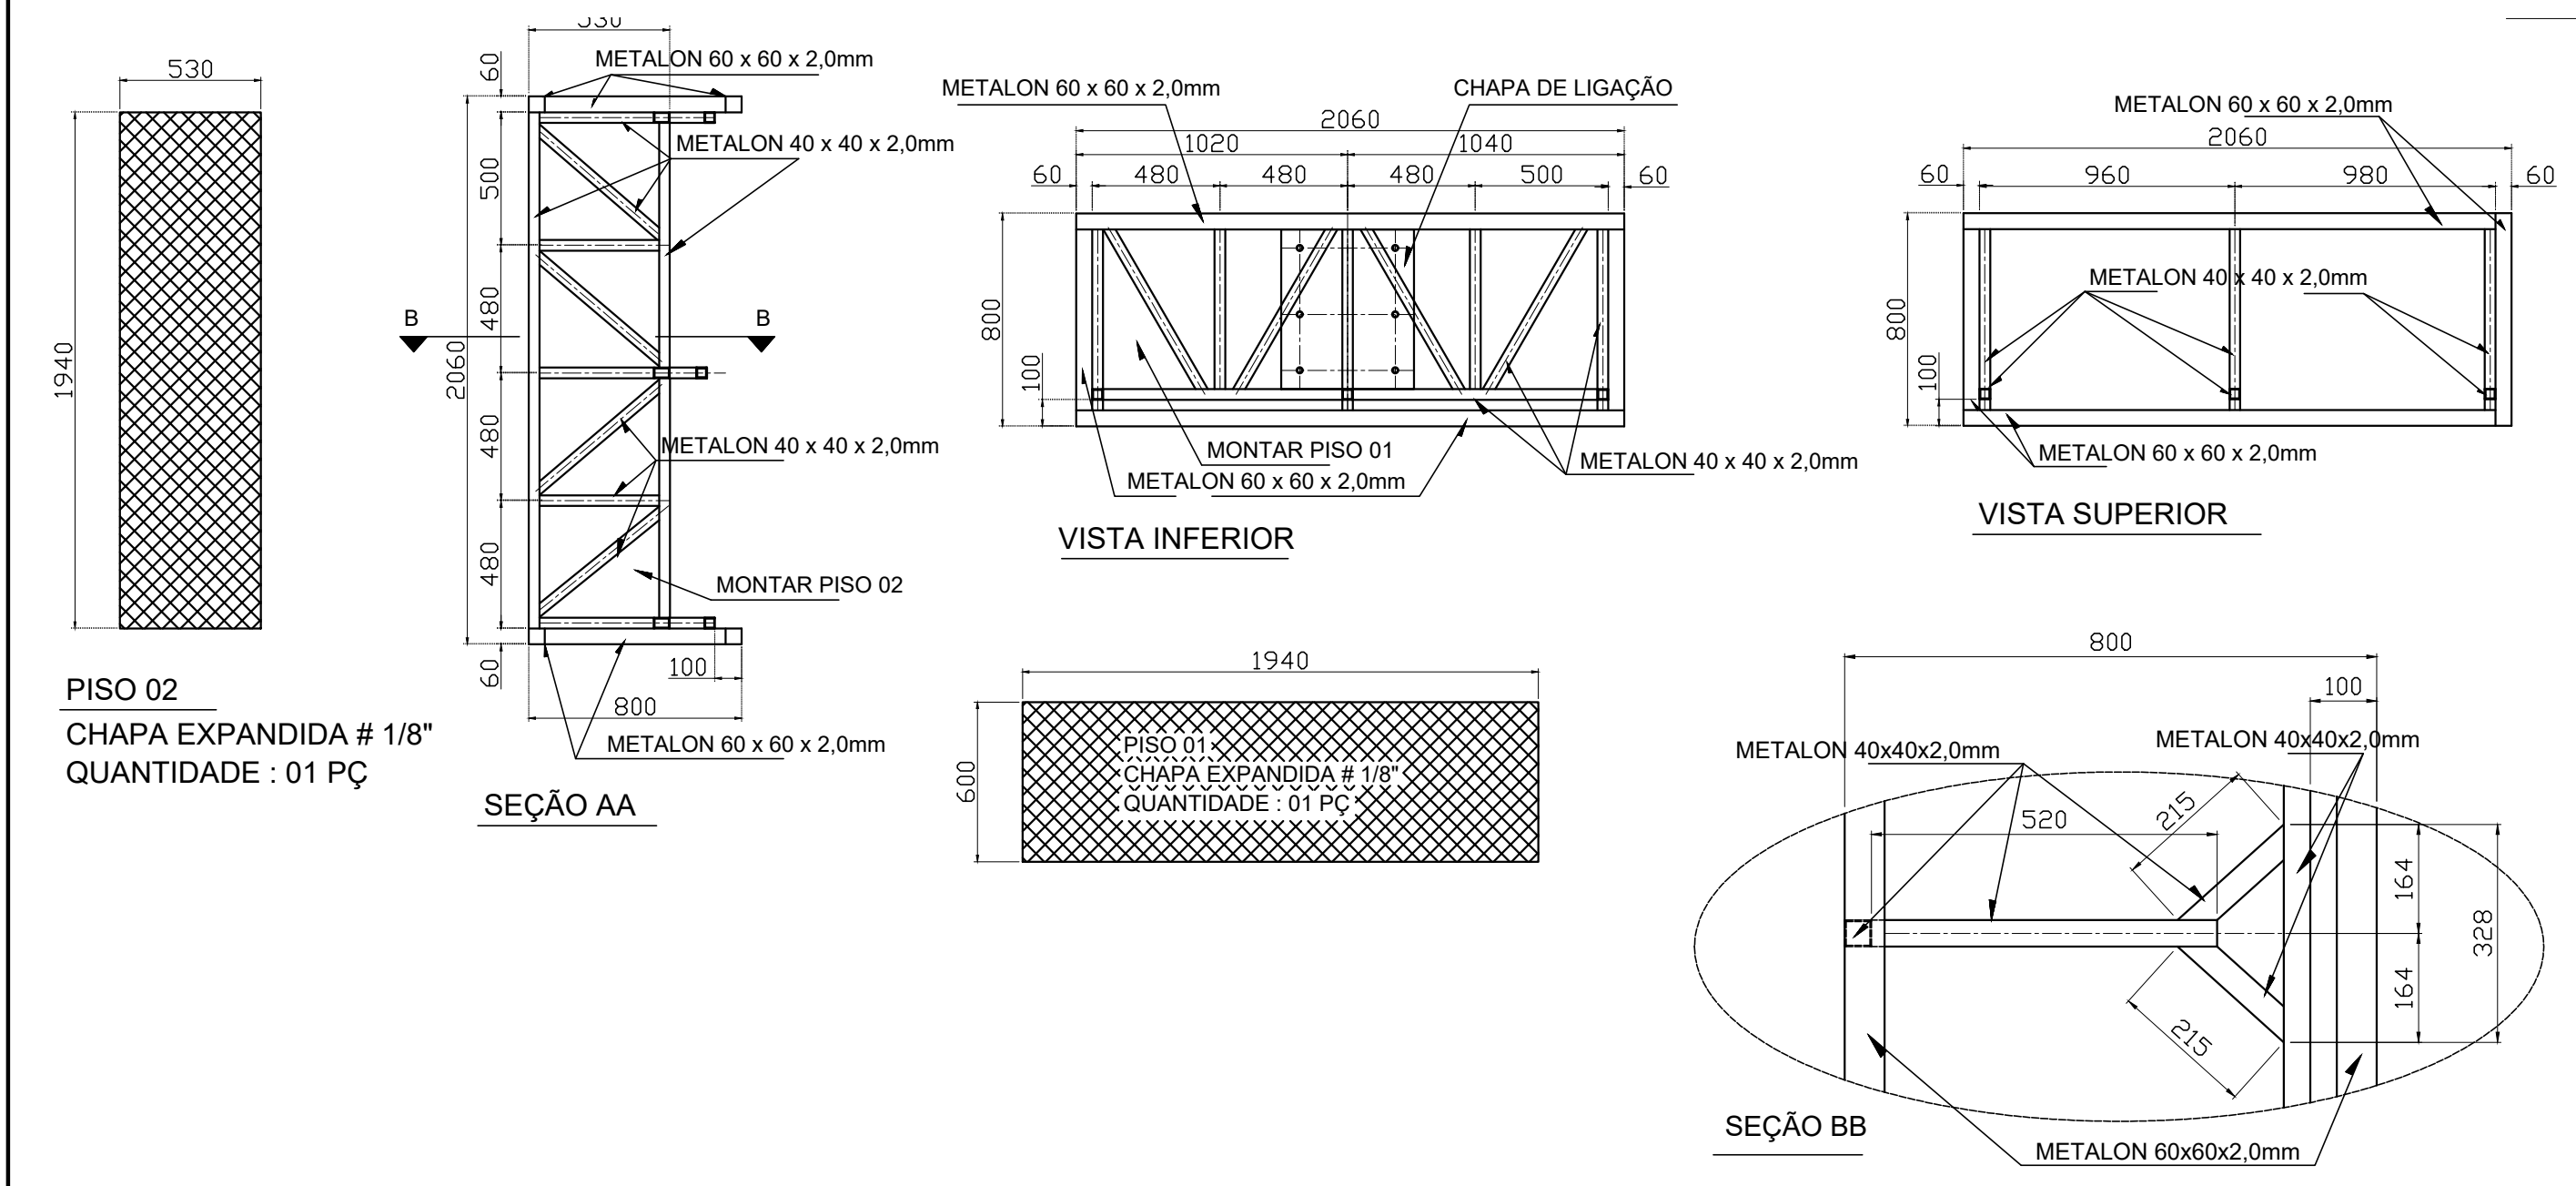


PROJETO SOMENTE PARA ORÇAMENTO

NAO UTILIZAR PARA FABRICAÇÃO


OBRA		Data:	Desenhista:			
PAINEL 2 x 3 GB RENTAL OUTDOOR		21-03-2023				
CONTÉM:						
PROJETO DE ESTRUTURA METÁLICA						
ESCALA	SE	R.T.:	FORMATO:	REVISÃO		
IND.	--	--	102-2023-03-FL01	A2 00		

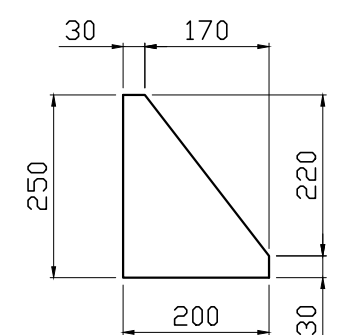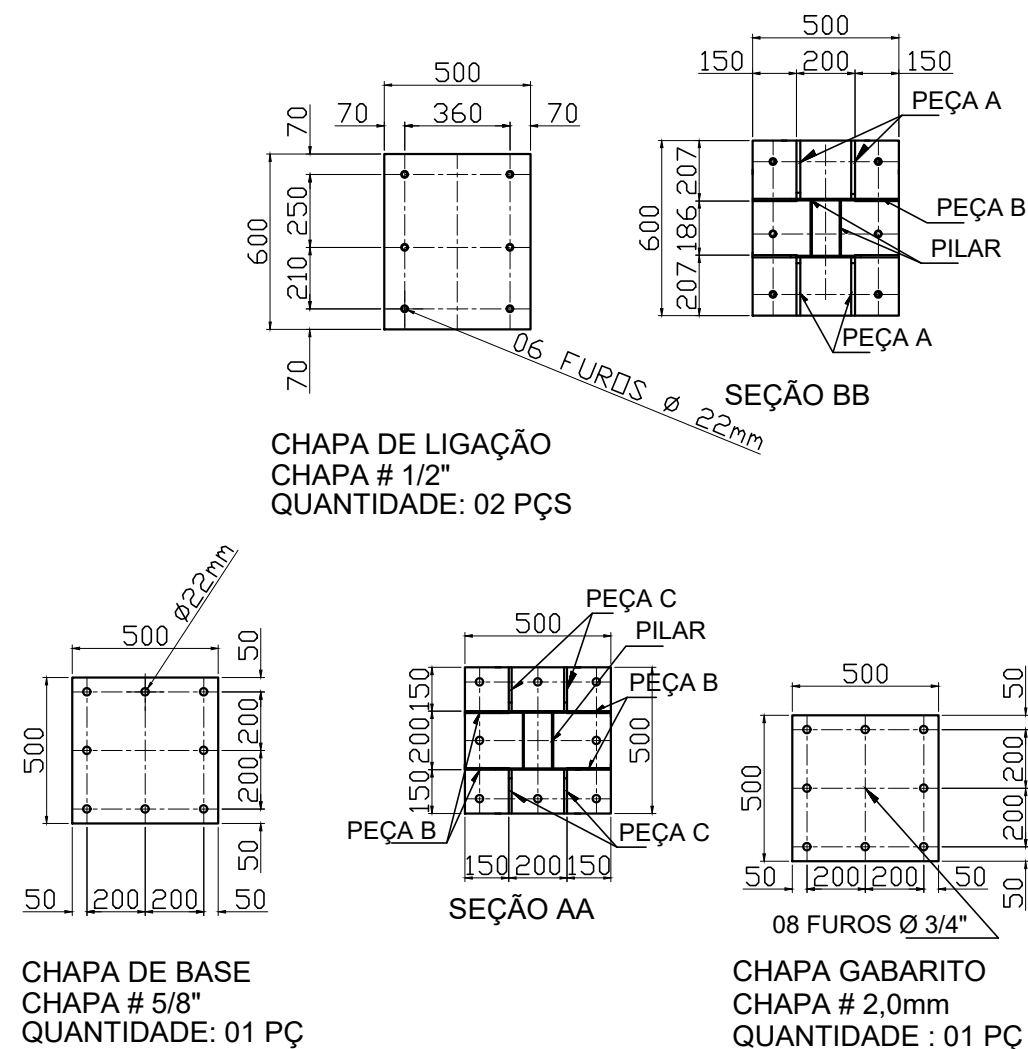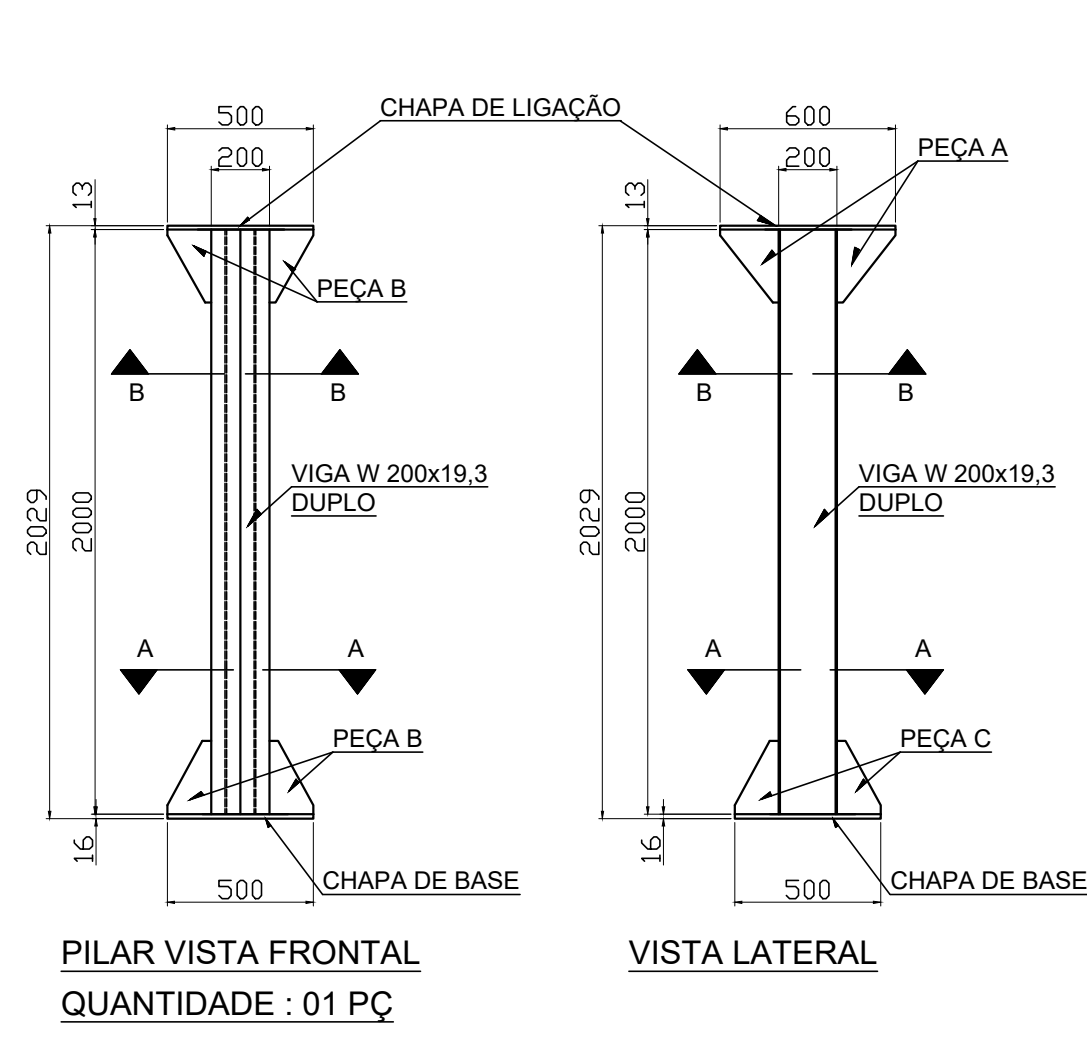


PEÇA A
CHAPA #3/8"
QUANTIDADE : 04 PÇS

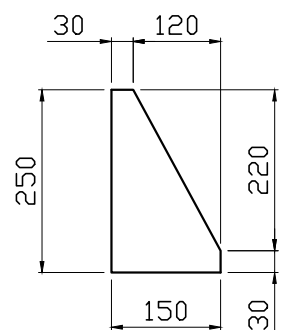


PEÇA B
CHAPA #1/4"
QUANTIDADE : 08 PÇS

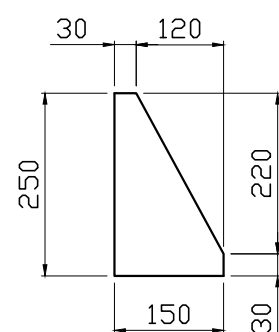

PEÇA C
CHAPA #3/8"
QUANTIDADE : 04 PÇS

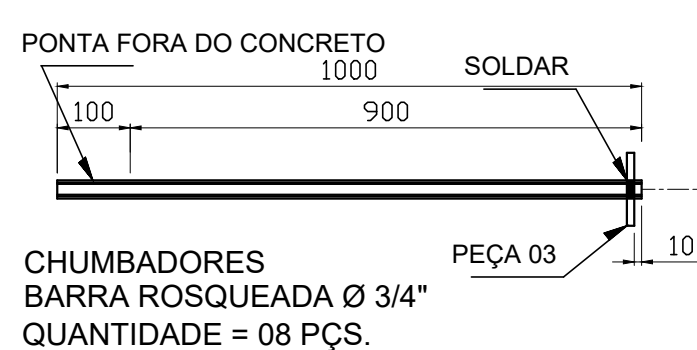

CHUMBADORES
BARRA ROSQUEADA Ø 3/4"
QUANTIDADE = 08 PÇS.

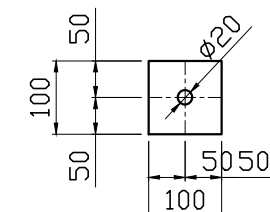

PEÇA 03
CHAPA # 3/8"
QUANTIDADE = 08 PÇS.

NOTAS: MEDIDAS EM MILIMETRO;

4				
3				
2				
1				
0	INICIAL	F.G.S		21/03/23
N°	DESCRIÇÃO	DES.	RESP.	DATA

**PROJETO SOMENTE PARA ORÇAMENTO
NAO UTILIZAR PARA FABRICAÇÃO**

OBRA PAINEL 2 x 3 GB RENTAL OUTDOOR			Data: 21-03-2023	Desenhista: FLAB AN	
CONTÉM: PROJETO DE ESTRUTURA METÁLICA (PILAR)					
ESCALA IND.	SE --	R.T.: --	102-2023-03-FL02	FORMATO: A2	REVISÃO 00