




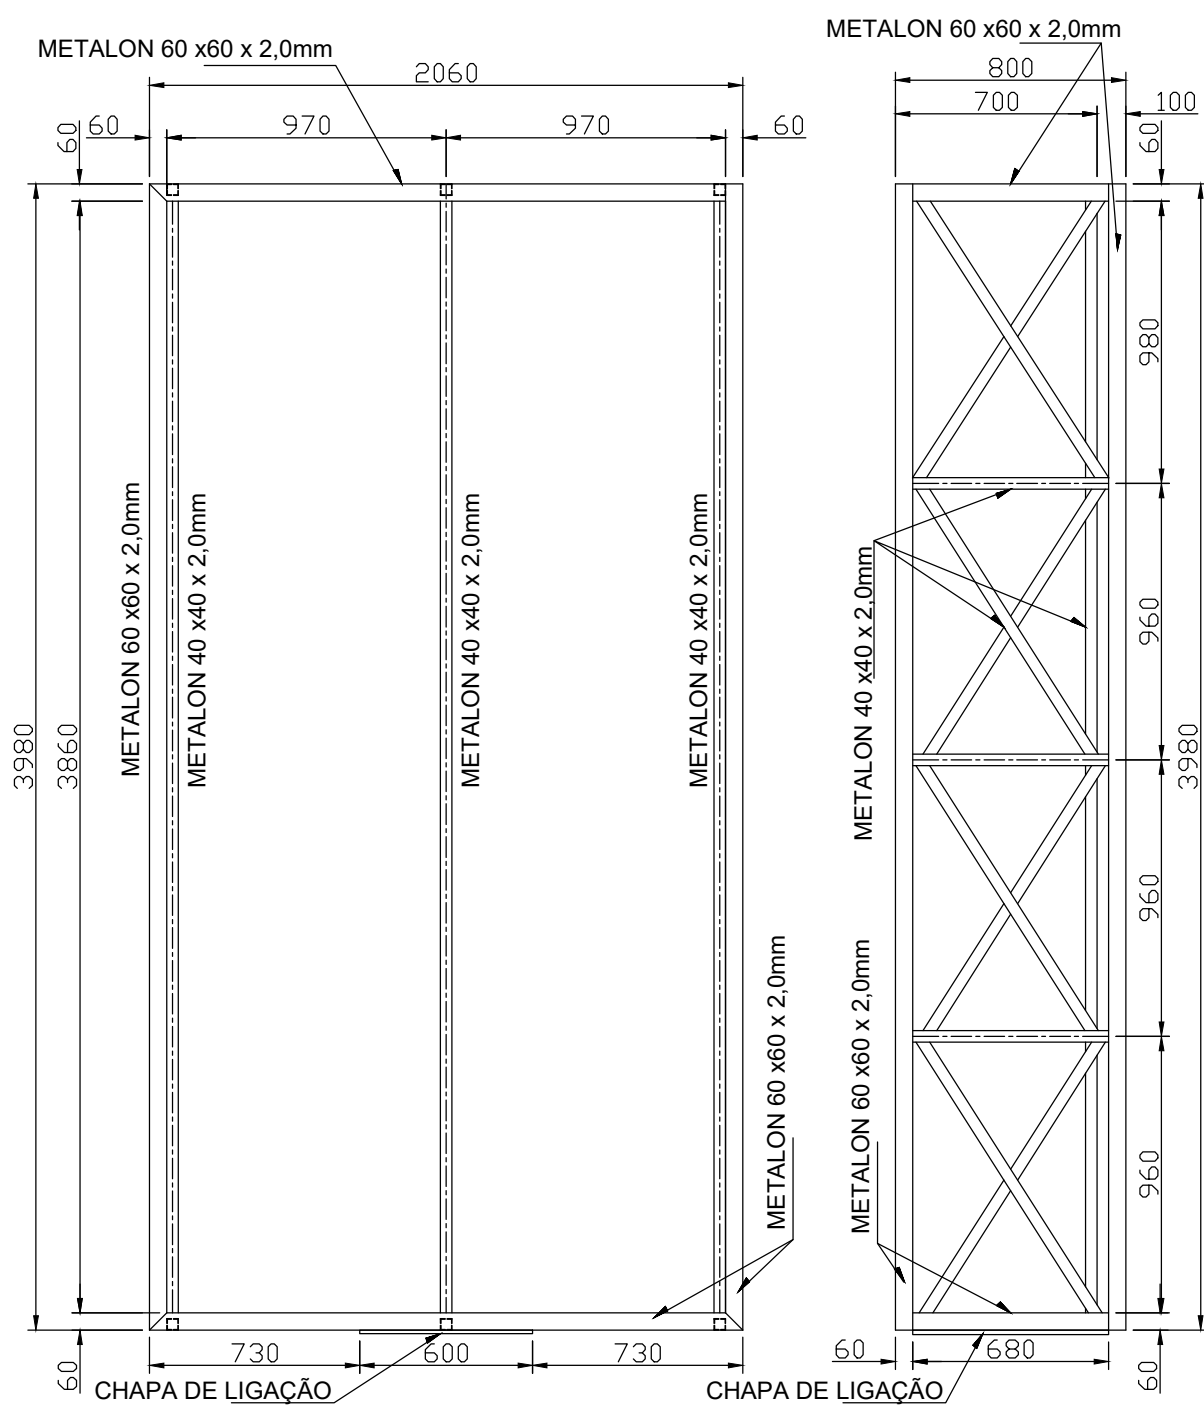


VISTA FRONTAL

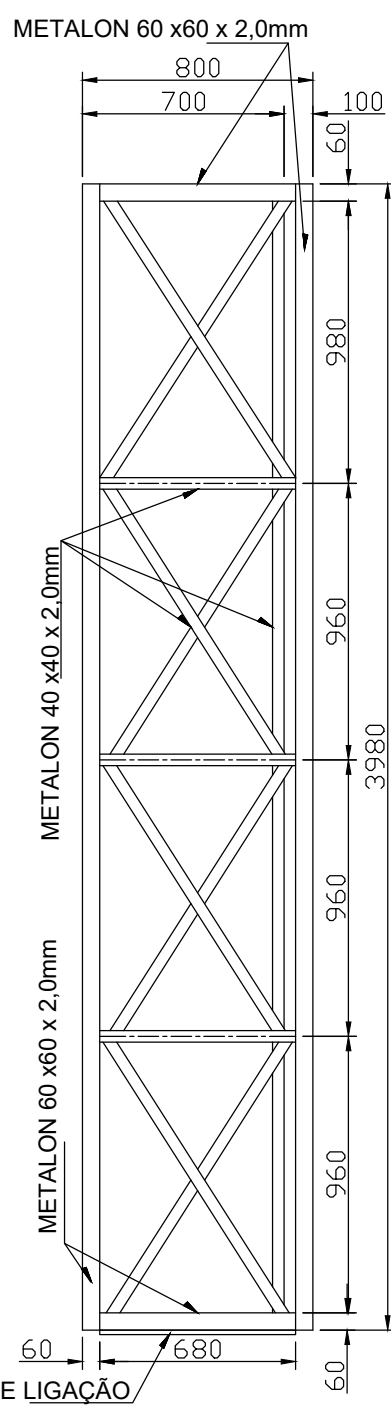


VISTA LATERAL

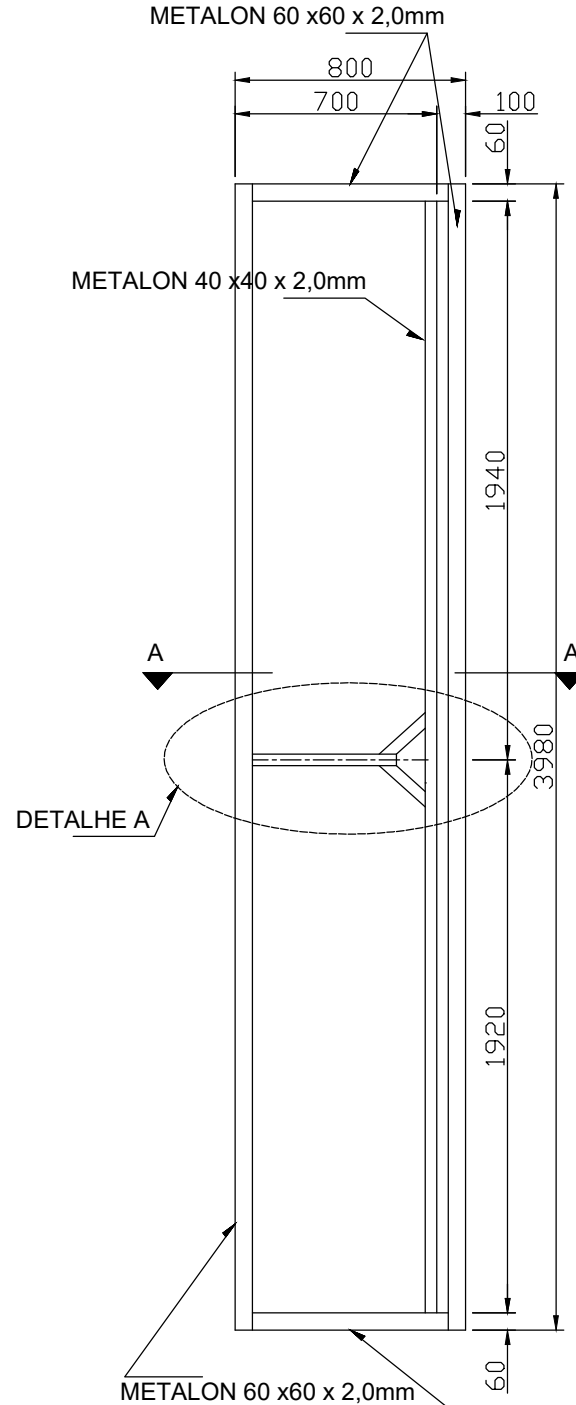


PLATAFORMA
SECUNDÁRIA

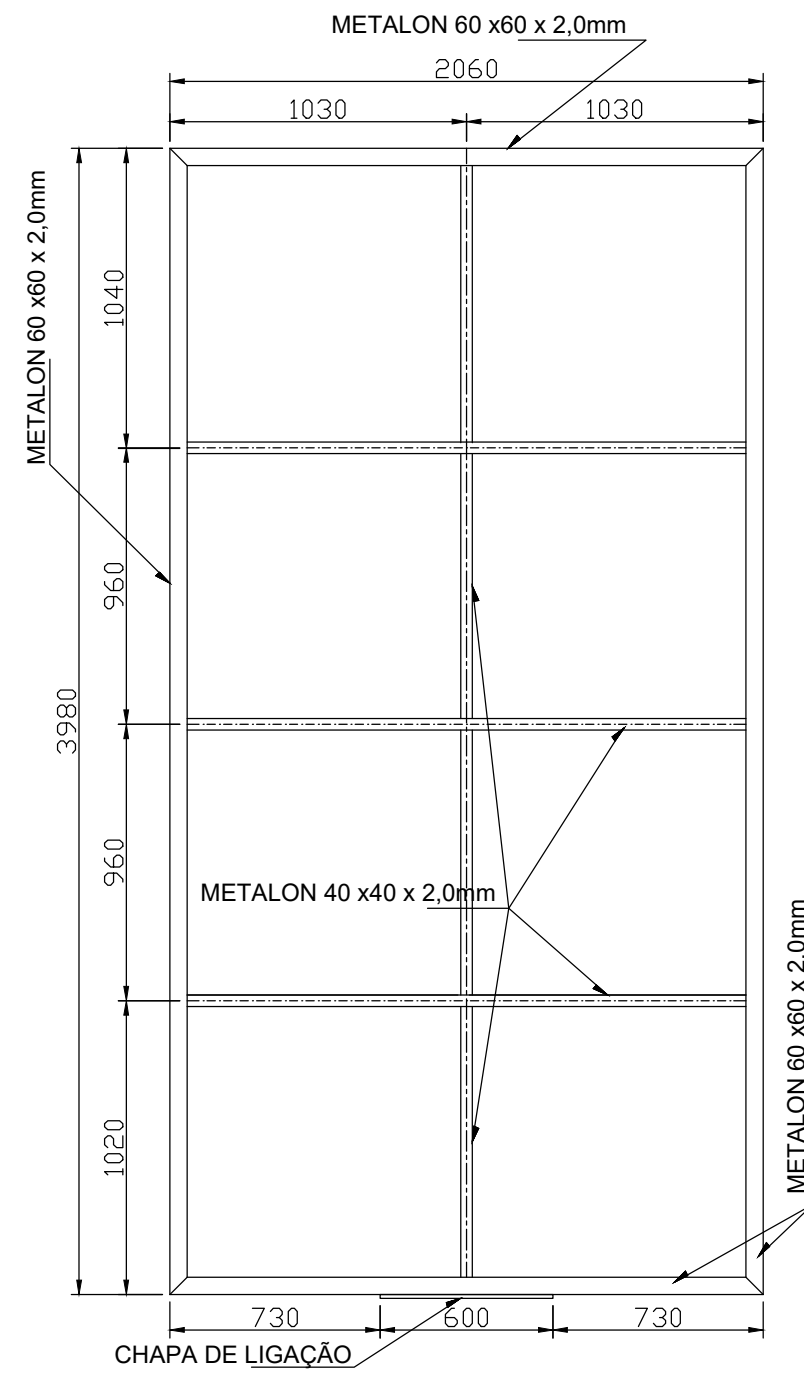


VISTA DO FUNDO

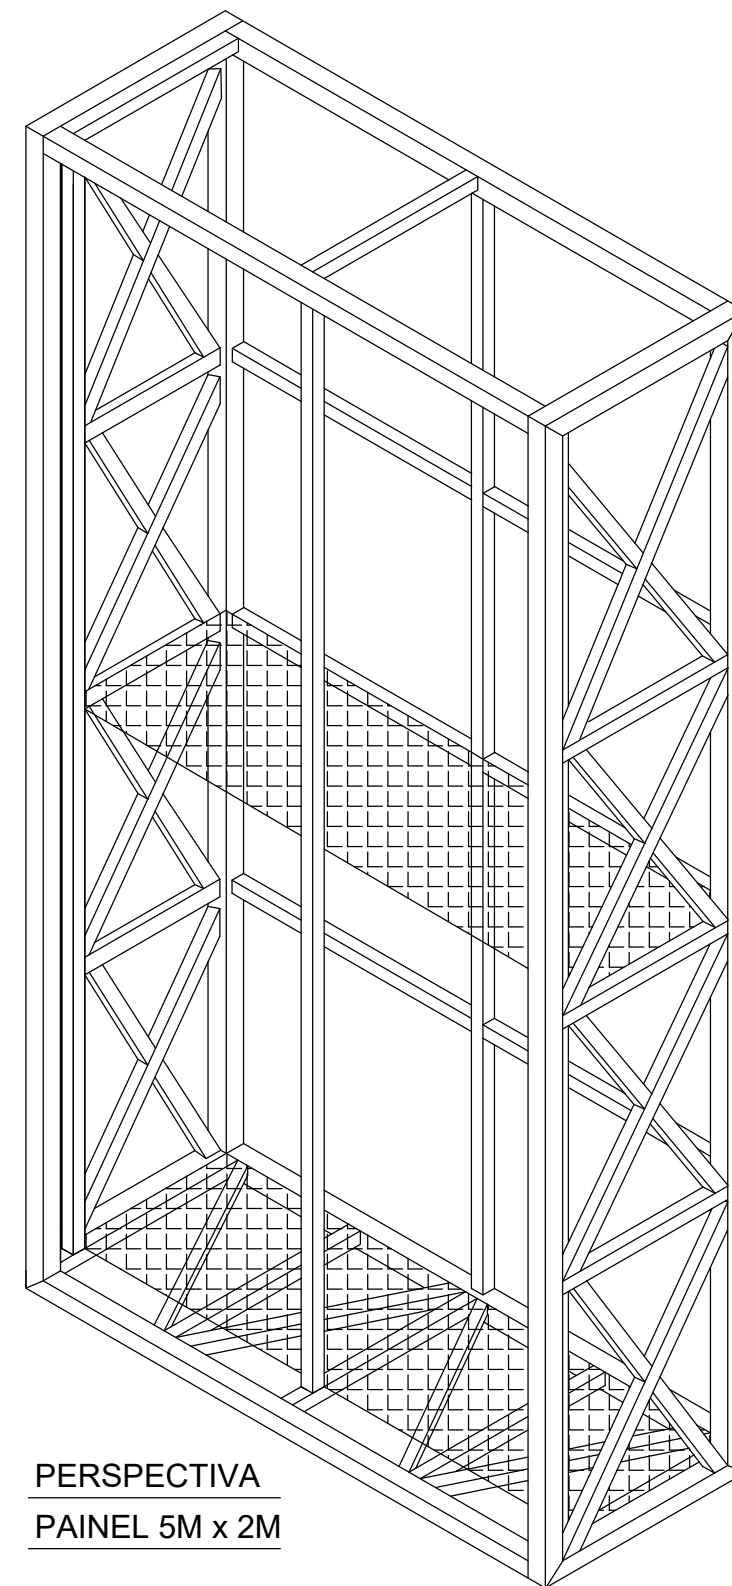


PERSPECTIVA
PAINEL 5M x 2M

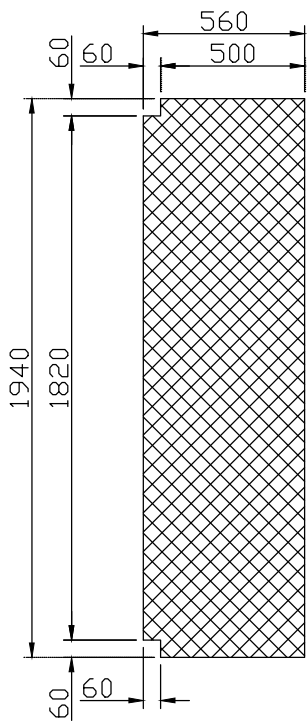



PISO 02
CHAPA EXPANDIDA # 1/8"
QUANTIDADE : 01 PÇ

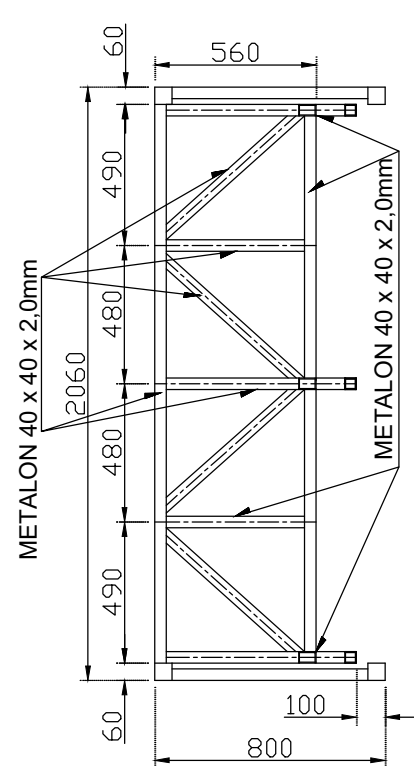


SEÇÃO AA

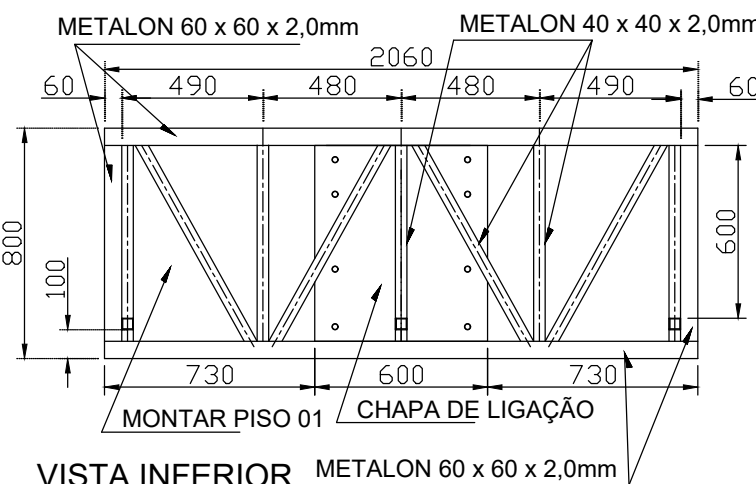

VISTA INFERIOR

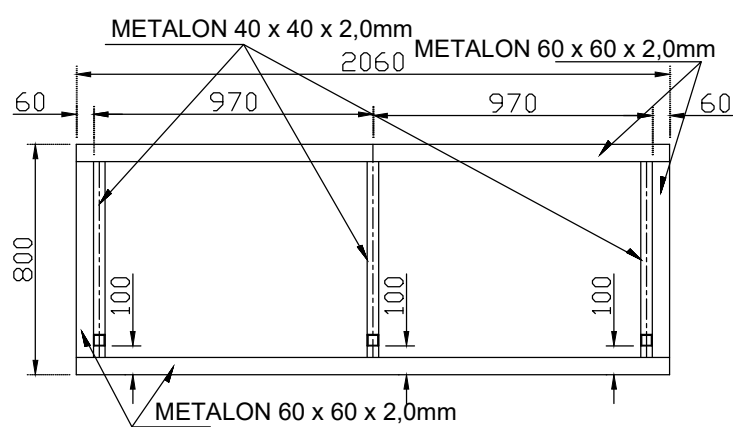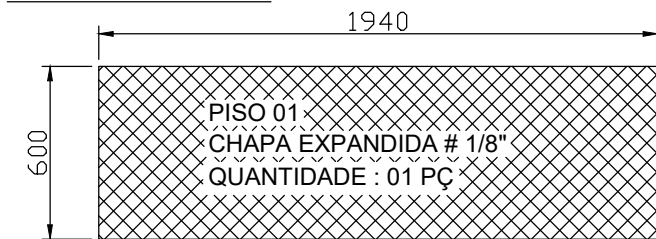

VISTA SUPERIOR

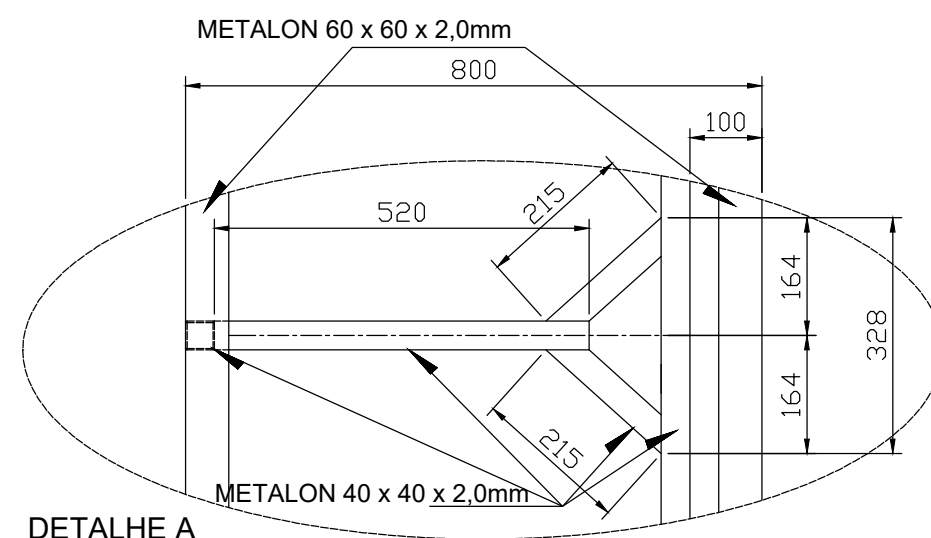

DETALHE A


LISTA DE MATERIAIS						
Cliente: JOSÉ AUGUSTO ATHAIDE				DATA: 10/04/2024		
Obra: PAINEL 2x4 GB RENTAL OUTDOOR POSTE 2,0 METROS						
	ESTRUTURA METÁLICA					
POS.	DESCRIÇÃO	COMPR.	UNID.	QUANT.	PESO UNIT.	PESO TOTAL
01	METALON 60x60x2,0mm	6000mm	PÇS	05	3,66 KG/M	109,80 KG
02	METALON 40x40x2,0mm	6000mm	PÇS	12	2,41 KG/M	173,52 KG
03	CHAPA EXPANDIDA # 1/8" x 600mm (PISO 01)	1940mm	PÇS	01	4,2 KG/M2	4,88 KG
04	CHAPA EXPANDIDA # 1/8" x 560mm (PISO 02)	1940mm	PÇS	01	4,2 KG/M2	4,56 KG
05	CHAPA BASE # 1" ø 680mm	ø 680mm	PÇS	01	196,00 KG/M2	71,14 KG
06	CHAPA DE LIGAÇÃO # 5/8" x 600mm	680mm	PÇS	02	125,44 KG/M2	102,35 KG
07	CHAPA # 3/8" x 140mm (PEÇA A)	250mm	PÇS	08	74,48 KG/M2	10,42 KG
08	CHAPA # 3/8" x 130mm (PEÇA B)	200mm	PÇS	08	74,48 KG/M2	7,74 KG
09	CHAPA # 1/4" x 1200mm (PILAR)	2000mm	PÇS	01	49,39 KG/M2	118,53 KG
10	CHAPA # 14 ø 680mm (GABARITO)	ø 680mm	PÇS	01	16,00 KG/M2	5,80 KG
11	BARRA ROSQUEADA ø 1" (CHUMBADORES)	1000mm	PÇS	08	3,98 KG/M	31,84 KG
12	CHAPA # 3/8" x 100mm (PEÇA 03)	100mm	PÇS	08	74,48 KG/M2	5,95 KG
13						
PESO TOTAL GERAL :						646,53 KG

NOTAS: MEDIDAS EM MILIMETRO; SEGUIR TODAS AS COTAS DO PROJETO.

4				
3				
2				
1				
0	INICIAL	F.G.S		10/04/24
N°	DESCRIÇÃO	DES.	RESP.	DATA


**PROJETO SOMENTE PARA ORÇAMENTO
NAO UTILIZAR PARA FABRICAÇÃO**

OBRA			Data:	Desenhista:		
PAINEL 2 x 4 GB RENTAL OUTDOOR			10-04-2024	FABIAN		
CONTÉM:						
PROJETO DE ESTRUTURA METÁLICA – PILAR 2,0 METROS						
ESCALA	SE	R.T.:	N° LED EXPERT:		FORMATO:	REVISÃO
IND.	--	--	299-2024-04-FL01		A2	00

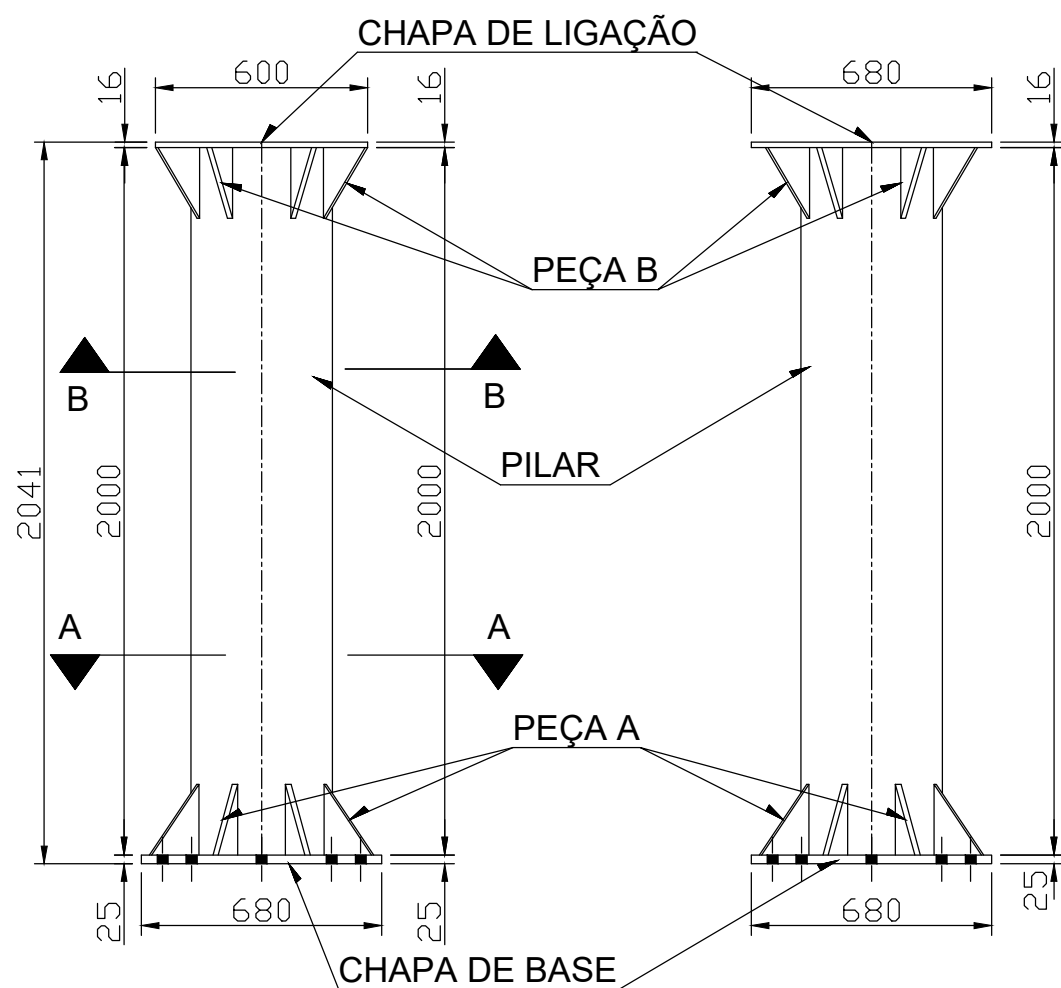


PILAR
VISTA DA FRENTE
QUANTIDADE: 01 PÇ


VISTA LATERAL

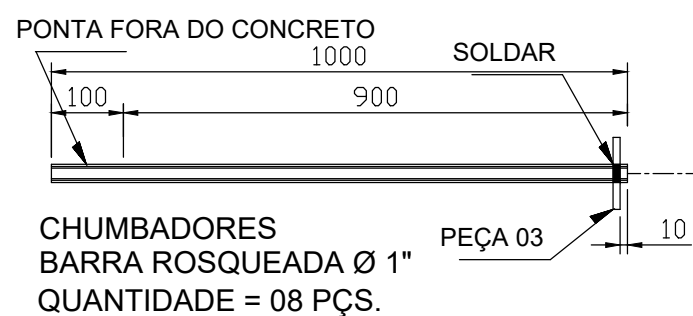


CHUMBADORES
BARRA ROSQUEADA Ø 1"
QUANTIDADE = 08 PÇS.

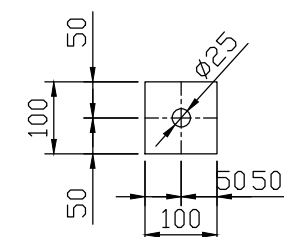


PEÇA 03
CHAPA # 3/8"
QUANTIDADE = 08 PÇS.

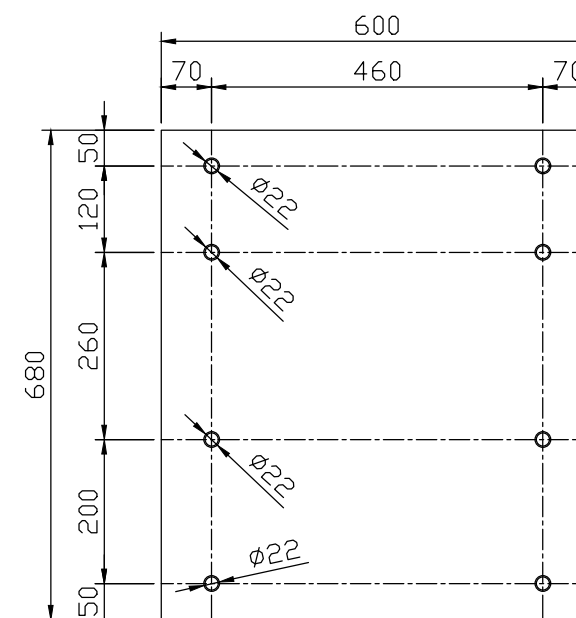


CHAPA DE LIGAÇÃO
CHAPA # 5/8"
QUANTIDADE: 02 PÇS

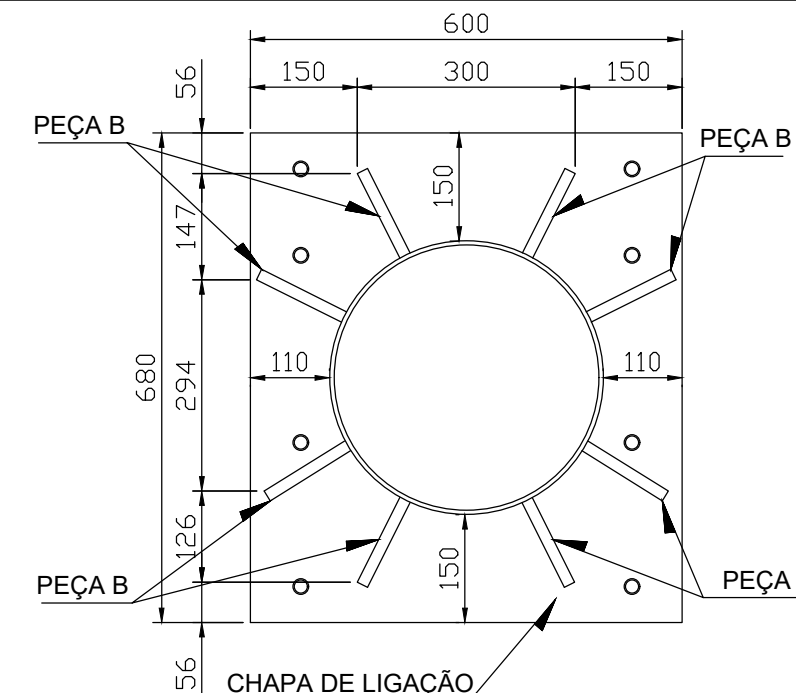


SEÇÃO BB

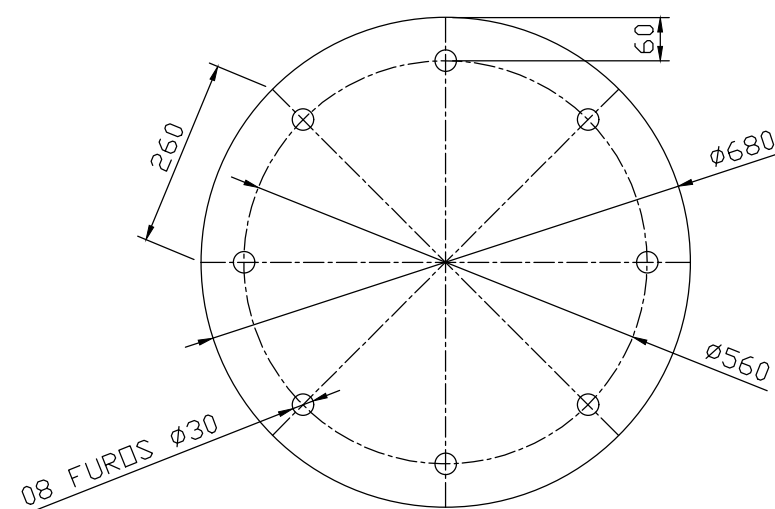


CHAPA DE BASE
CHAPA # 1"
QUANTIDADE: 01 PÇ

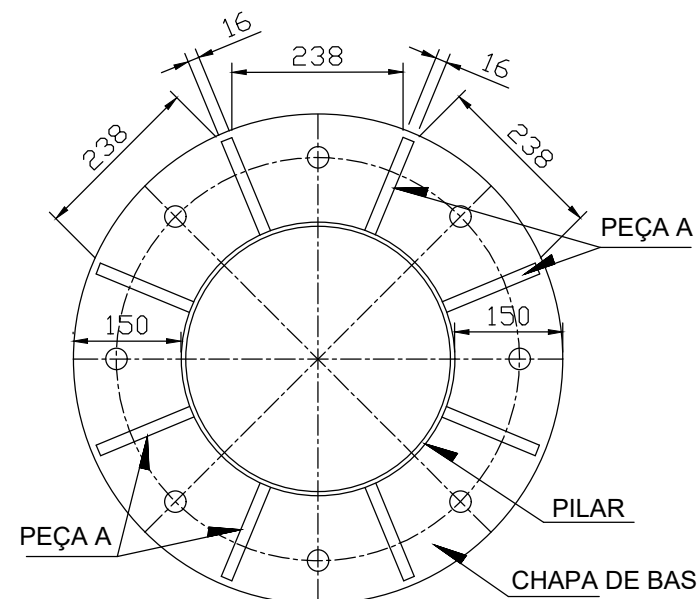



SEÇÃO AA

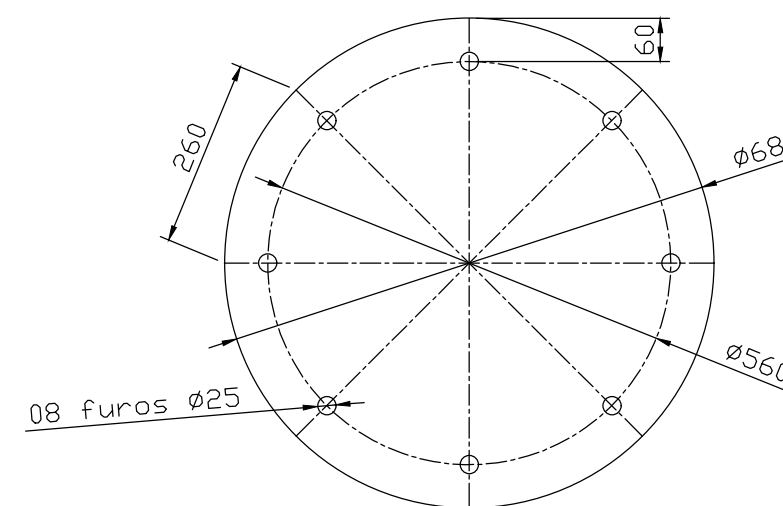


CHAPA GABARITO
CHAPA # 14"
QUANTIDADE: 01 PÇ

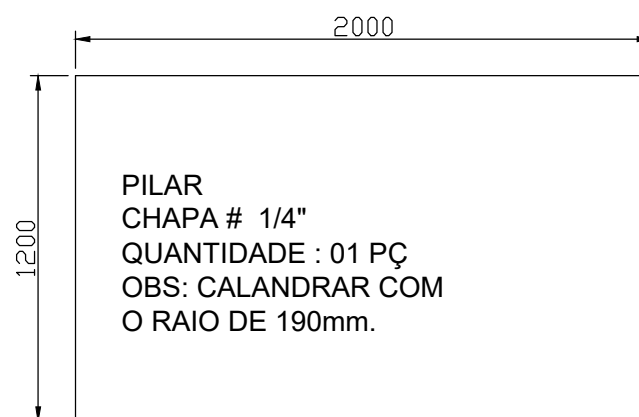

PILAR
CHAPA # 1/4"
QUANTIDADE : 01 PÇ
OBS: CALANDRAR COM
O RAIO DE 190mm.

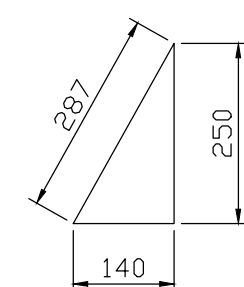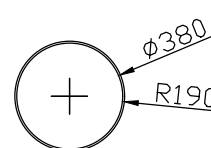

PEÇA A
CHAPA # 3/8"
QUANTIDADE : 08 PÇS

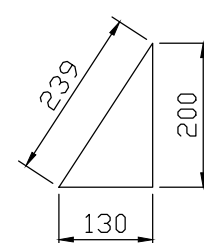

PEÇA B
CHAPA # 3/8"
QUANTIDADE : 08 PÇS

NOTAS: MEDIDAS EM MILIMETRO;

4				
3				
2				
1				
0	INICIAL	F.G.S		10/04/24
N°	DESCRIÇÃO	DES.	RESP.	DATA

**PROJETO SOMENTE PARA ORÇAMENTO
NAO UTILIZAR PARA FABRICAÇÃO**

OBRA PAINEL 2 x 4 GB RENTAL OUTDOOR			Data: 10-04-2024		Desenhista: FABIAN	
CONTÉM: PROJETO DE ESTRUTURA METÁLICA – PILAR 2,0 METROS						
ESCALA IND.	SE --	R.T.: --	N° LED EXPERT: 299-2024-04-FL02		FORMATO: A2	REVISÃO: 00