




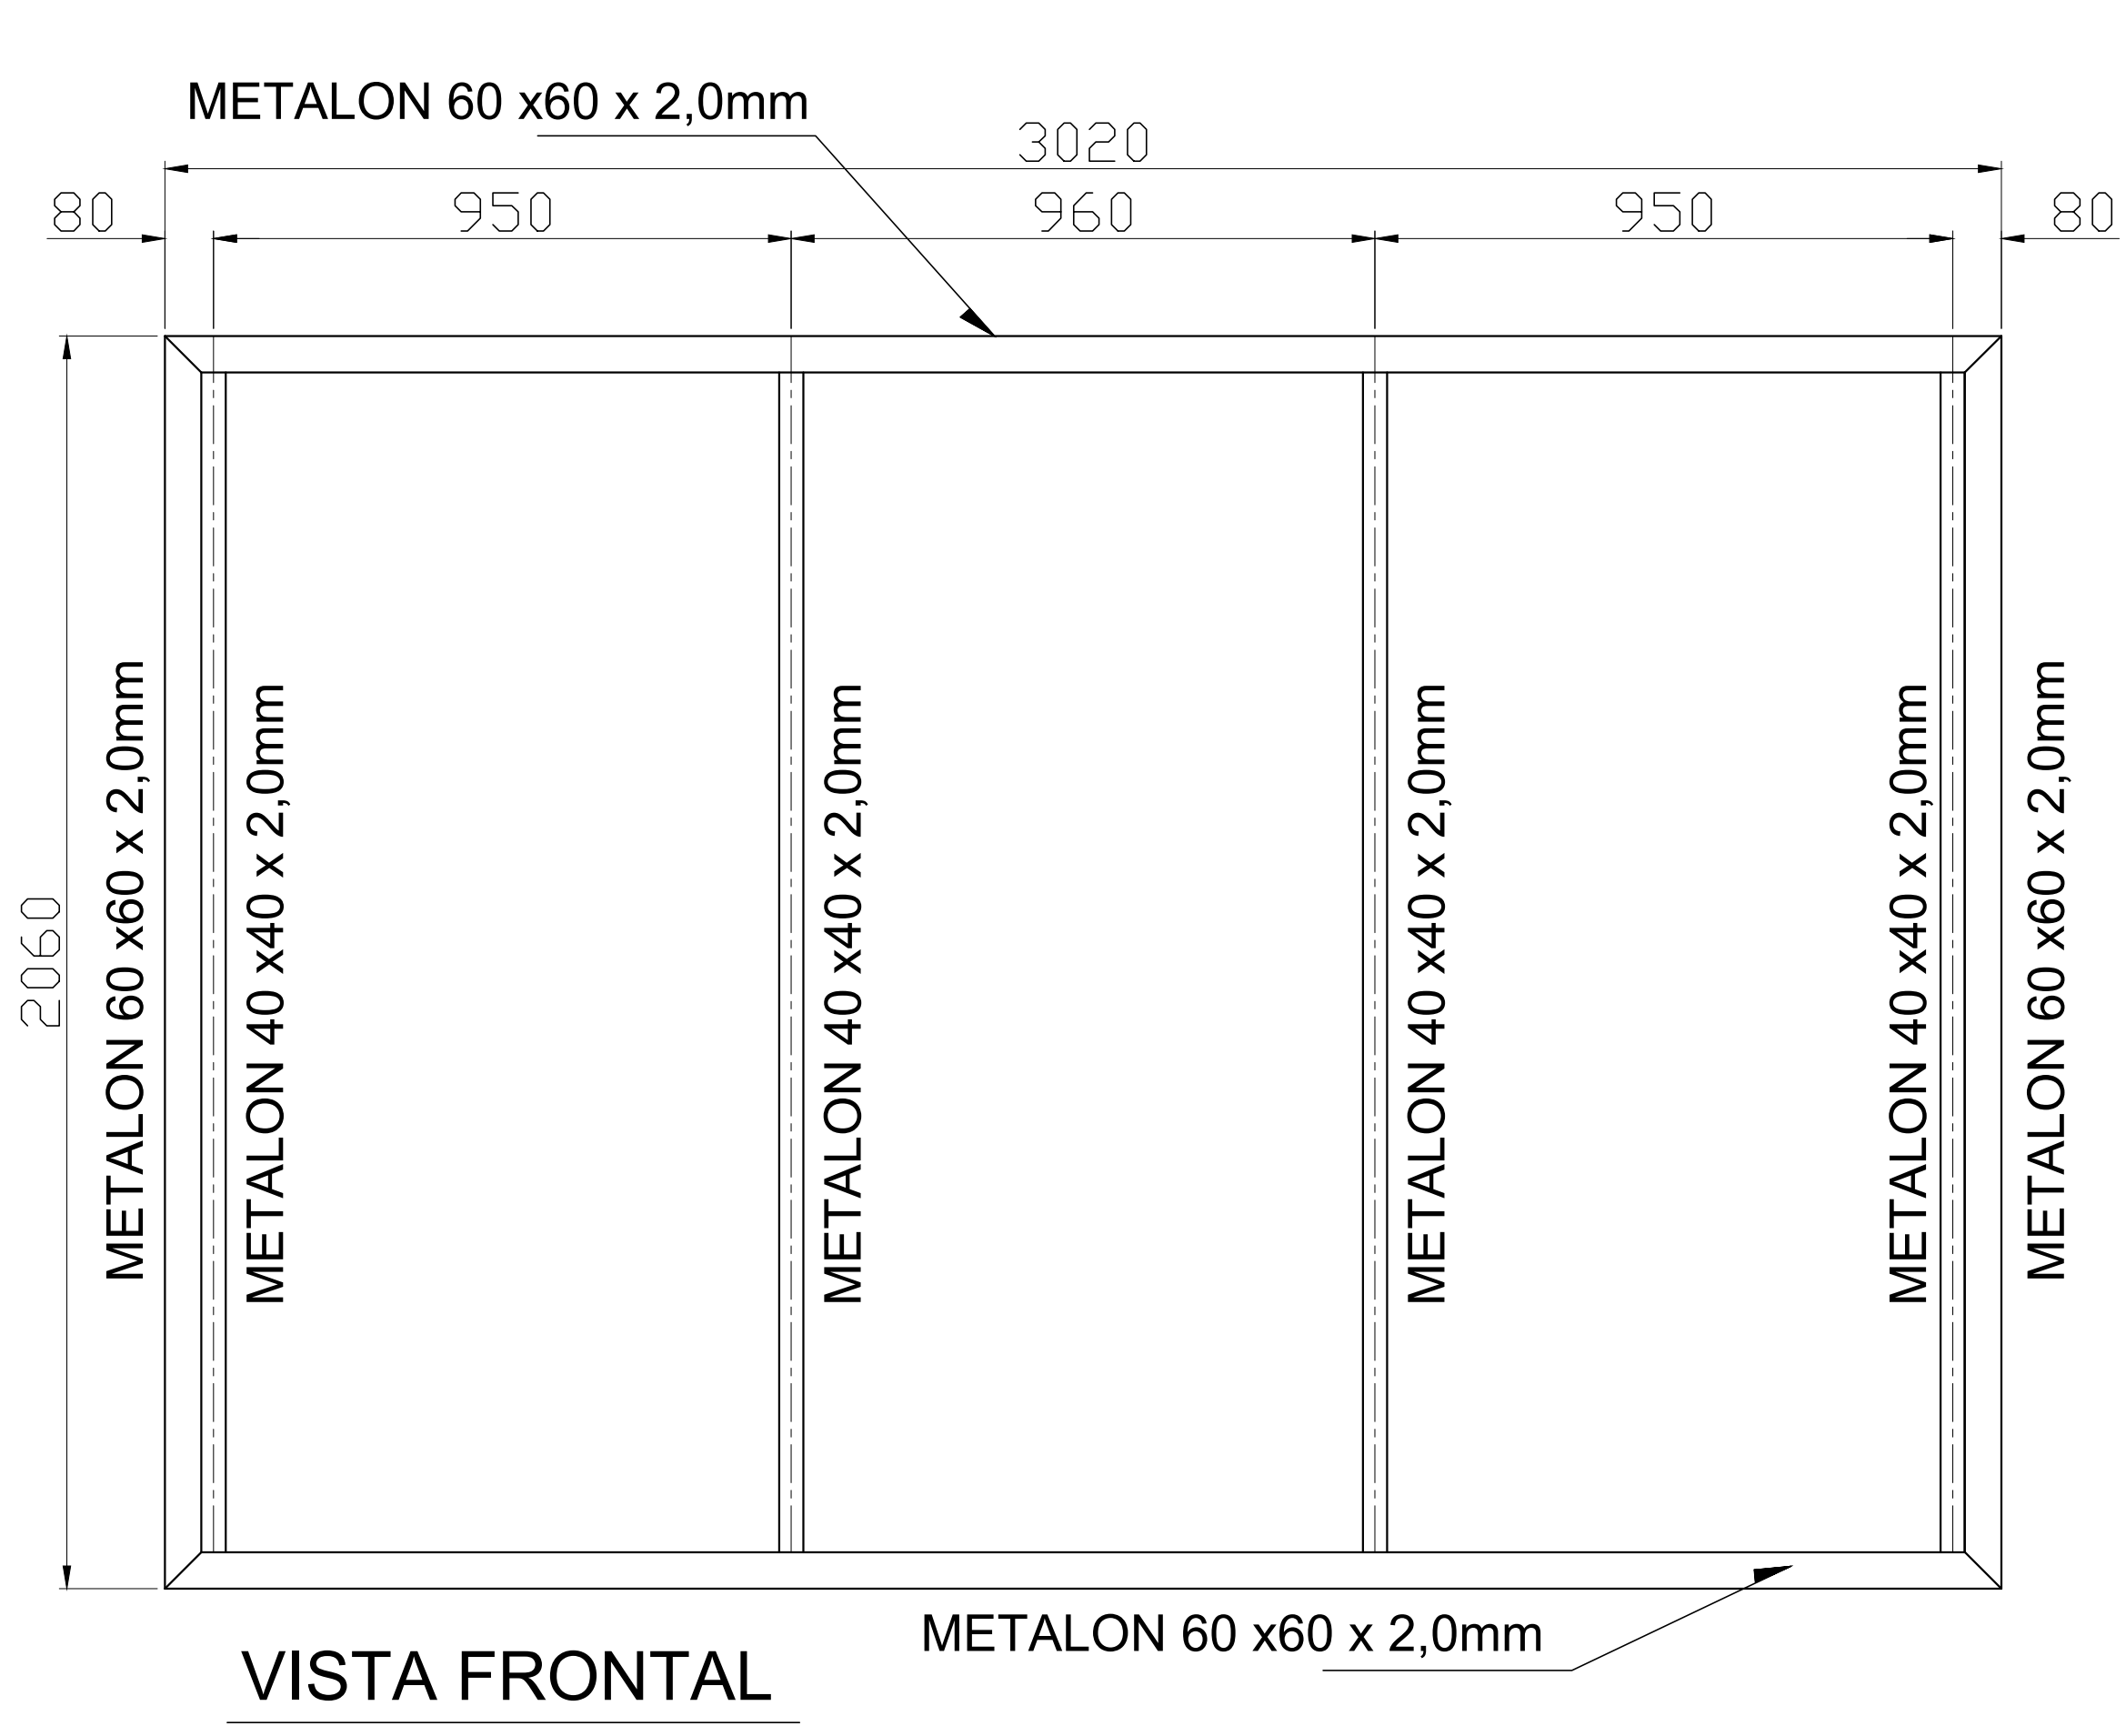


VISTA FRONTAL

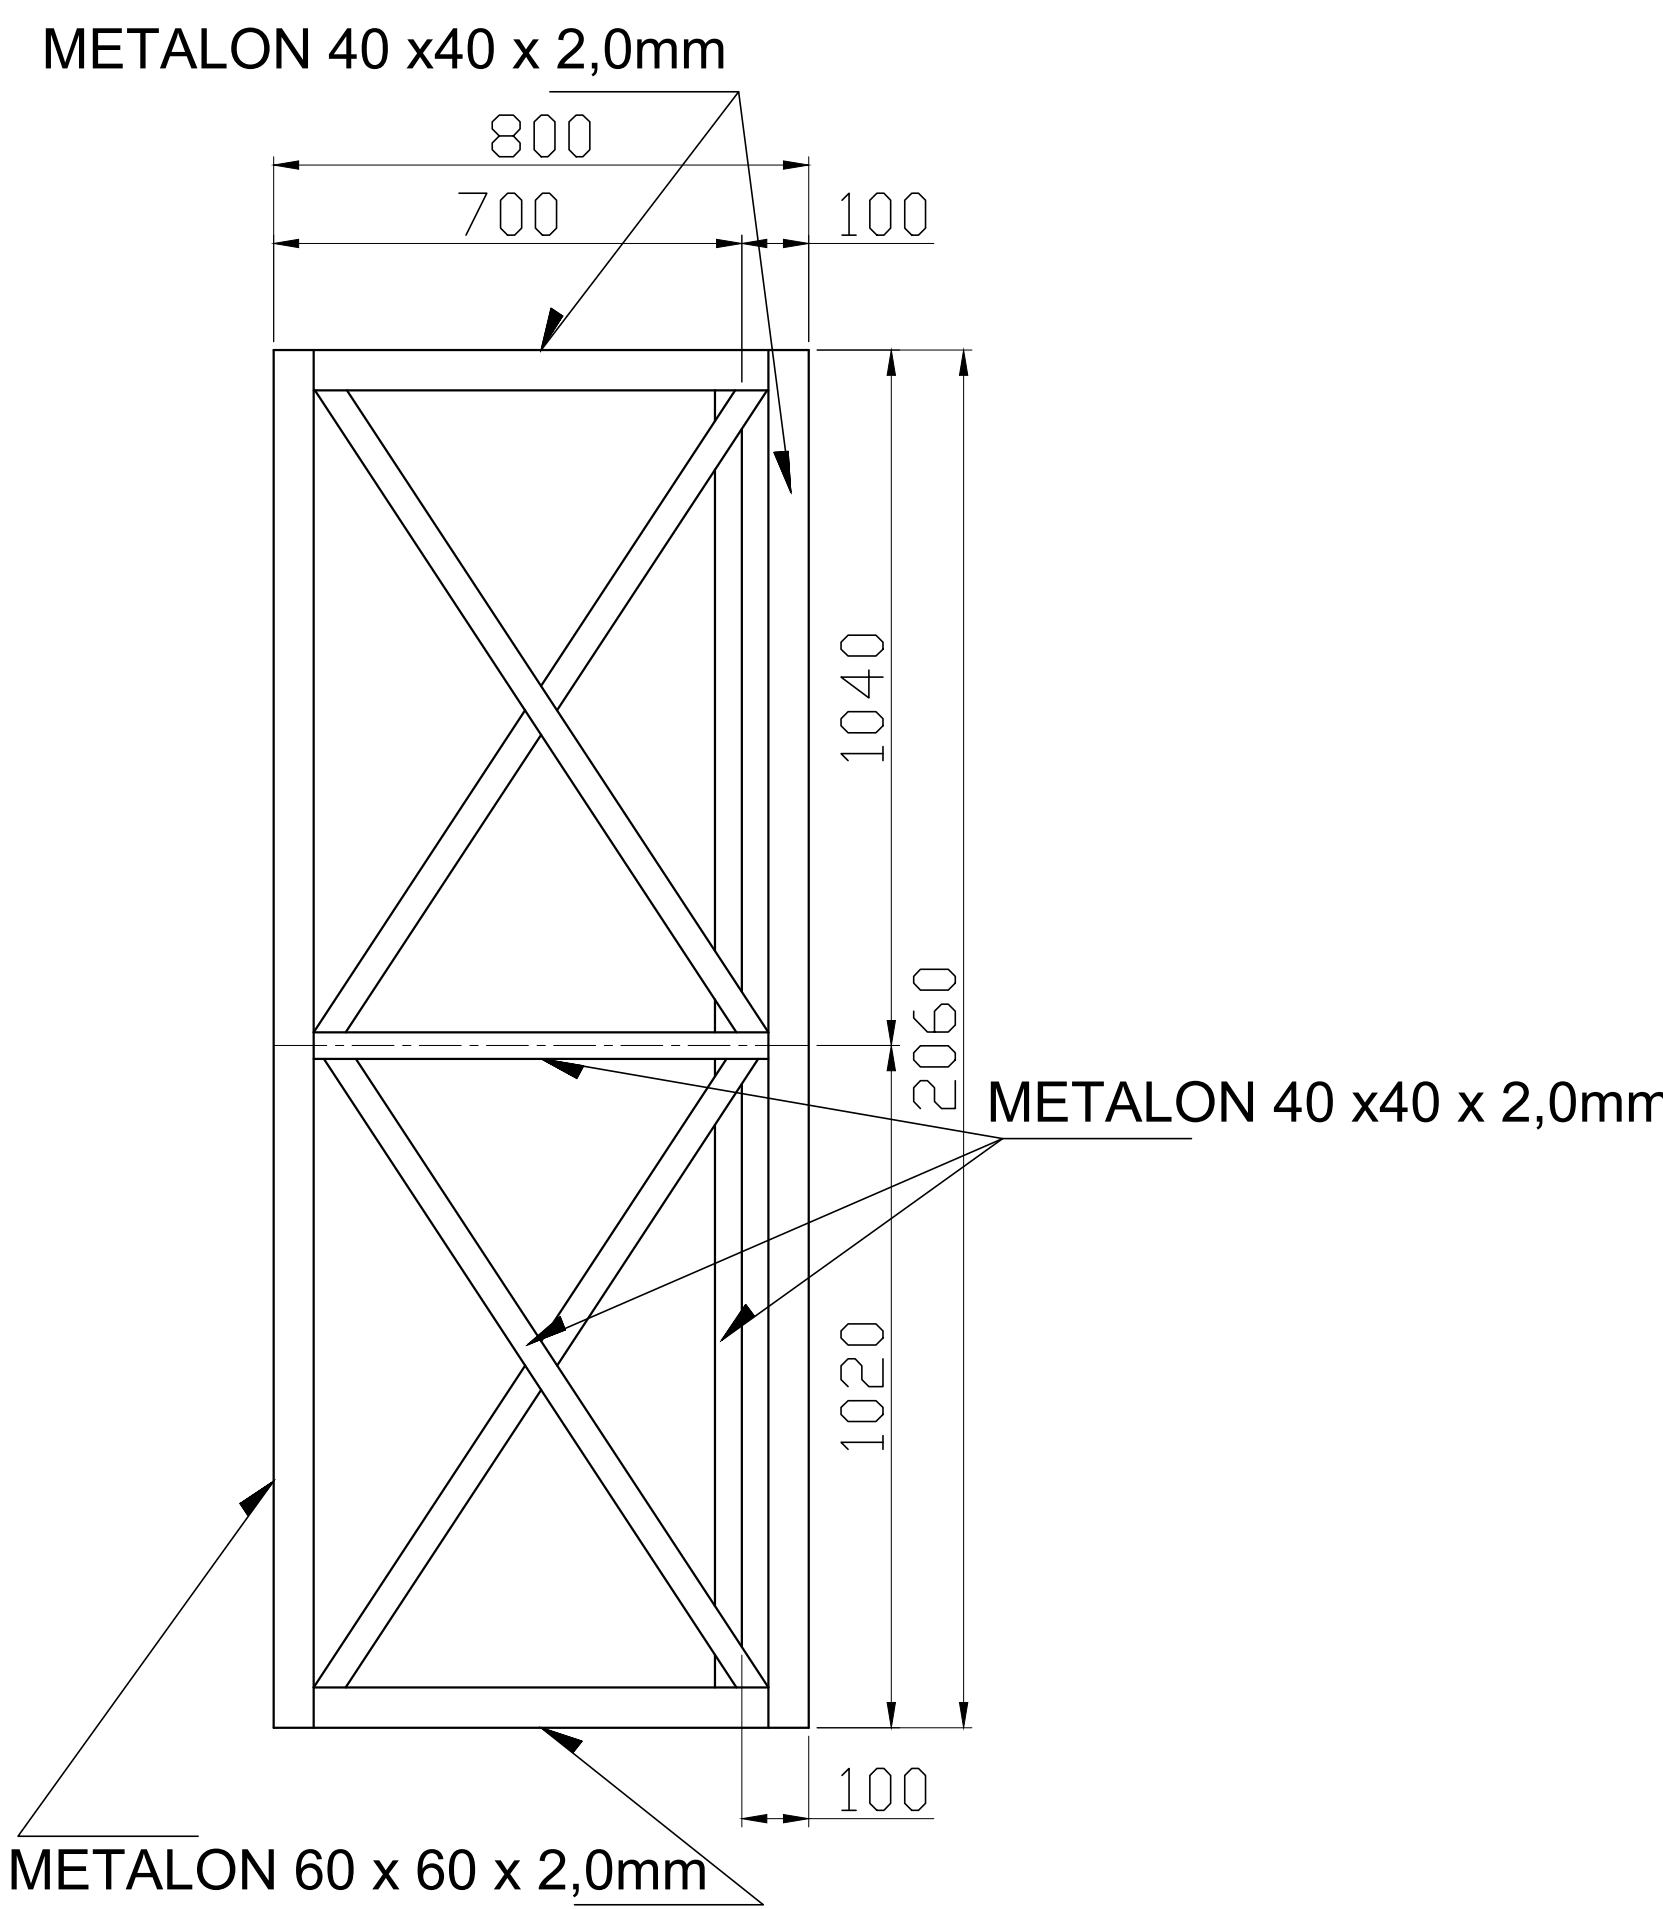


VISTA LATERAL

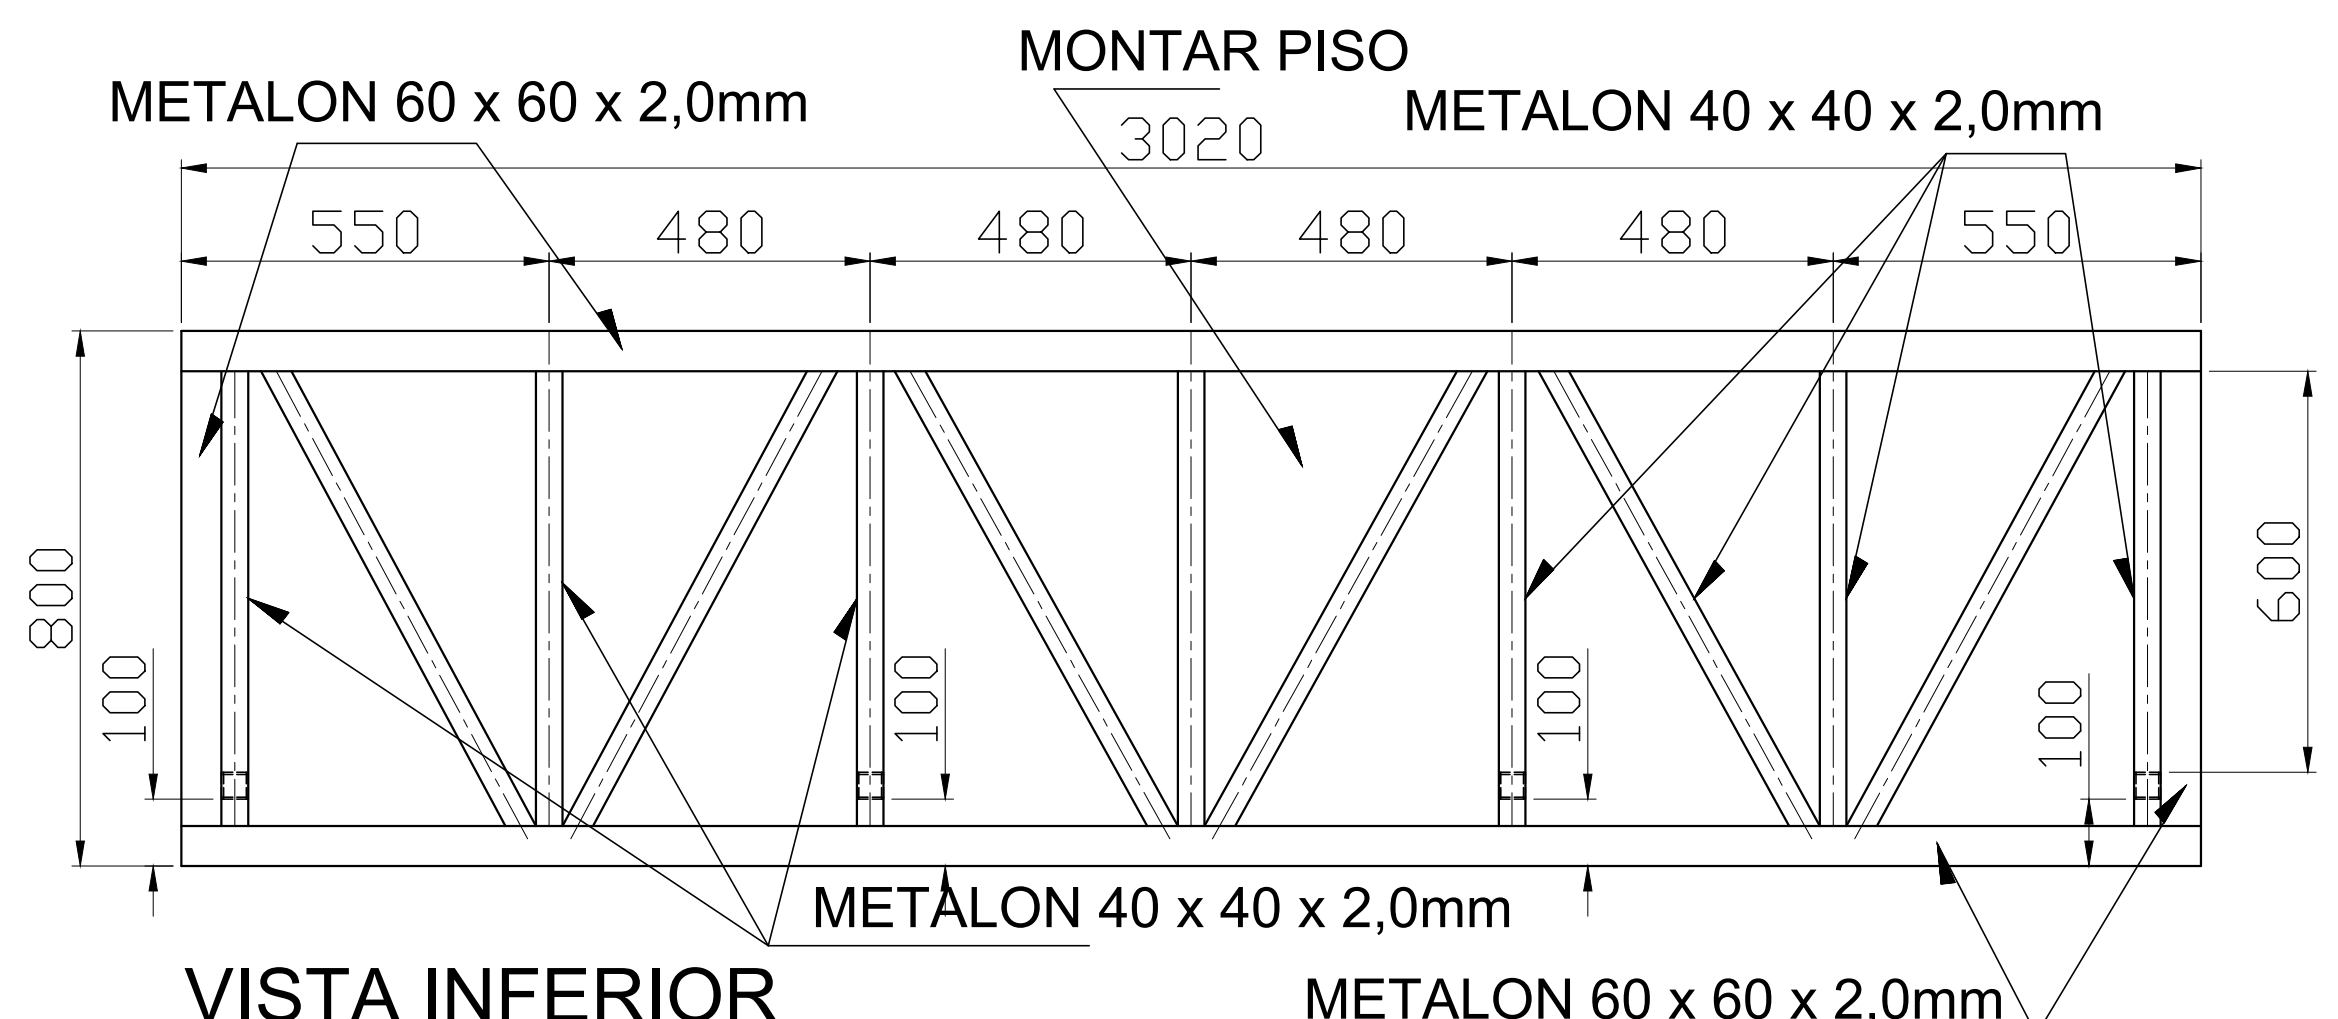




VISTA INFERIOR

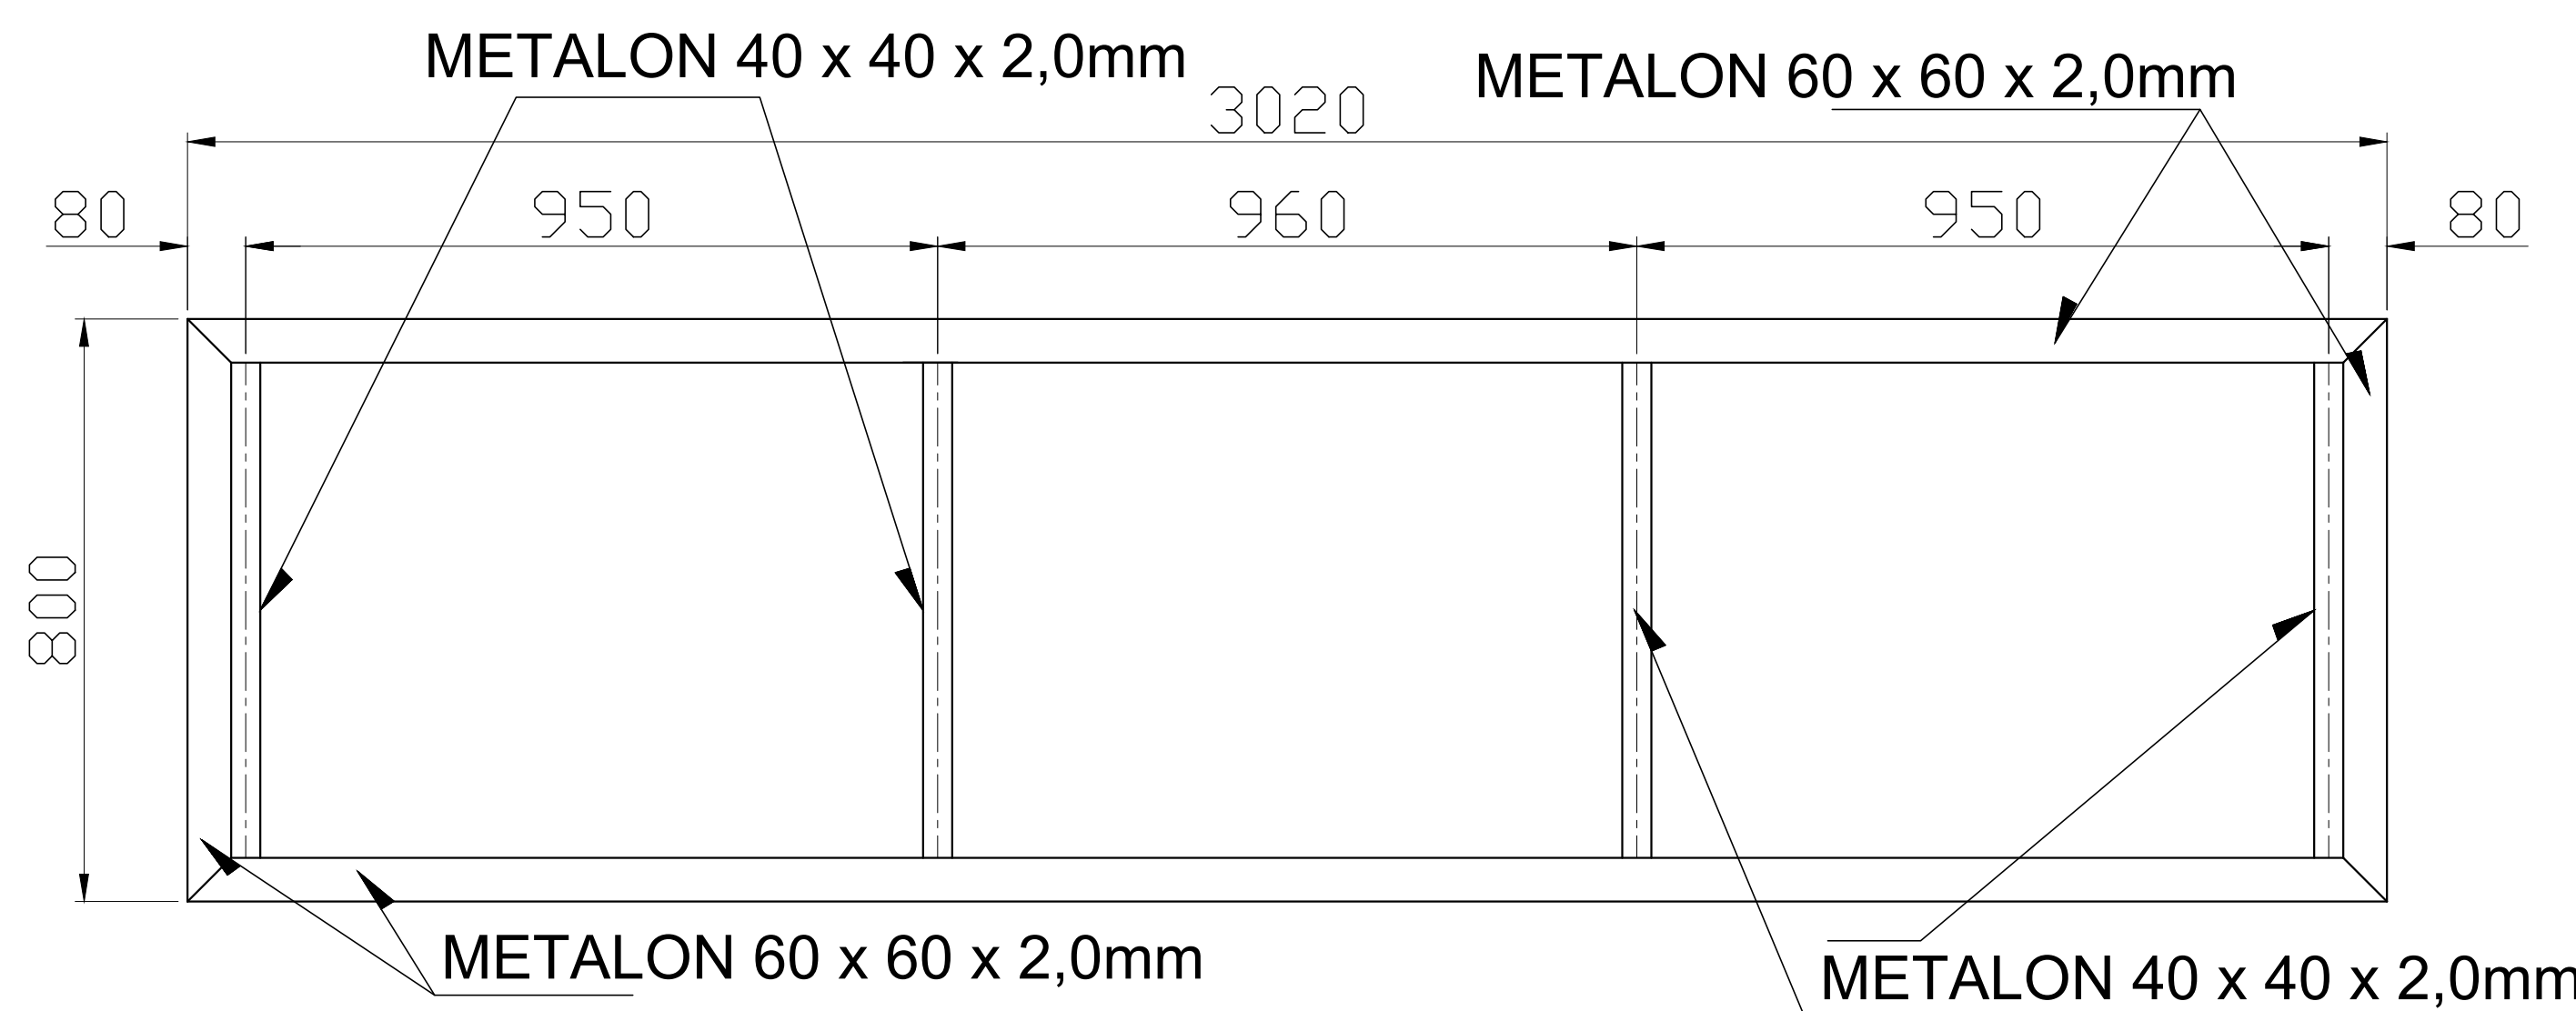

VISTA SUPERIOR

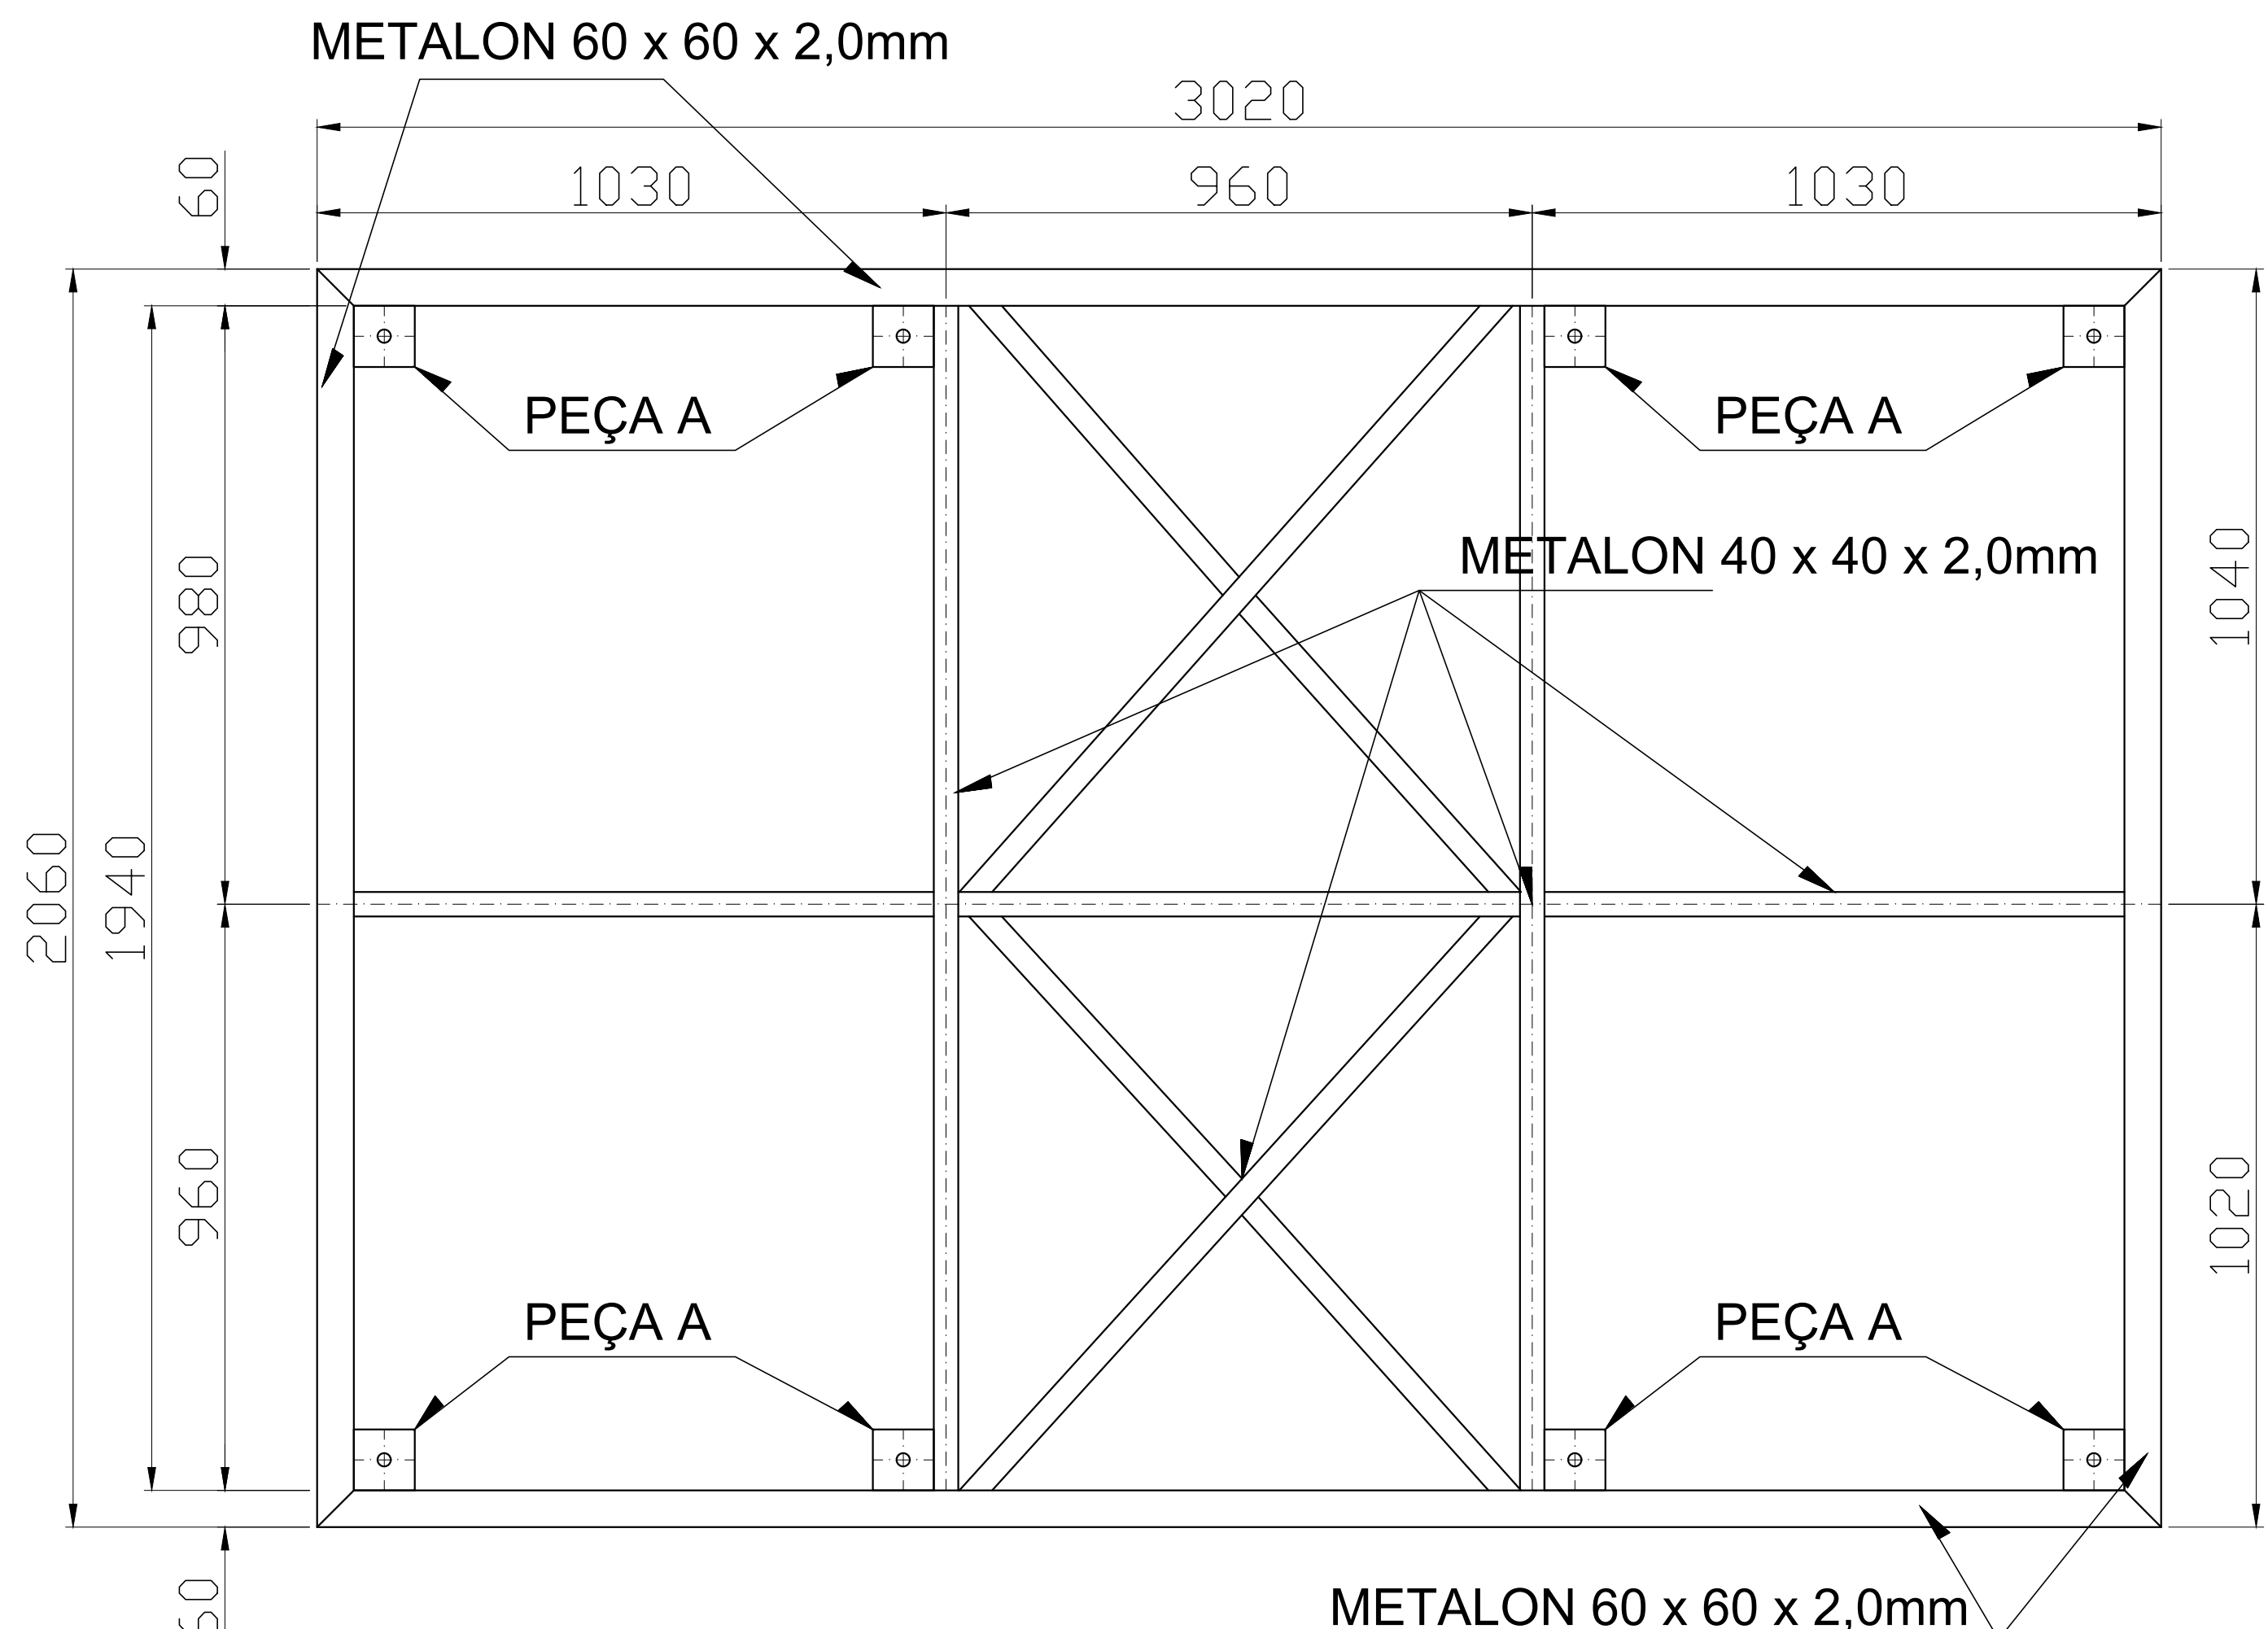

VISTA DO FUNDO

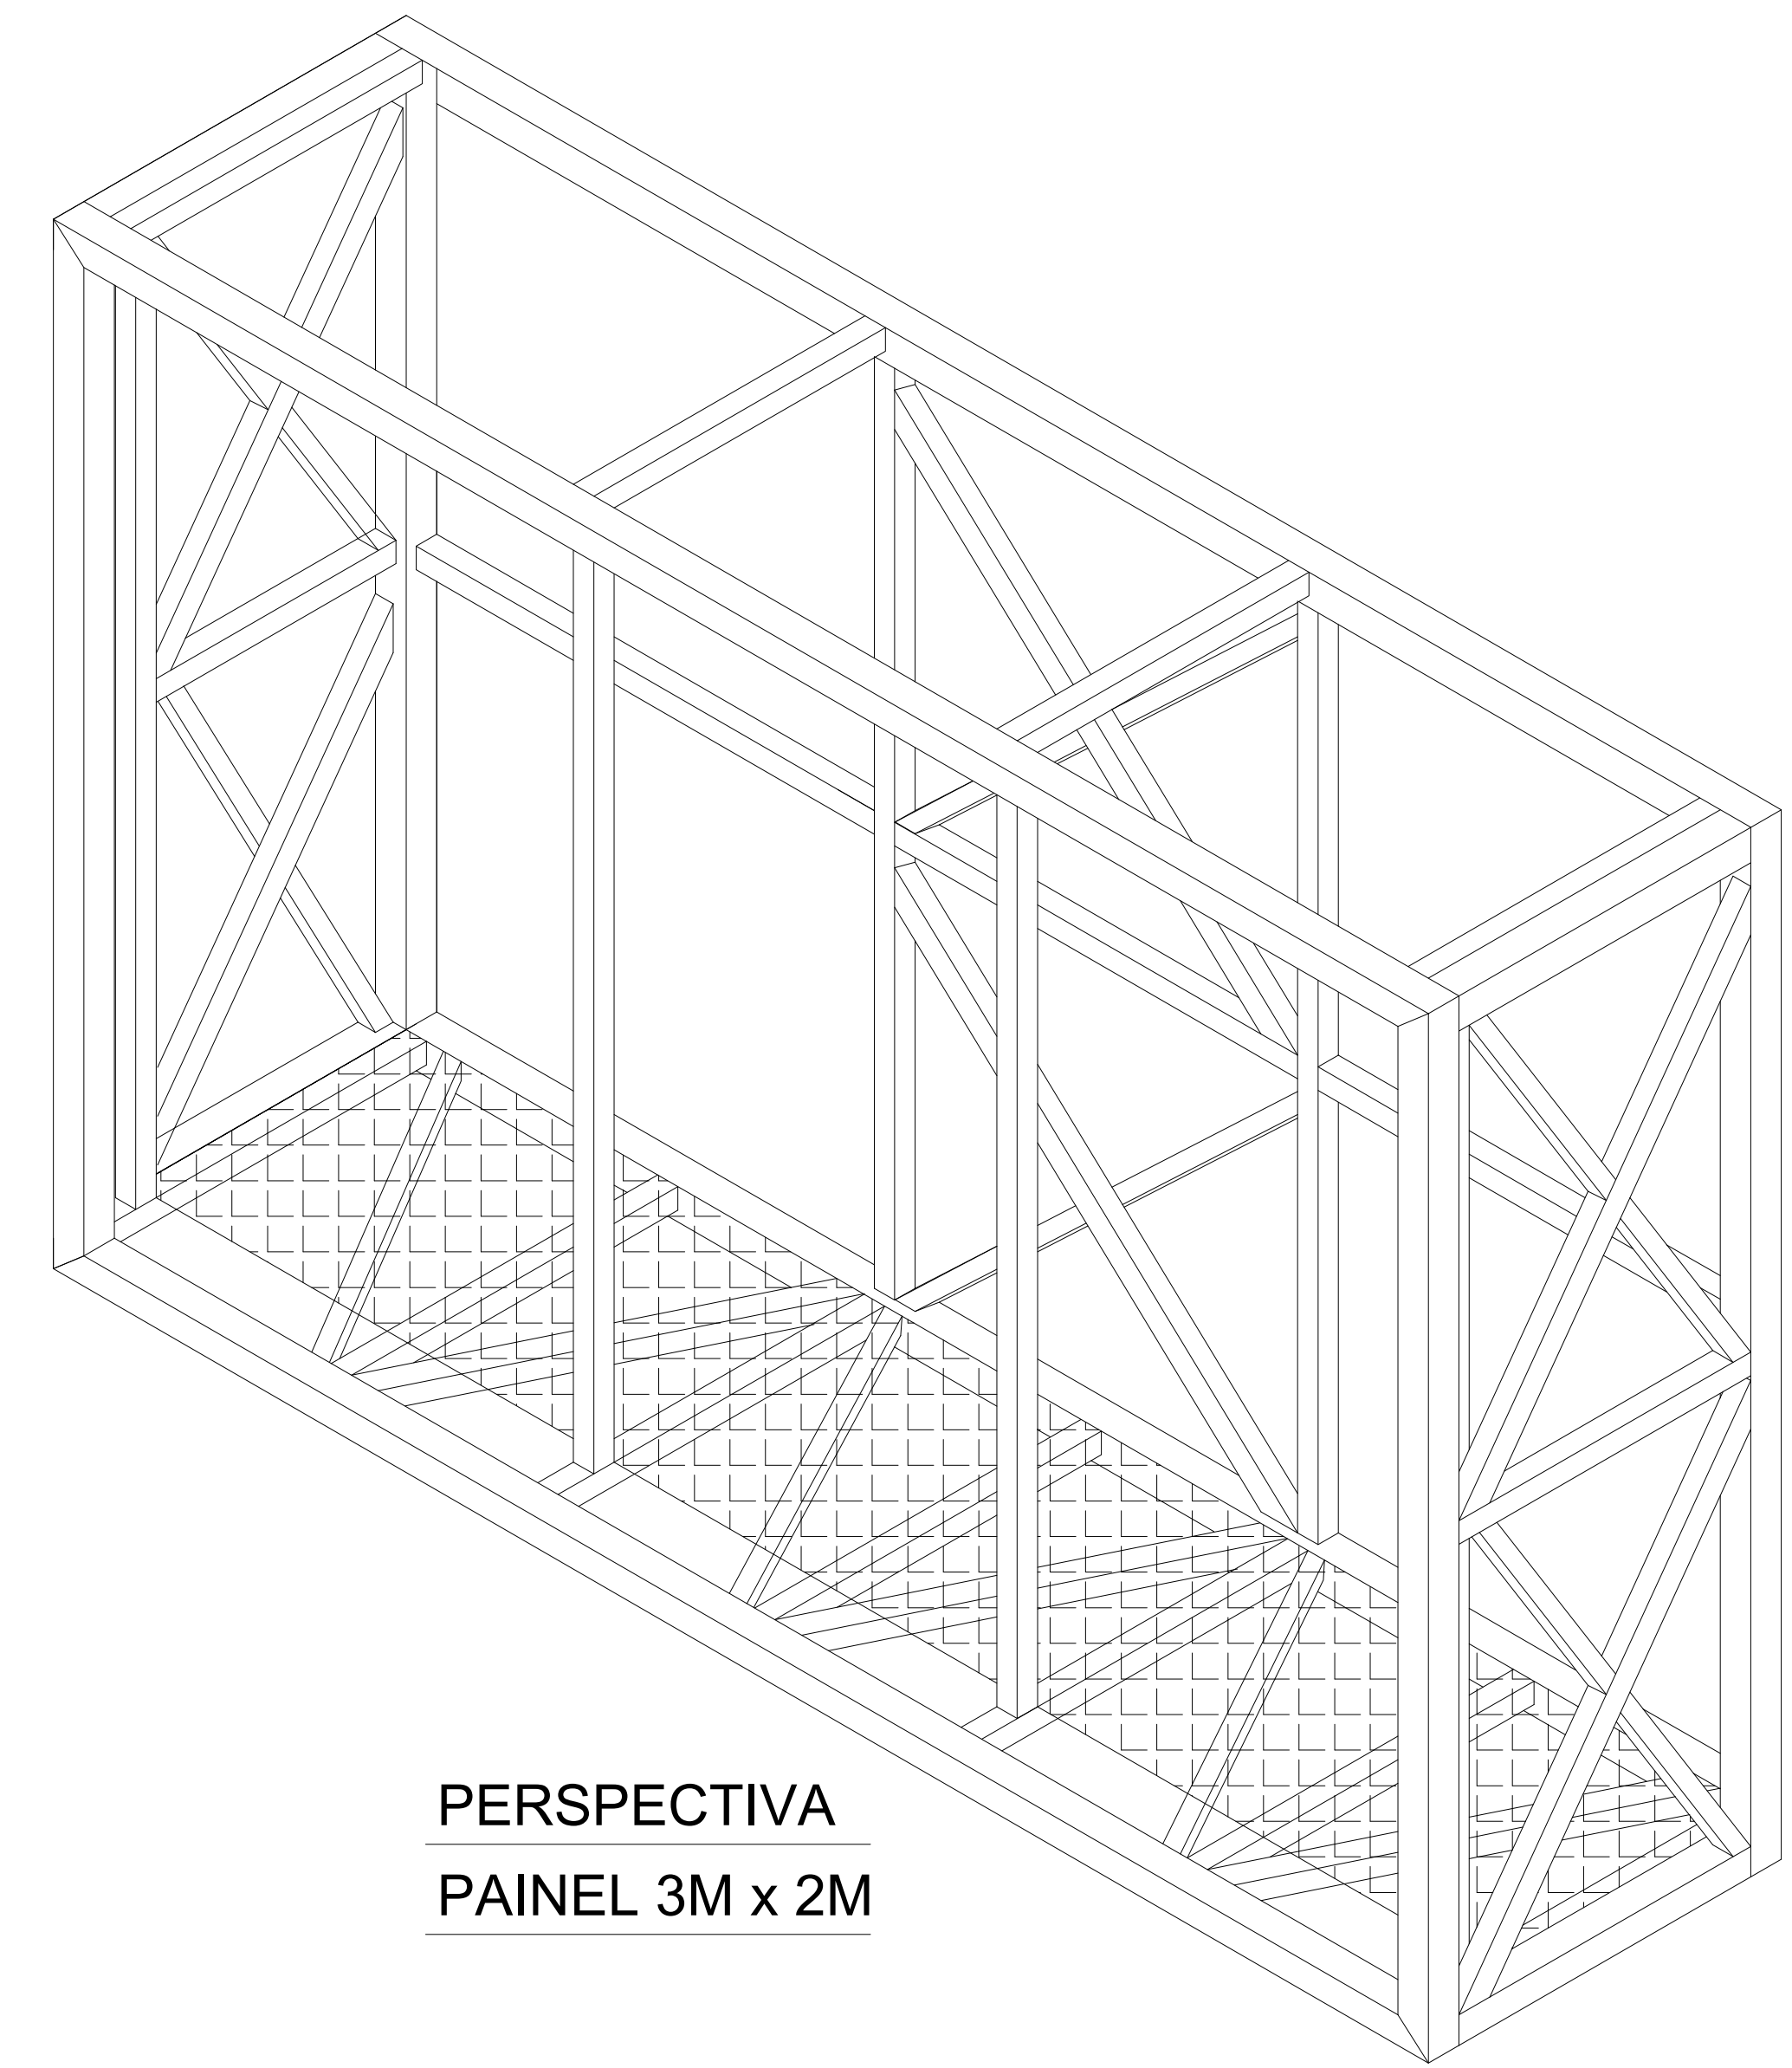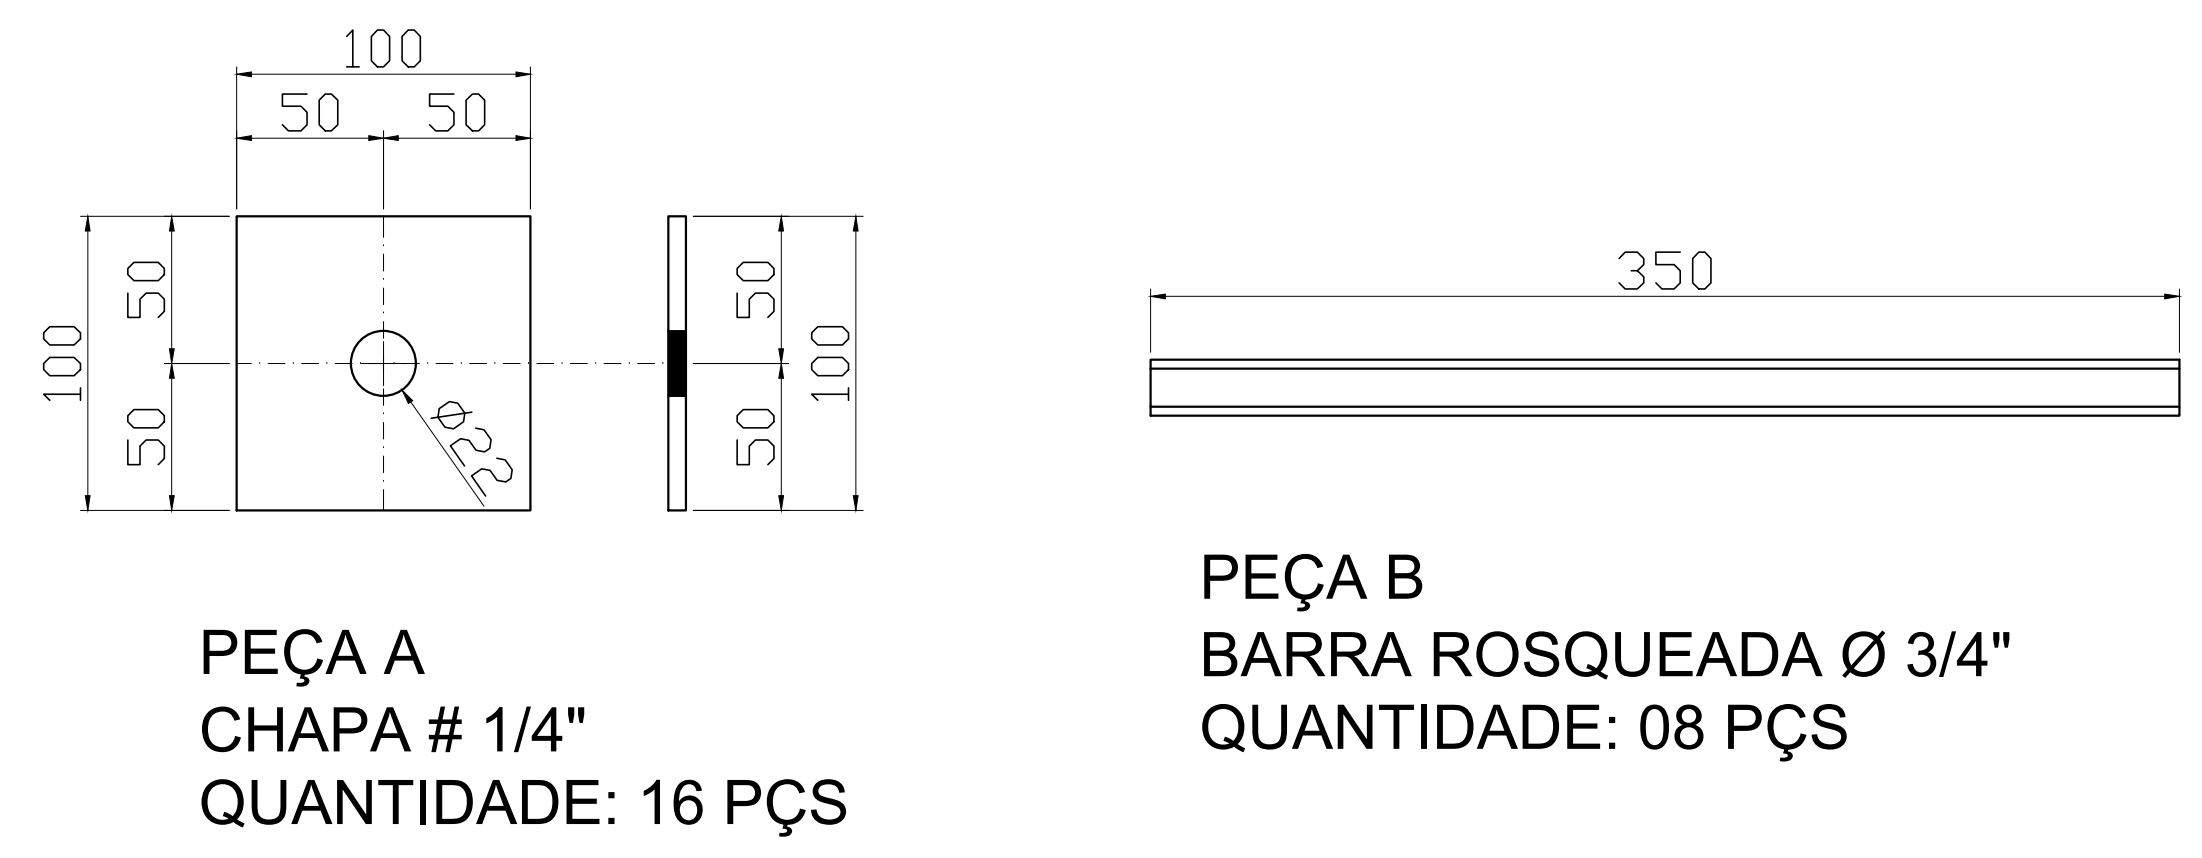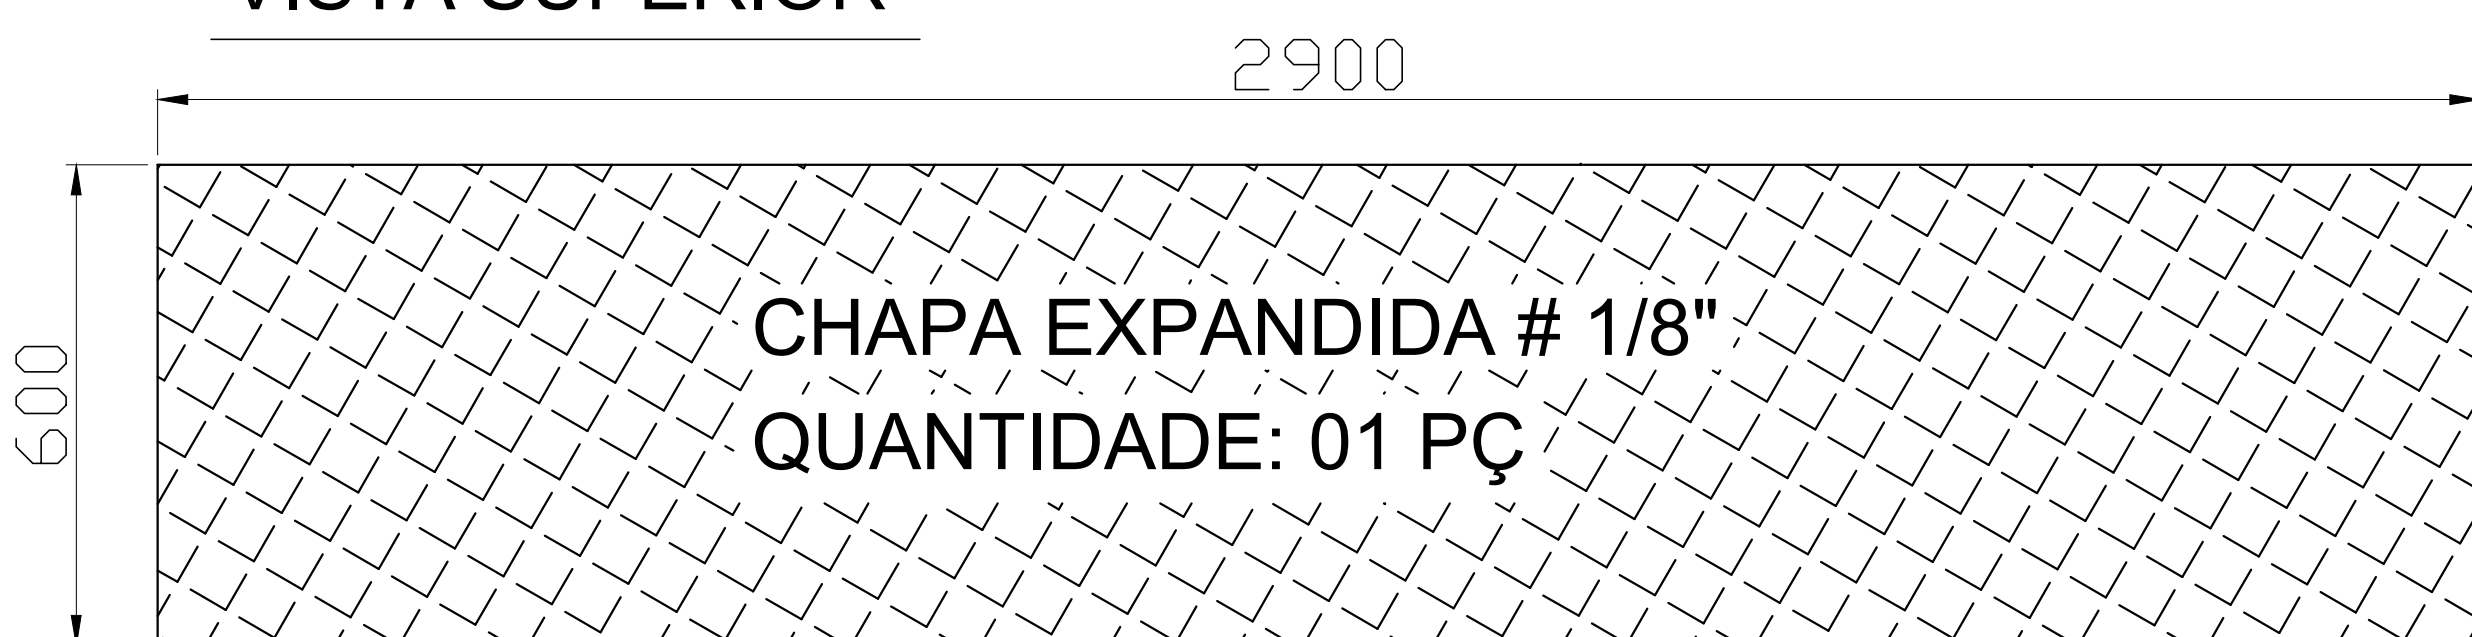

PERSPECTIVA
PAINEL 3M x 2M

LISTA DE MATERIAIS						
POS.	ESTRUTURA METÁLICA	DESCRİÇÃO	COMPR.	UNID.	QUANT.	PESO UNIT. PESO TOTAL.
01	METALON 60x60x2,0mm		6000mm	PÇS	04	3,66 KG/M 87,84 KG
02	METALON 40x40x2,0mm		6000mm	PÇS	09	2,41 KG/M 130,14 KG
03	CHAPA EXPANDIDA # 1/8" x 600mm		2900mm	PÇS	01	4,2 KG/M2 7,30 KG
04	CHAPA # 1/4" x 100mm (PEÇA A)		100mm	PÇS	16	49,39 KG/M2 7,90 KG
05	BARRA ROSQUEADA Ø 3/4" (PEÇA B)		350mm	PÇS	08	2,24 KG/M 3,92 KG
PESO TOTAL GERAL :						225,28 KG

NOTAS: MEDIDAS EM MILIMETRO;

4				
3				
2				
1				
0	INICIAL	J.W.F		13/08/24
N°	DESCRİÇÃO	DES.	RESP.	DATA

LED EXPERT

PROJETO SOMENTE PARA ORÇAMENTO
NAO UTILIZAR PARA FABRICAÇÃO

OBRA PAINEL 3 x 2 OUTDOOR			Data: 13-08-2024	Projeto: JANILSON	
CONTÉM: PROJETO DE ESTRUTURA METÁLICA					
ESCALA IND.	SE --	R.T.: --	Nº LED EXPERT: 70-2024-08		FORMATO: REVISÃO A2 00