
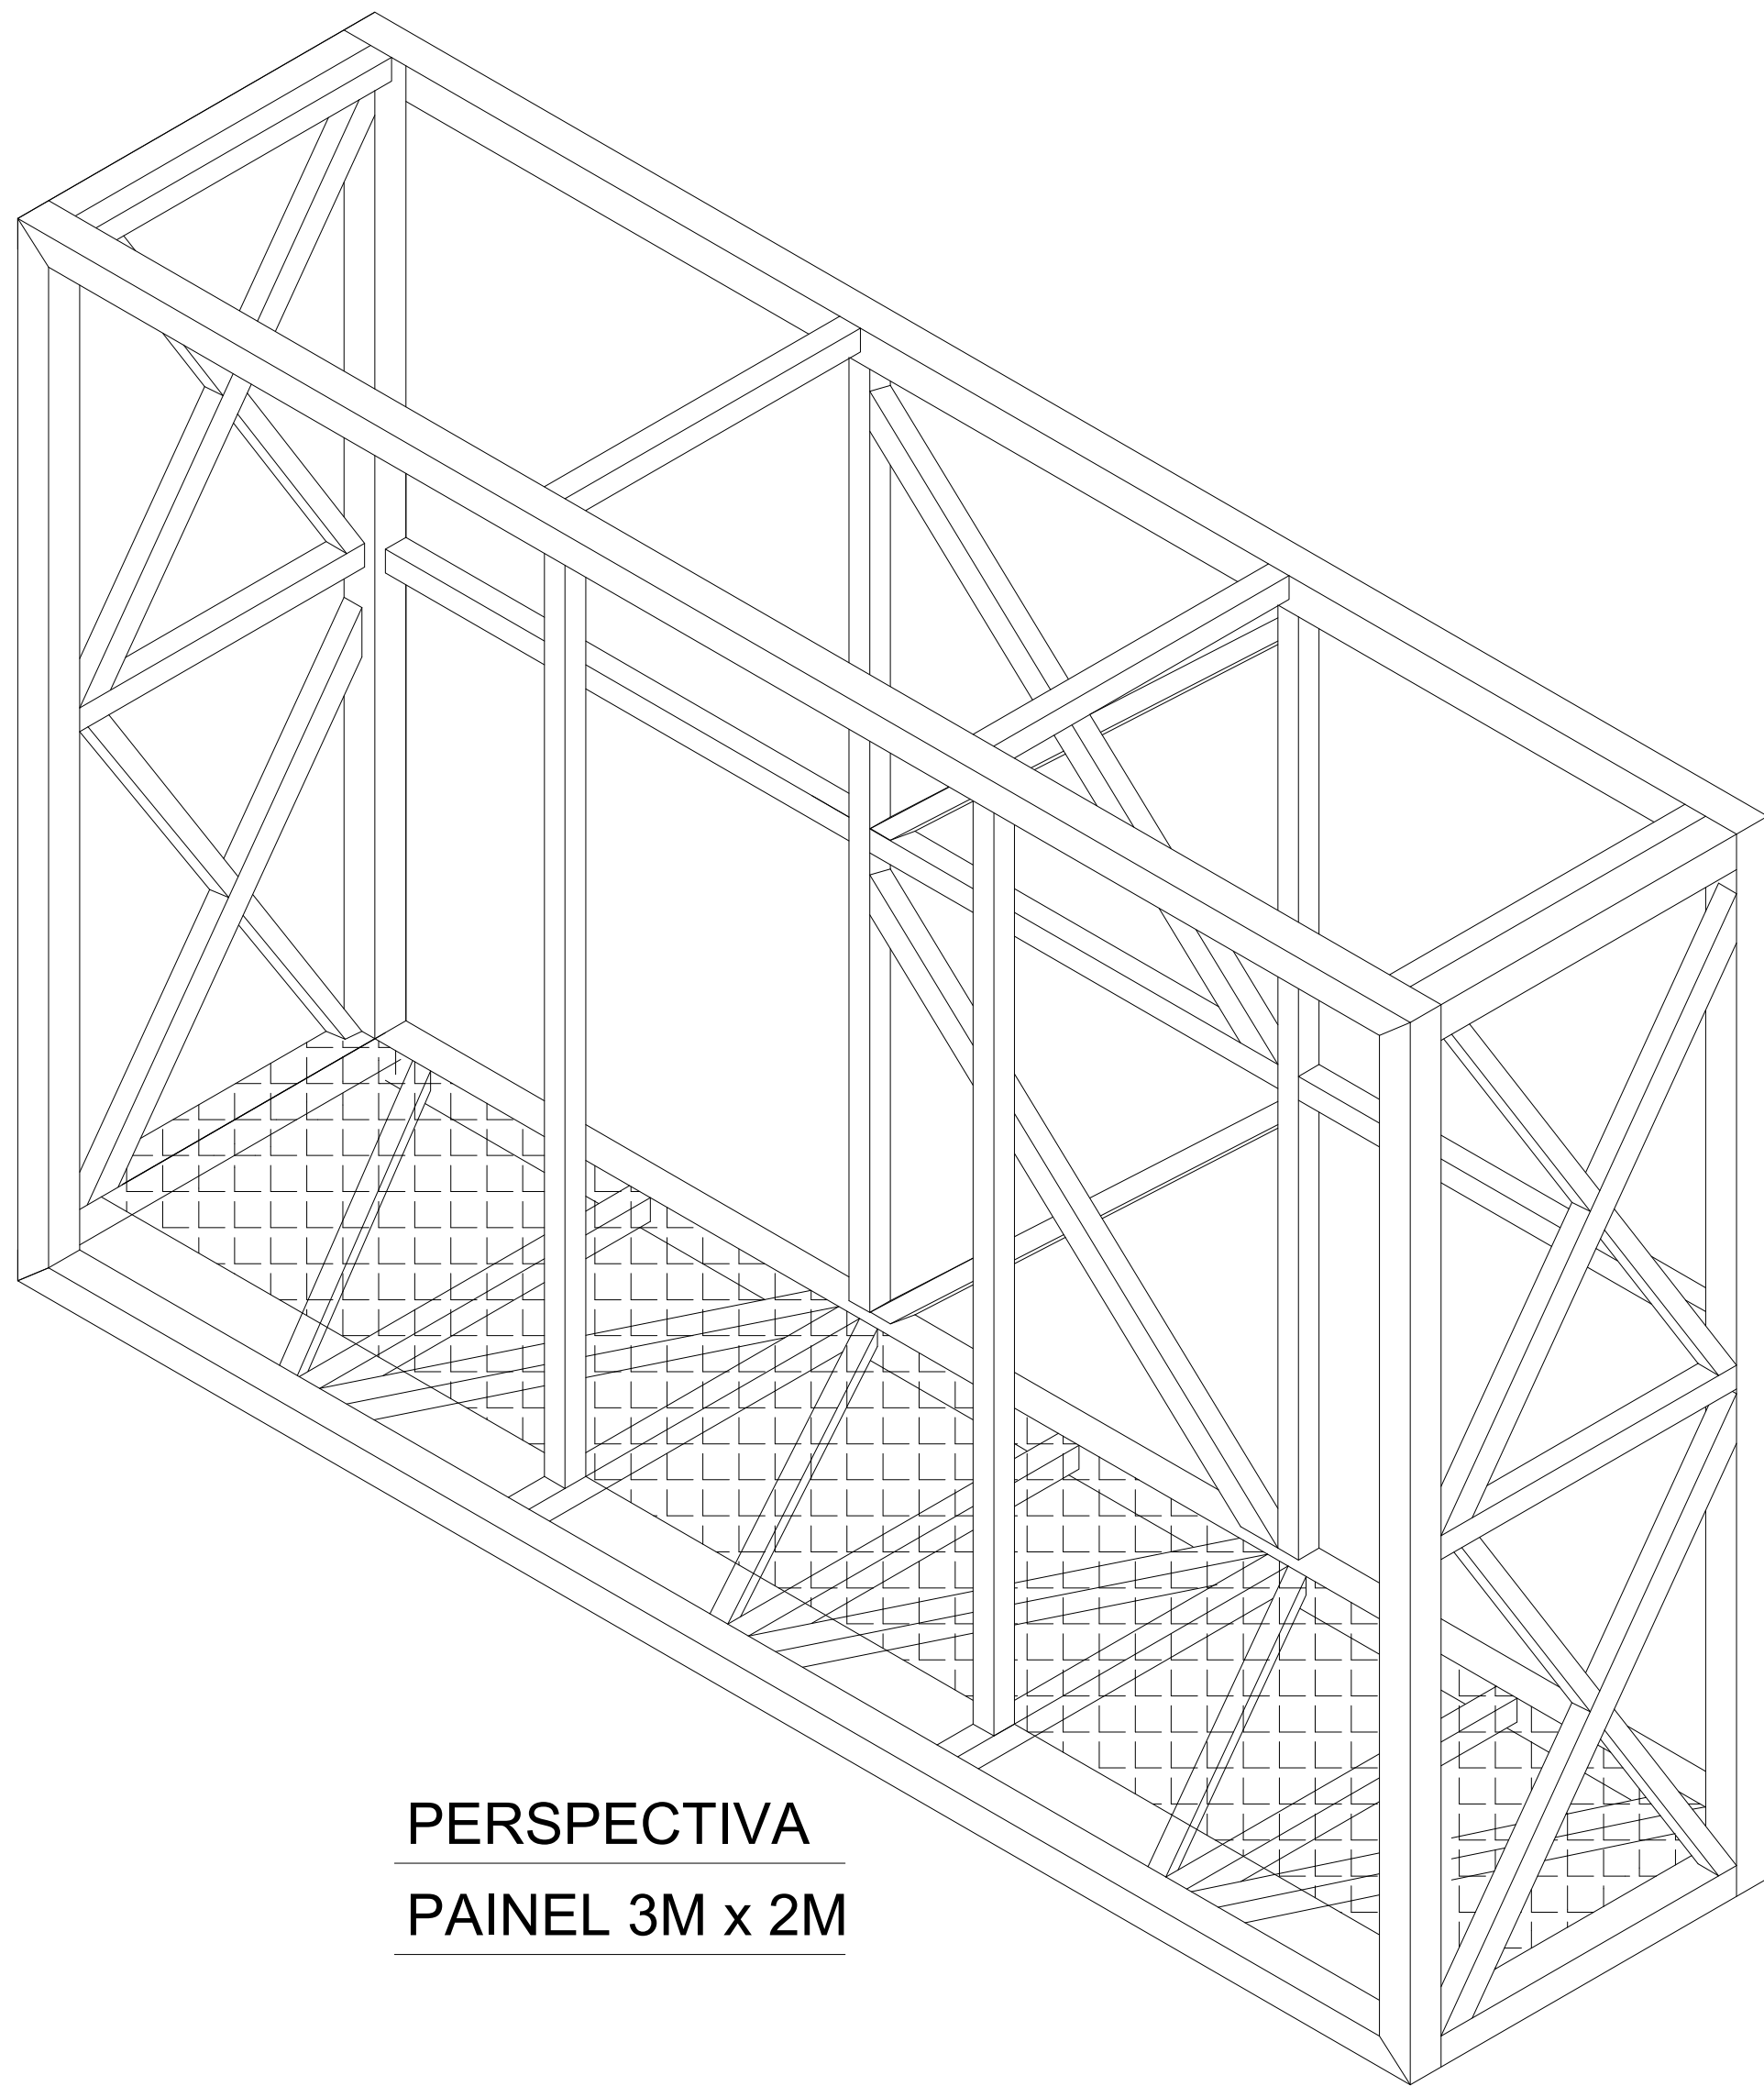
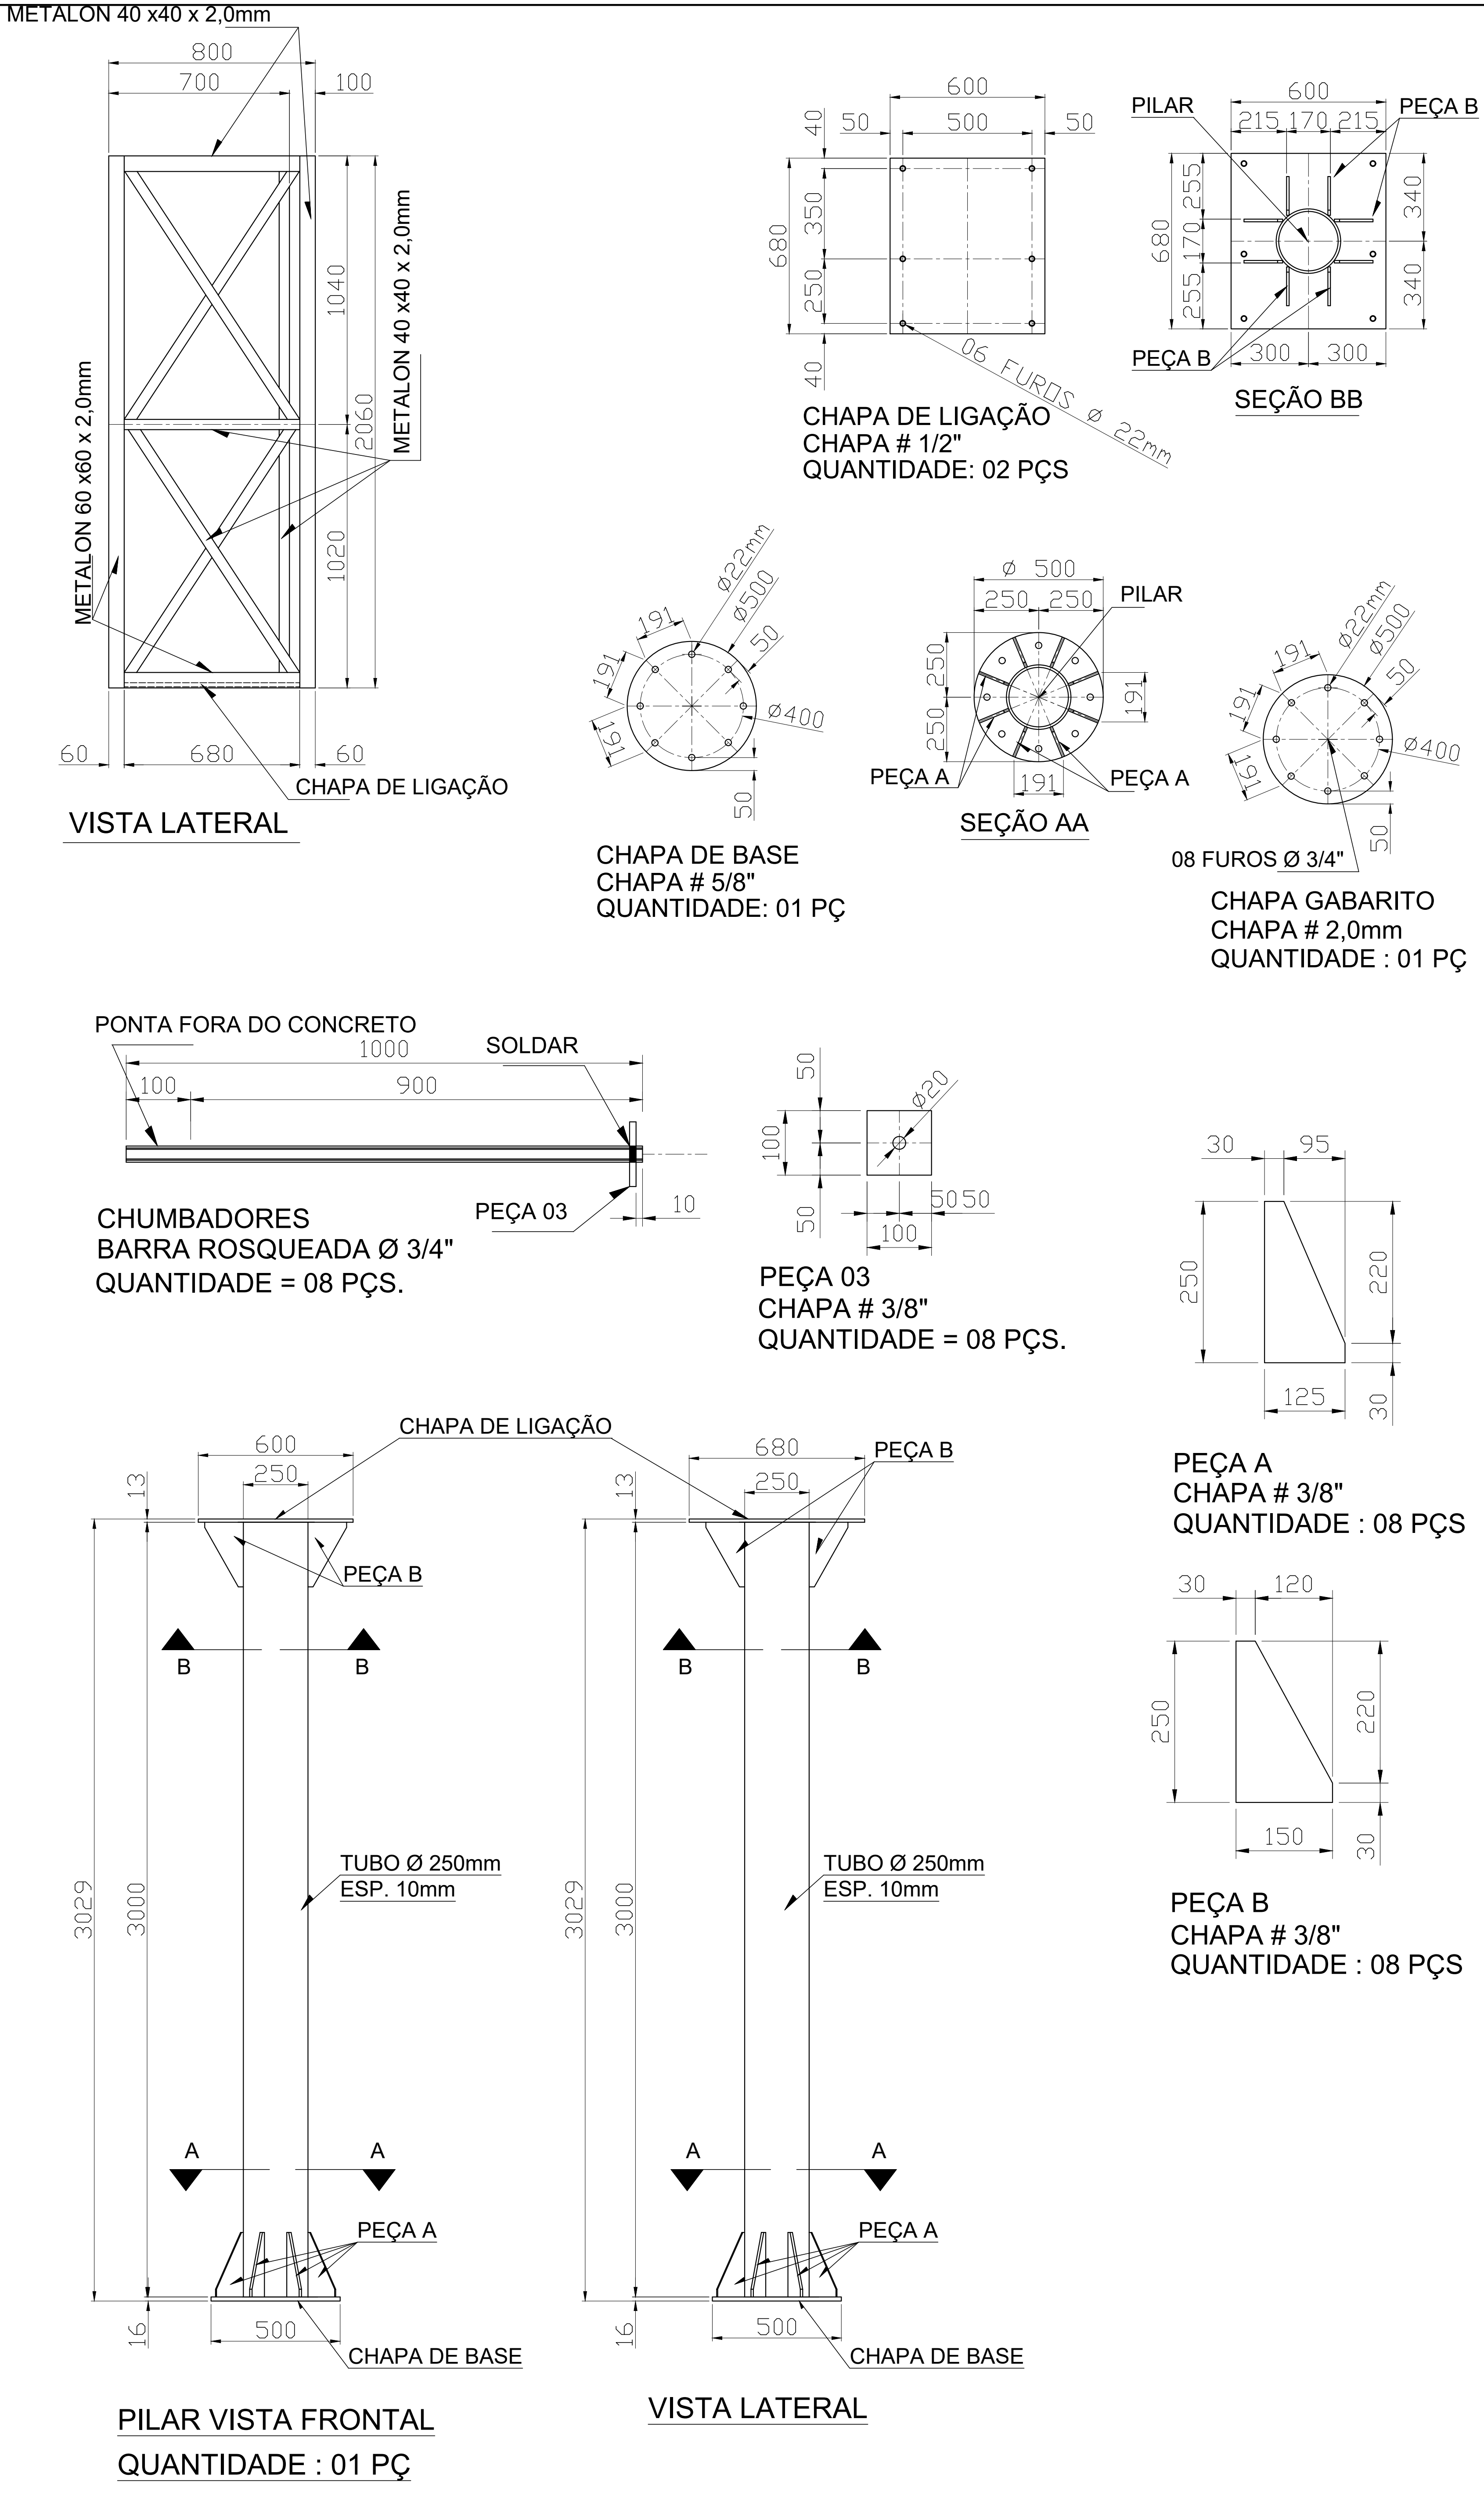


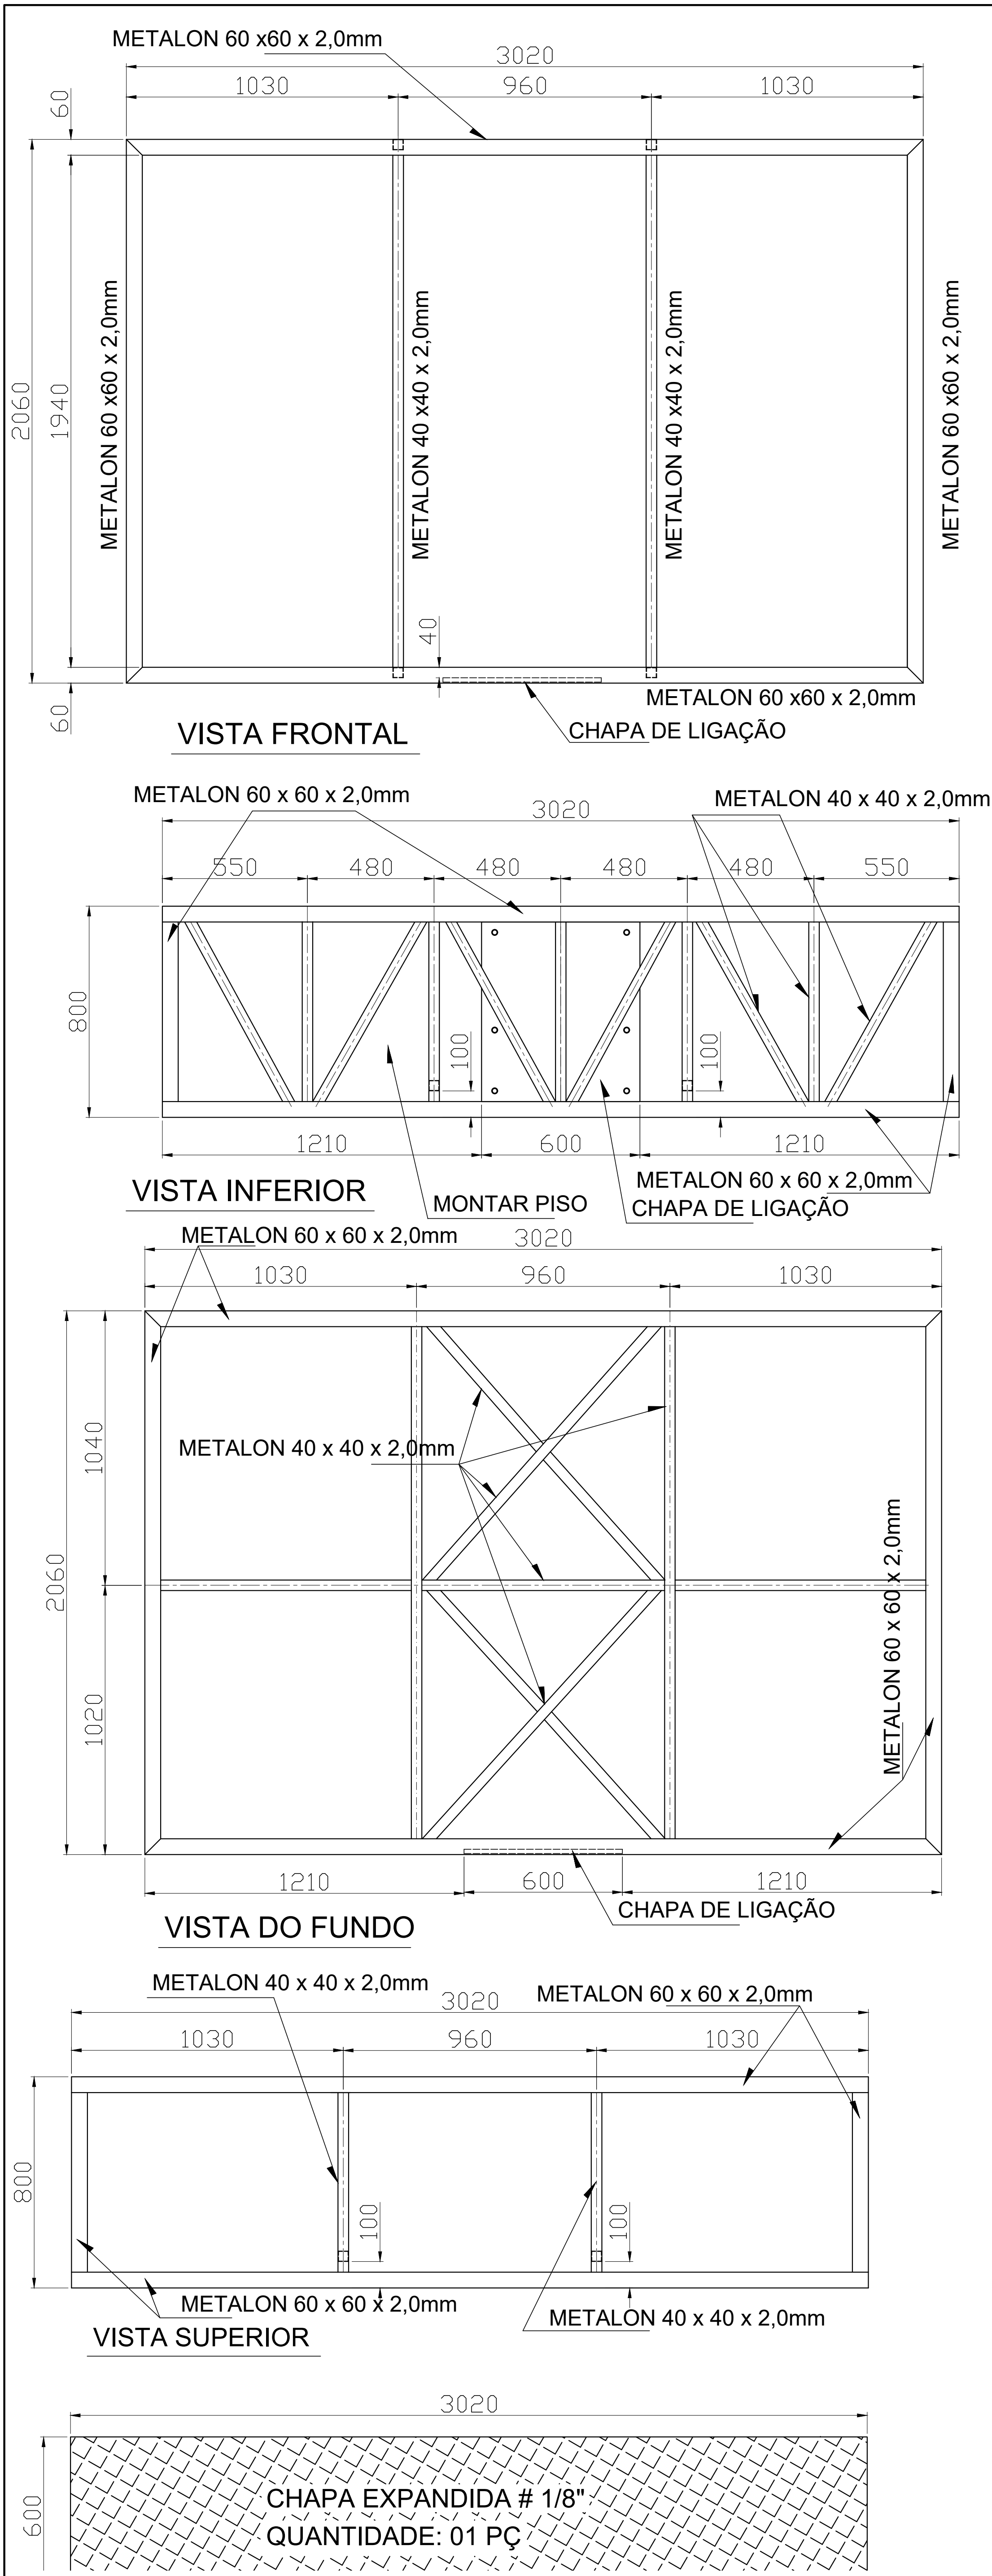

PERSPECTIVA  
PAINEL 3M x 2M

| LISTA DE MATERIAIS                                             |                                       |                  |       |                  |                       |
|----------------------------------------------------------------|---------------------------------------|------------------|-------|------------------|-----------------------|
| Cliente: HUMBERTO MADUREIRA                                    |                                       |                  |       | DATA: 15/08/2023 |                       |
| Obra: PAINEL 3x2 GB RENTAL OUTDOOR      PILAR 3,0 METROS       |                                       |                  |       |                  |                       |
|                                                                | ESTRUTURA METÁLICA                    |                  |       |                  |                       |
| POS.                                                           | DESCRIÇÃO                             | COMPR.           | UNID. | QUANT.           | PESO UNIT. PESO TOTAL |
| 01                                                             | METALON 60x60x2,0mm                   | 6000mm           | PÇS   | 04               | 3,61 KG/M 87,00 KG    |
| 02                                                             | METALON 40x40x2,0mm                   | 6000mm           | PÇS   | 07               | 2,41 KG 101,22 KG     |
| 03                                                             | CHAPA EXPANDIDA # 1/8" x 600mm        | 3020mm           | PÇS   | 01               | 4,2 KG/M2 7,61 KG     |
| 04                                                             | TUBO ø 250mm PAREDE ESP. 10mm (PILAR) | 3000mm           | PÇS   | 01               | 58,46 KG/M 175,40 KG  |
| 05                                                             | CHAPA # 5/8" x ø 500mm (BASE)         | ø 500mm          | PÇ    | 01               | 125,44 KG/M2 24,61 KG |
| 06                                                             | CHAPA # 3/8" x 600mm (LIGAÇÃO)        | 680mm            | PÇS   | 02               | 74,50 KG/M2 60,79 KG  |
| 07                                                             | CHAPA # 3/8" x 125mm (PEÇA A)         | 250mm            | PÇS   | 08               | 74,50 KG/M2 9,31 KG   |
| 08                                                             | CHAPA # 3/8" x 150mm (PEÇA B)         | 250mm            | PÇS   | 08               | 74,50 KG/M2 11,17 KG  |
| 09                                                             | CHAPA # 14 x ø 500mm (GABARITO)       | ø 500mm          | PÇ    | 01               | 16,00 KG/M2 3,14 KG   |
| 10                                                             | FERRO REDONDO ø 3/4" (CHUMBADOR)      | 1000mm           | PÇS   | 08               | 2,24 KG/M 17,92 KG    |
| 11                                                             | CHAPA # 3/8" x 100mm (PEÇA 03)        | 100mm            | PÇS   | 08               | 74,48 KG/M2 5,95 KG   |
| PESO TOTAL GERAL :                                             |                                       |                  |       |                  | 504,12 KG             |
| NOTAS: MEDIDAS EM MILIMETRO;                                   |                                       |                  |       |                  |                       |
| 4                                                              |                                       |                  |       |                  |                       |
| 3                                                              |                                       |                  |       |                  |                       |
| 2                                                              |                                       |                  |       |                  |                       |
| 1                                                              |                                       |                  |       |                  |                       |
| 0                                                              | INICIAL                               |                  | F.G.S |                  | 15/08/23              |
| N°                                                             | DESCRIÇÃO                             |                  | DES.  | RESP.            | DATA                  |
| PROJETO SOMENTE PARA ORÇAMENTO<br>NAO UTILIZAR PARA FABRICAÇÃO |                                       |                  |       |                  |                       |
| OBRA<br>PAINEL 3 x 2 GB RENTAL OUTDOOR                         |                                       |                  | Data: |                  | Desenhista:           |
| CONTÉM:<br>PROJETO DE ESTRUTURA METÁLICA – PILAR 3 METROS      |                                       |                  |       |                  |                       |
| ESCALA                                                         | SE                                    | REGISTRO CREA.:  |       | FORMATO:         | REVISÃO               |
| IND.                                                           | --                                    | 168-2023-08-FL01 |       | A2               | 00                    |