


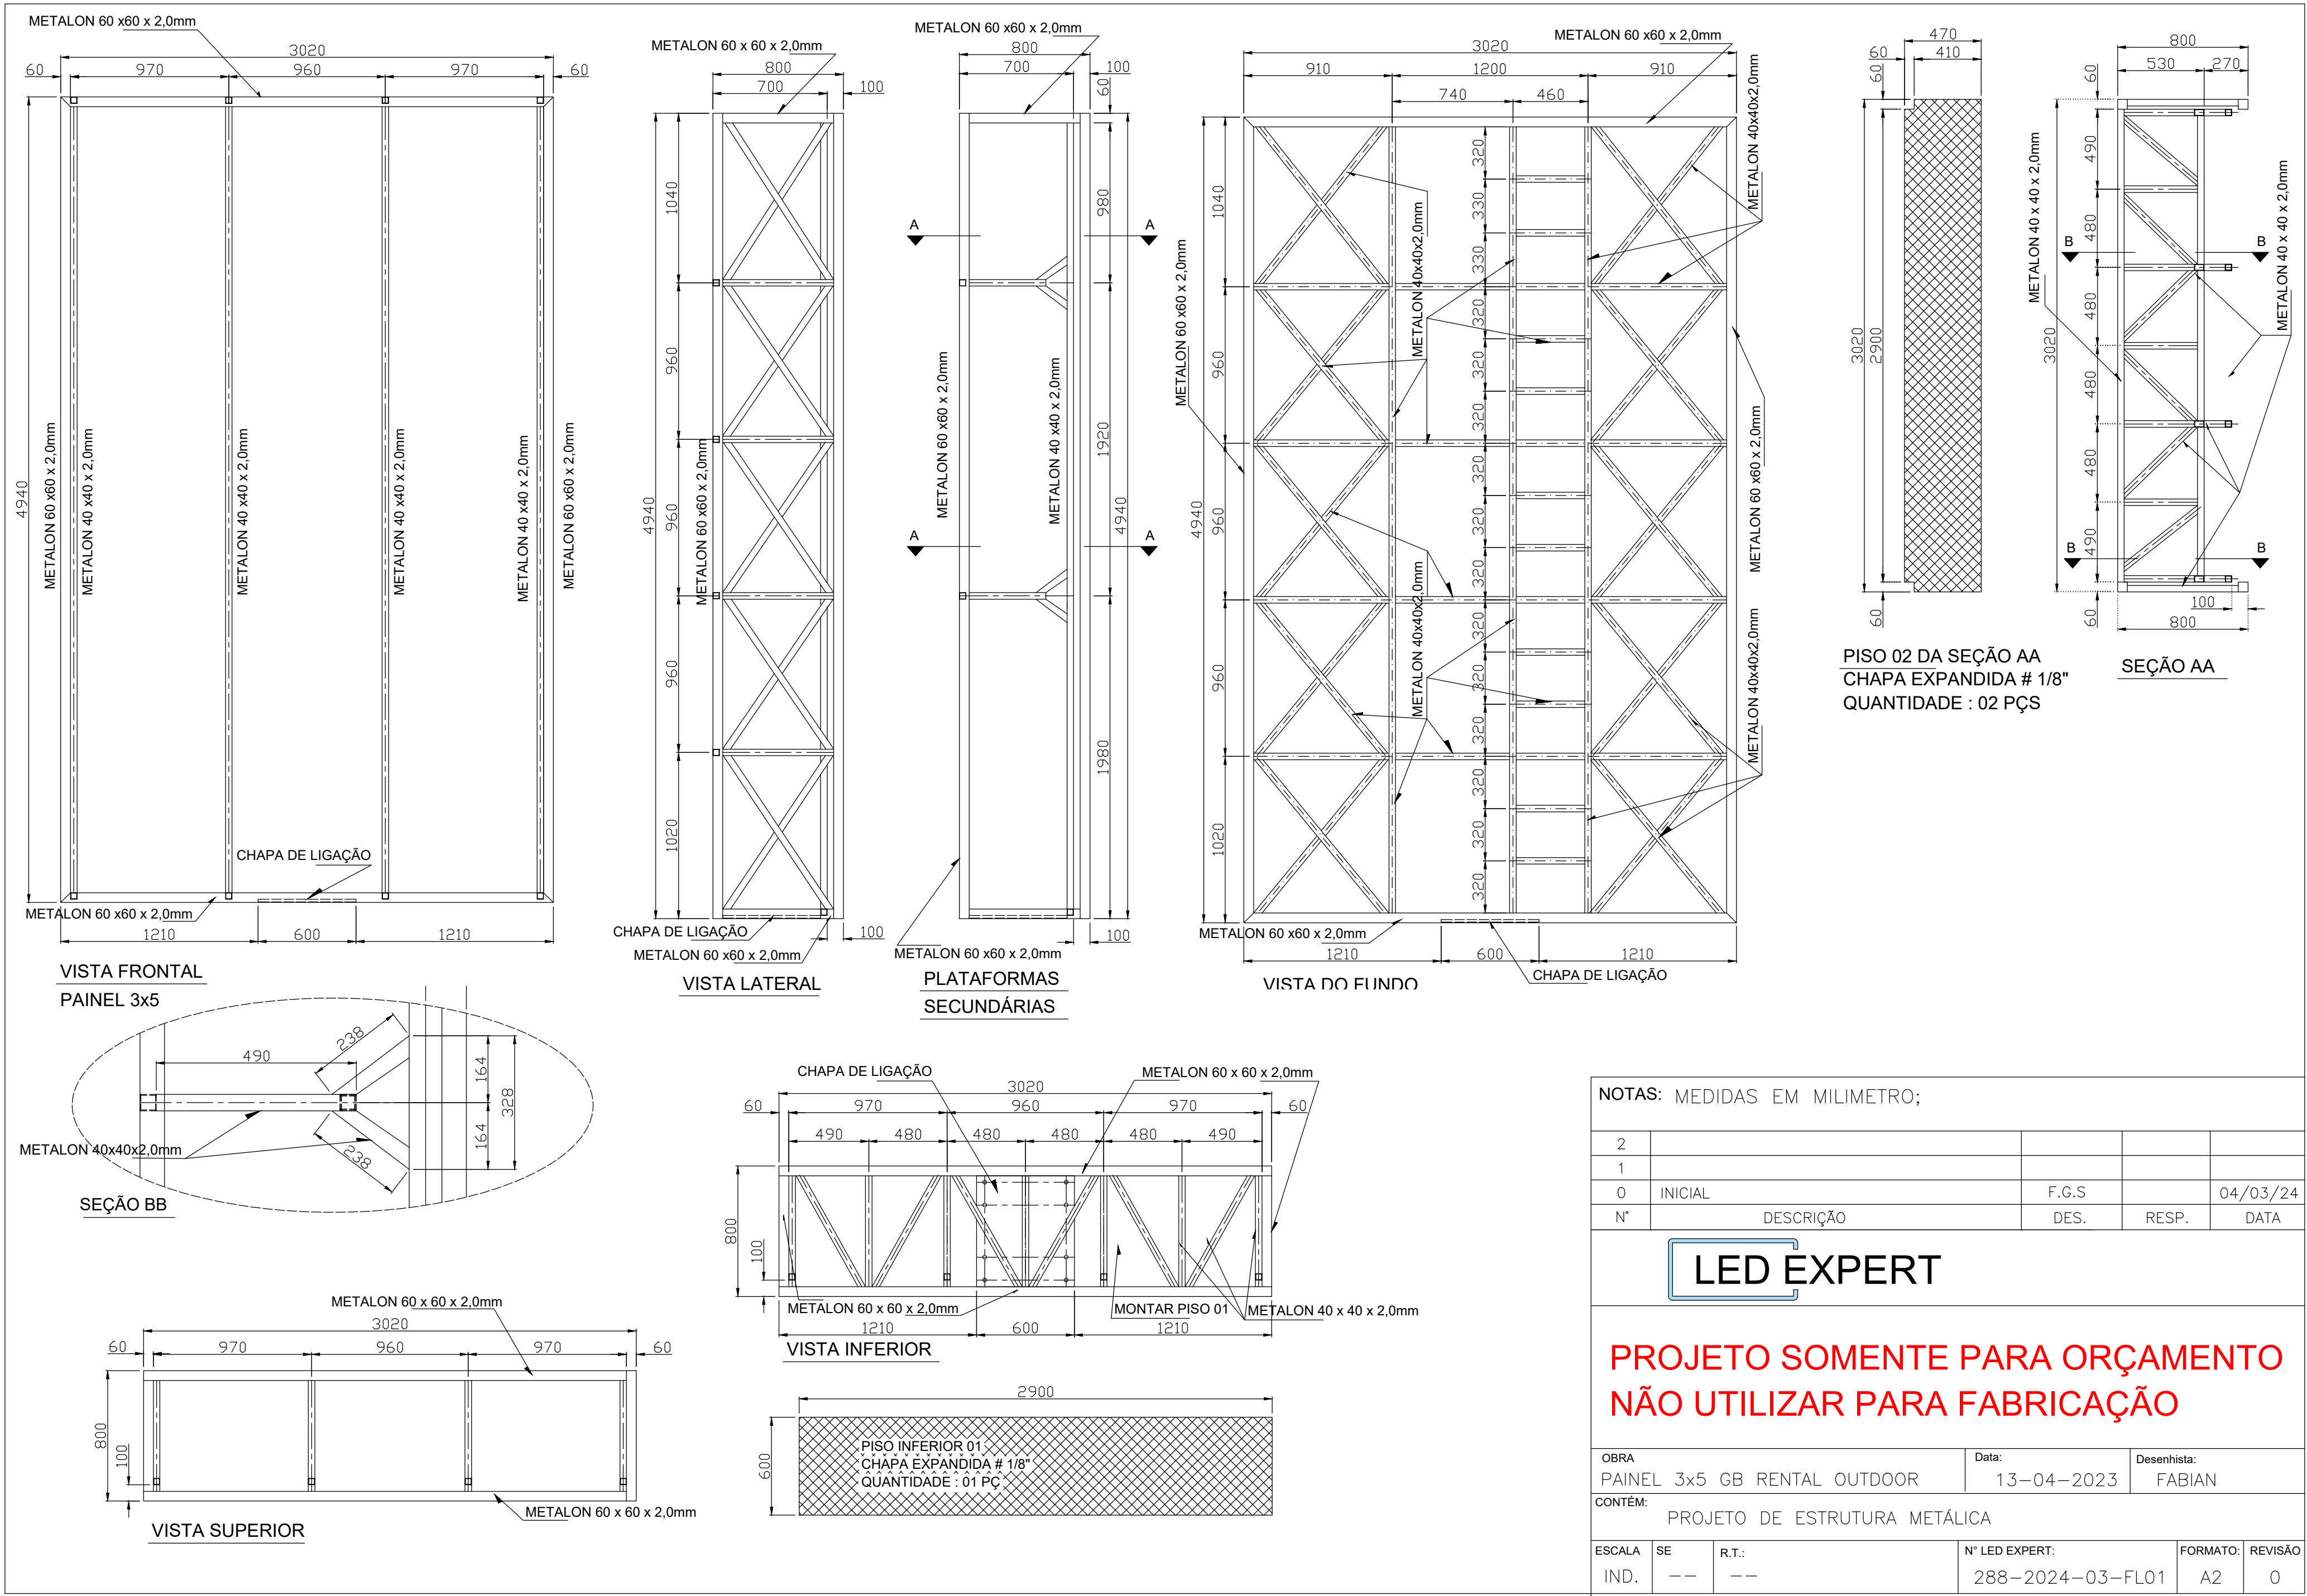


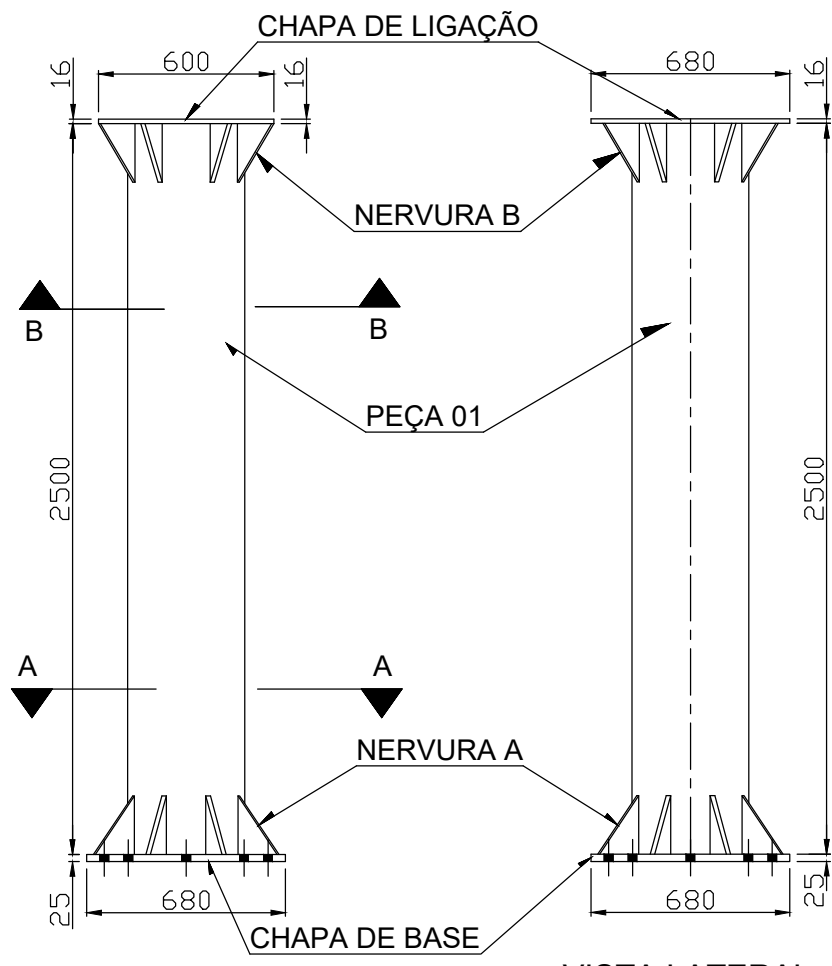


NOTAS: MEDIDAS EM MILIMETRO;					
2					
1					
0	INICIAL	F.G.S		04/03/24	
N°	DESCRIÇÃO	DES.	RESP.	DATA	
LED EXPERT					
PROJETO SOMENTE PARA ORÇAMENTO NÃO UTILIZAR PARA FABRICAÇÃO					
OBRA PAINEL 3x5 GB RENTAL OUTDOOR		Data: 13-04-2023		Desenhista: FABIAN	
CONTÉM: PROJETO DE ESTRUTURA METÁLICA					
ESCALA IND.	SE --	R.T.: --	N° LED EXPERT: 288-2024-03-FL01	FORMATO: A2	REVISÃO 0

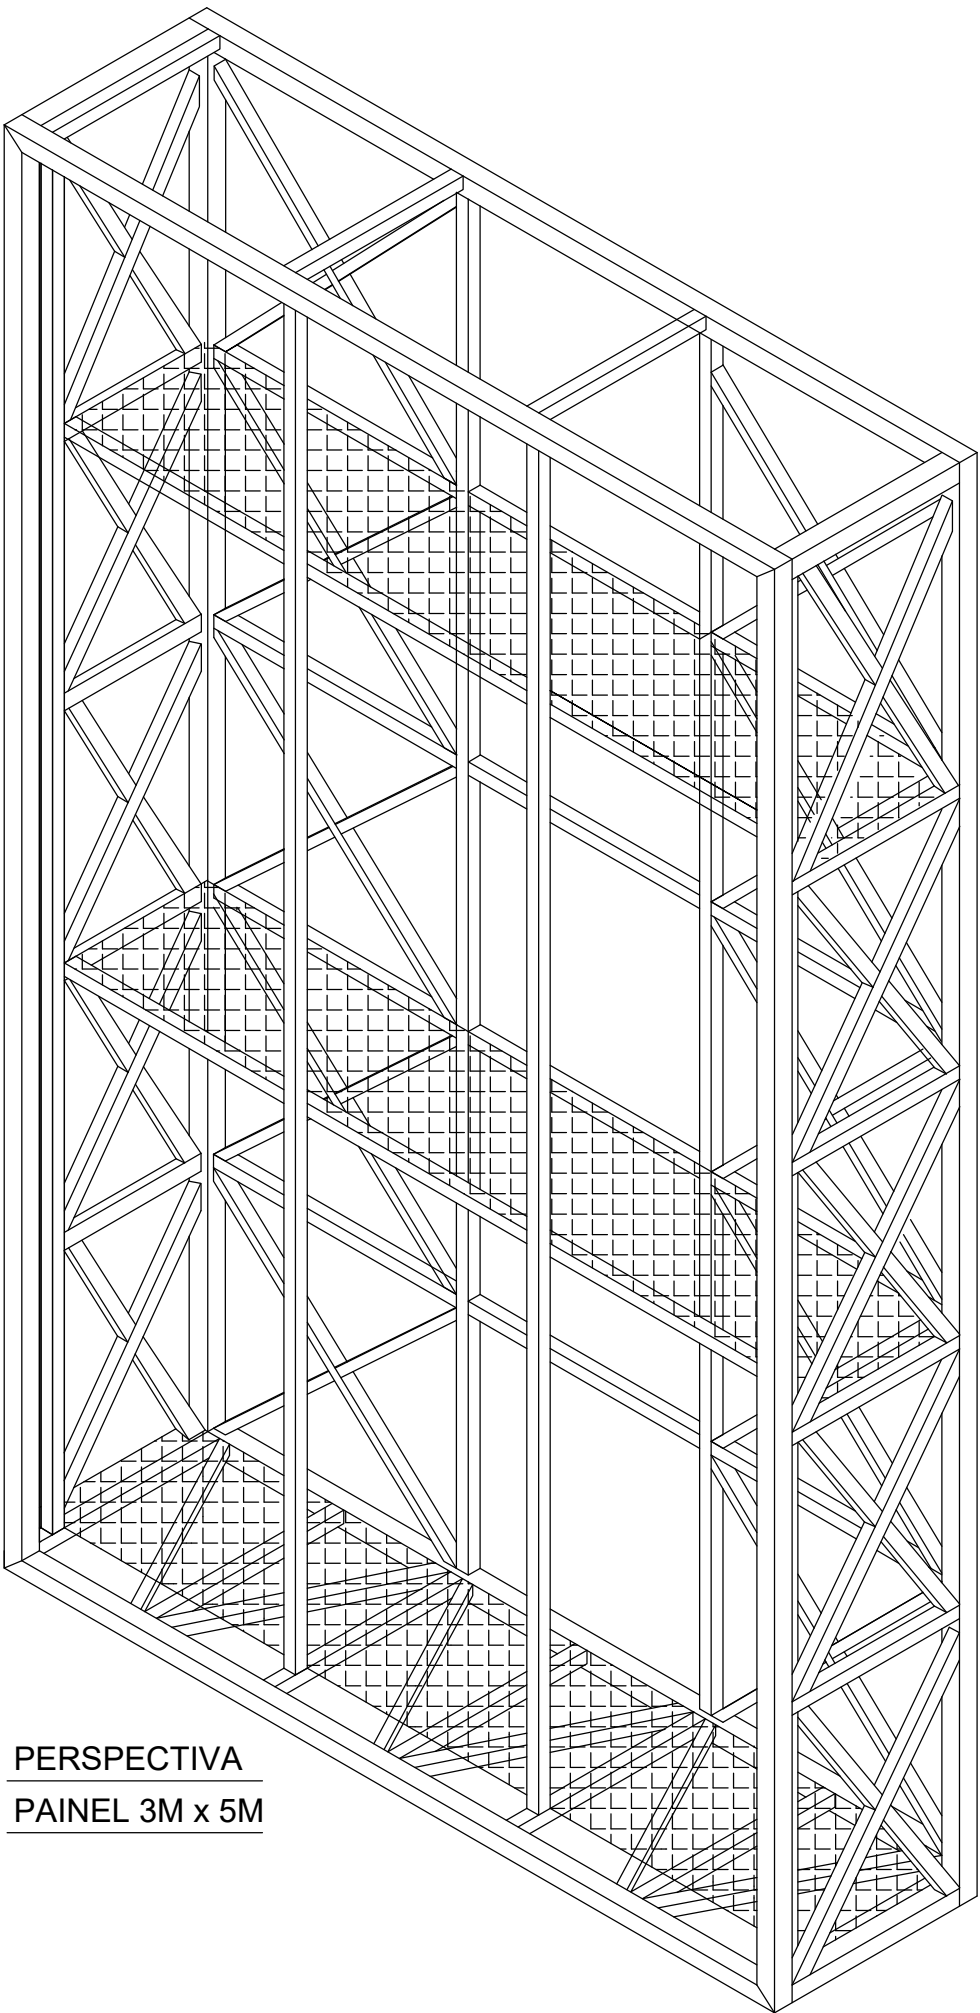

PILAR
VISTA FRONTAL
QUANTIDADE: 01 PÇ

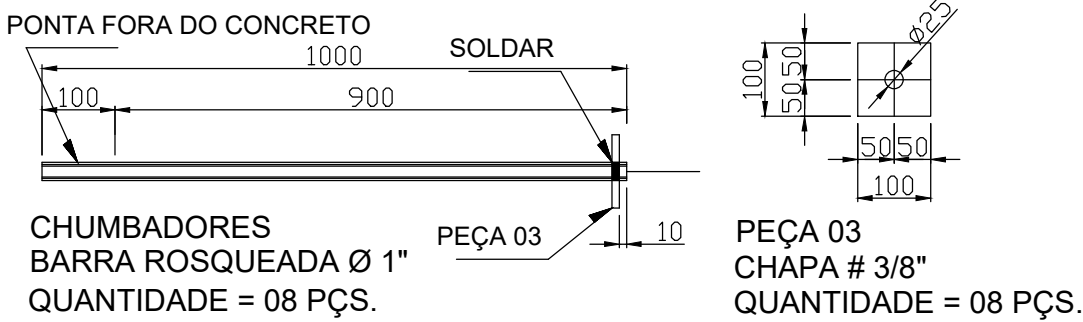

PERSPECTIVA
PAINEL 3M x 5M

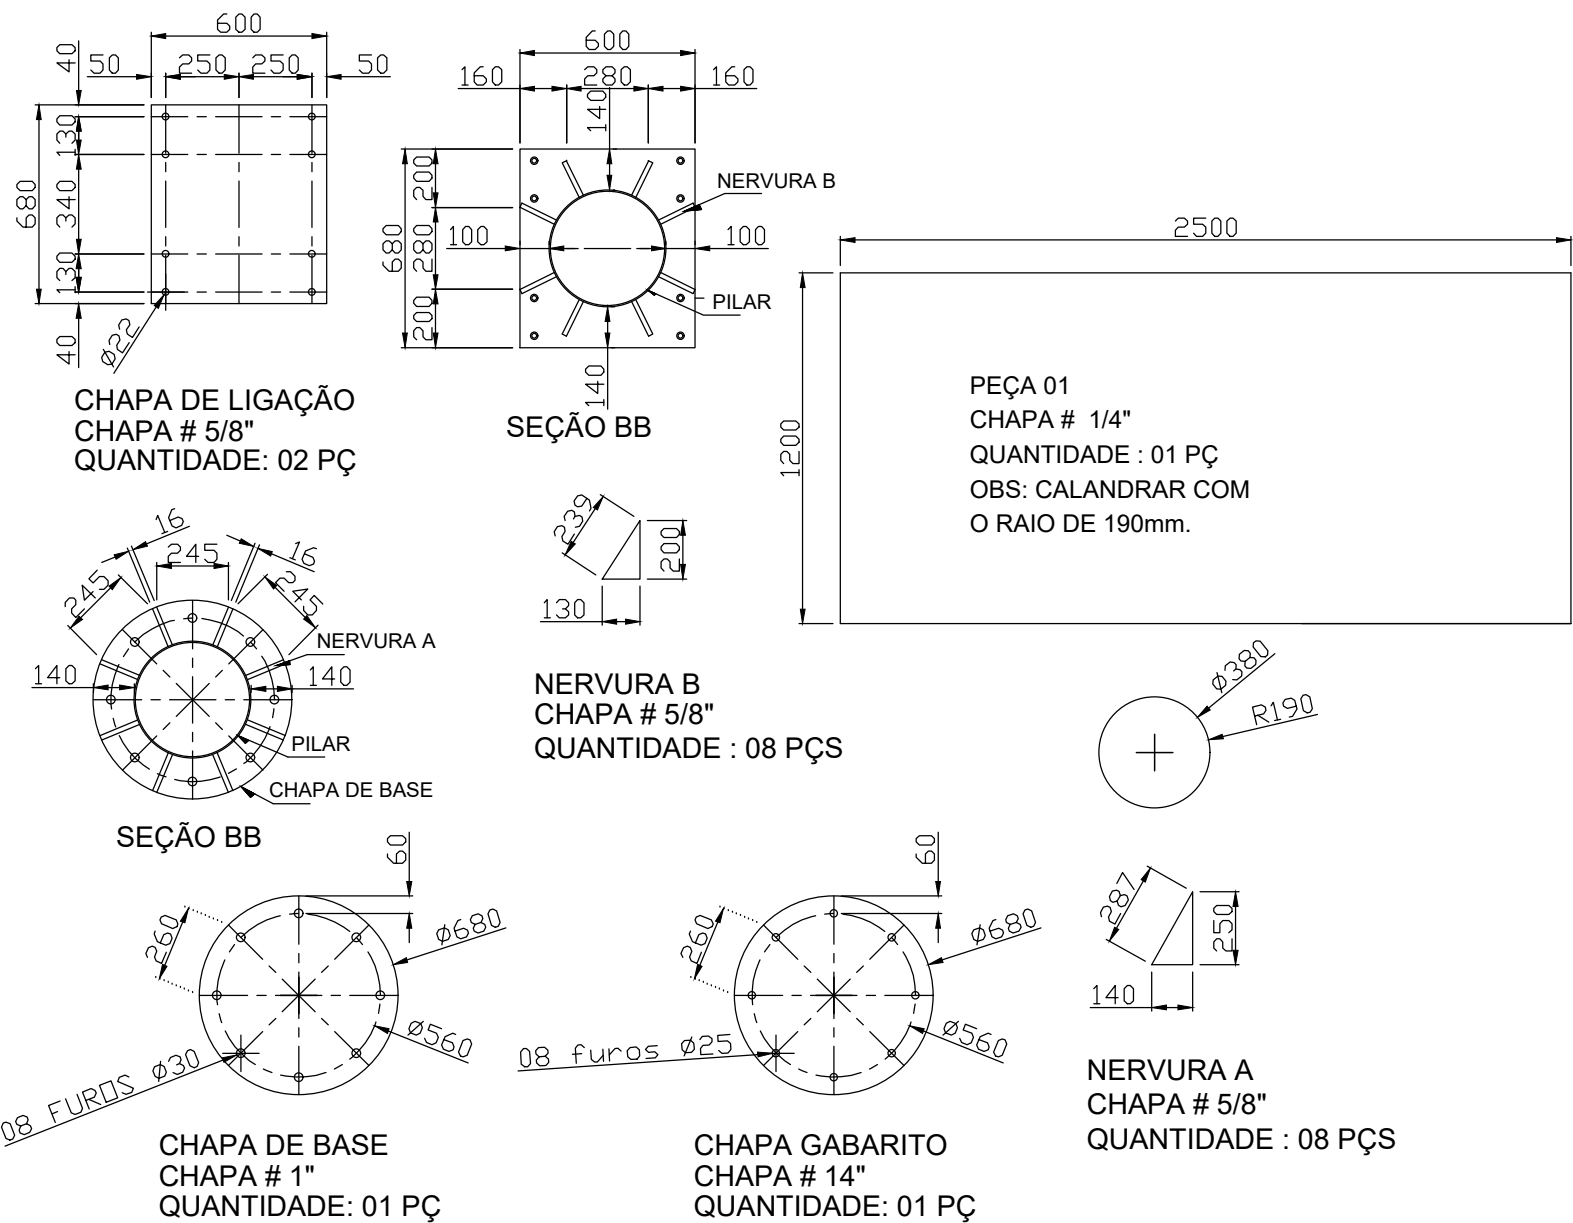

LISTA DE MATERIAIS						
Cliente: MATHEUS				DATA: 04/03/2024		
Obra: PAINEL 3x5 GB RENTAL OUTDOOR PILAR 2,0 MTS						
	ESTRUTURA METÁLICA					
	DESCRIÇÃO	COMPR.	UNID.	QUANT.	PESO UNIT.	PESO TOTAL
01	METALON 60x60x2,0mm	6000mm	PÇS	06	3,66 KG/M	131,76 KG
02	METALON 40x40x2,0mm	6000mm	PÇS	25	2,41 KG/M	361,50 KG
03	CHAPA EXPANDIDA # 1/8" x 600mm(PISO 01)	2900mm	PÇS	01	4,2 KG/M2	7,30 KG
04	CHAPA EXPANDIDA # 1/8" x 470mm(PISO 02)	3020mm	PÇS	02	4,2 KG/M2	11,92 KG
05	CHAPA BASE # 1"	ø 680mm	PÇS	01	196,00 KG/M2	71,14 KG
06	CHAPA DE LIGAÇÃO # 5/8" x 600mm	680mm	PÇS	02	125,44 KG/M2	102,35 KG
07	CHAPA NERVURA A # 5/8" x 140mm	250mm	PÇS	08	125,44 KG/M2	17,56 KG
08	CHAPA NERVURA B # 5/8" x 130mm	200mm	PÇS	08	125,44 KG/M2	13,04 KG
09	CHAPA PILAR # 1/4" x 1200 mm (PEÇA 01)	200mm	PÇS	01	49,39 KG/M2	152,91 KG
10	CHAPA # 14 (GABARITO)	ø 680mm	PÇS	01	16,00 KG/M2	5,80 KG
11	BARRA ROSQUEADA ø 1"	1000mm	PÇS	08	3,98 KG	31,84 KG
12	CHAPA # 3/8" x 100mm (PEÇA 03)	100mm	PÇS	08	74,48 KG/M2	5,95 KG
13						
				PESO TOTAL GERAL : 913,07 KG		

NOTAS: MEDIDAS EM MILIMETRO;

2				
1				
0	INICIAL	F.G.S		04/03/24
N°	DESCRIÇÃO	DES.	RESP.	DATA

LED EXPERT

PROJETO SOMENTE PARA ORÇAMENTO
NÃO UTILIZAR PARA FABRICAÇÃO

OBRA			Data:		Desenhista:	
PAINEL 3x5 GB RENTAL OUTDOOR			04-03-2024		FABIAN	
CONTÉM: PROJETO DE ESTRUTURA METÁLICA						
ESCALA	SE	R.T.:	N° LED EXPERT:		FORMATO:	REVISÃO
IND.	--	--	288-2024-03-FL02		A2	0