

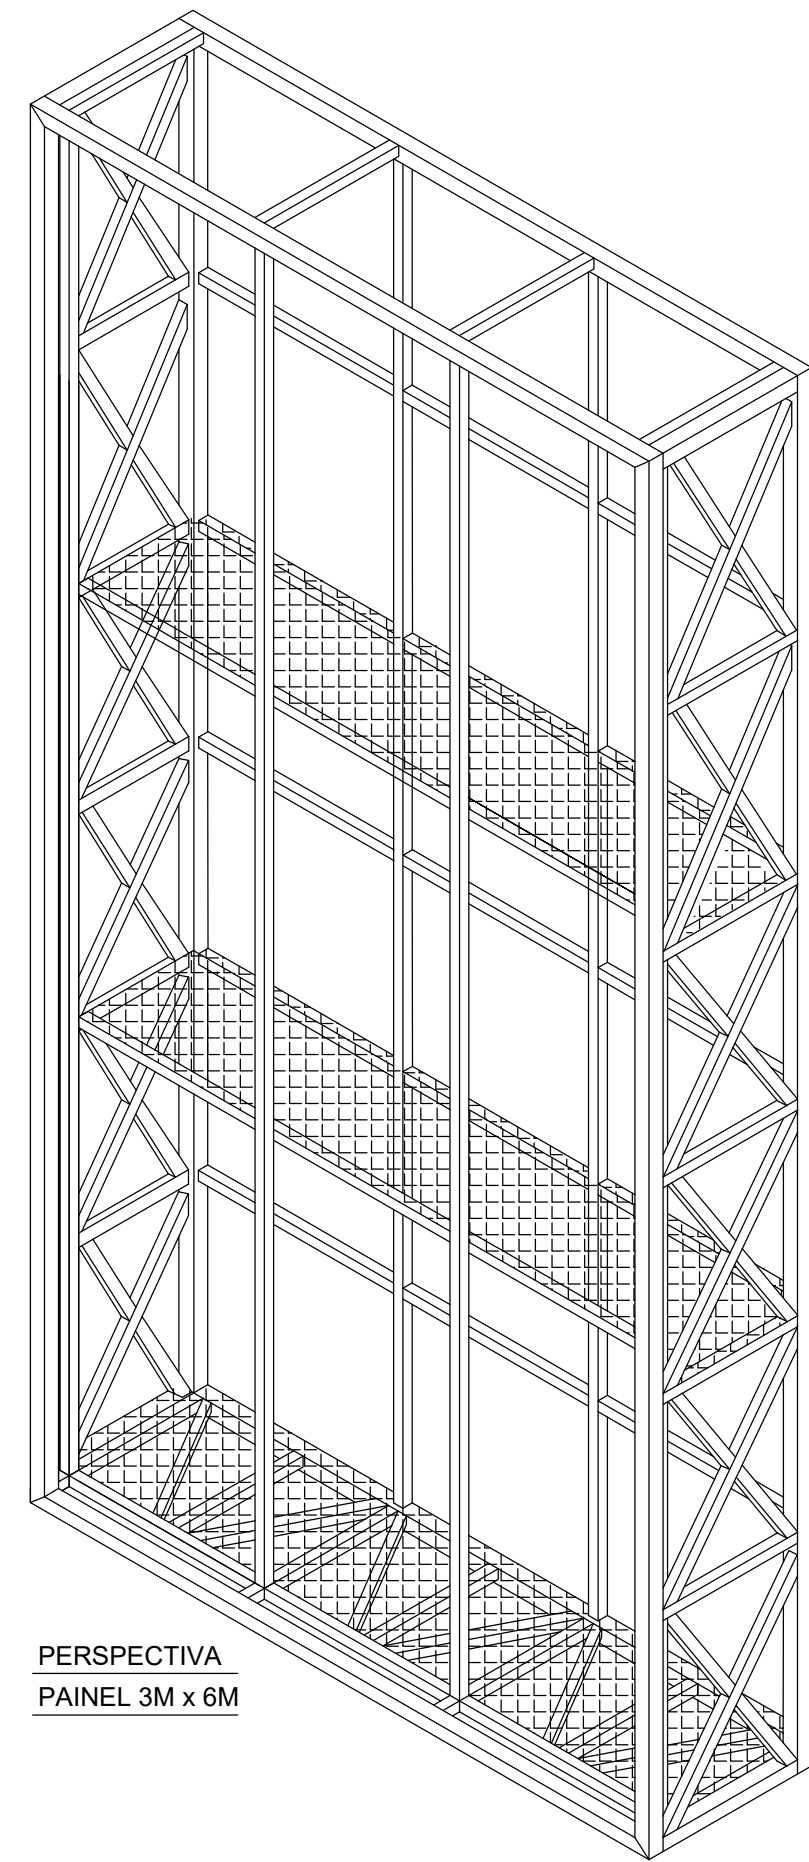
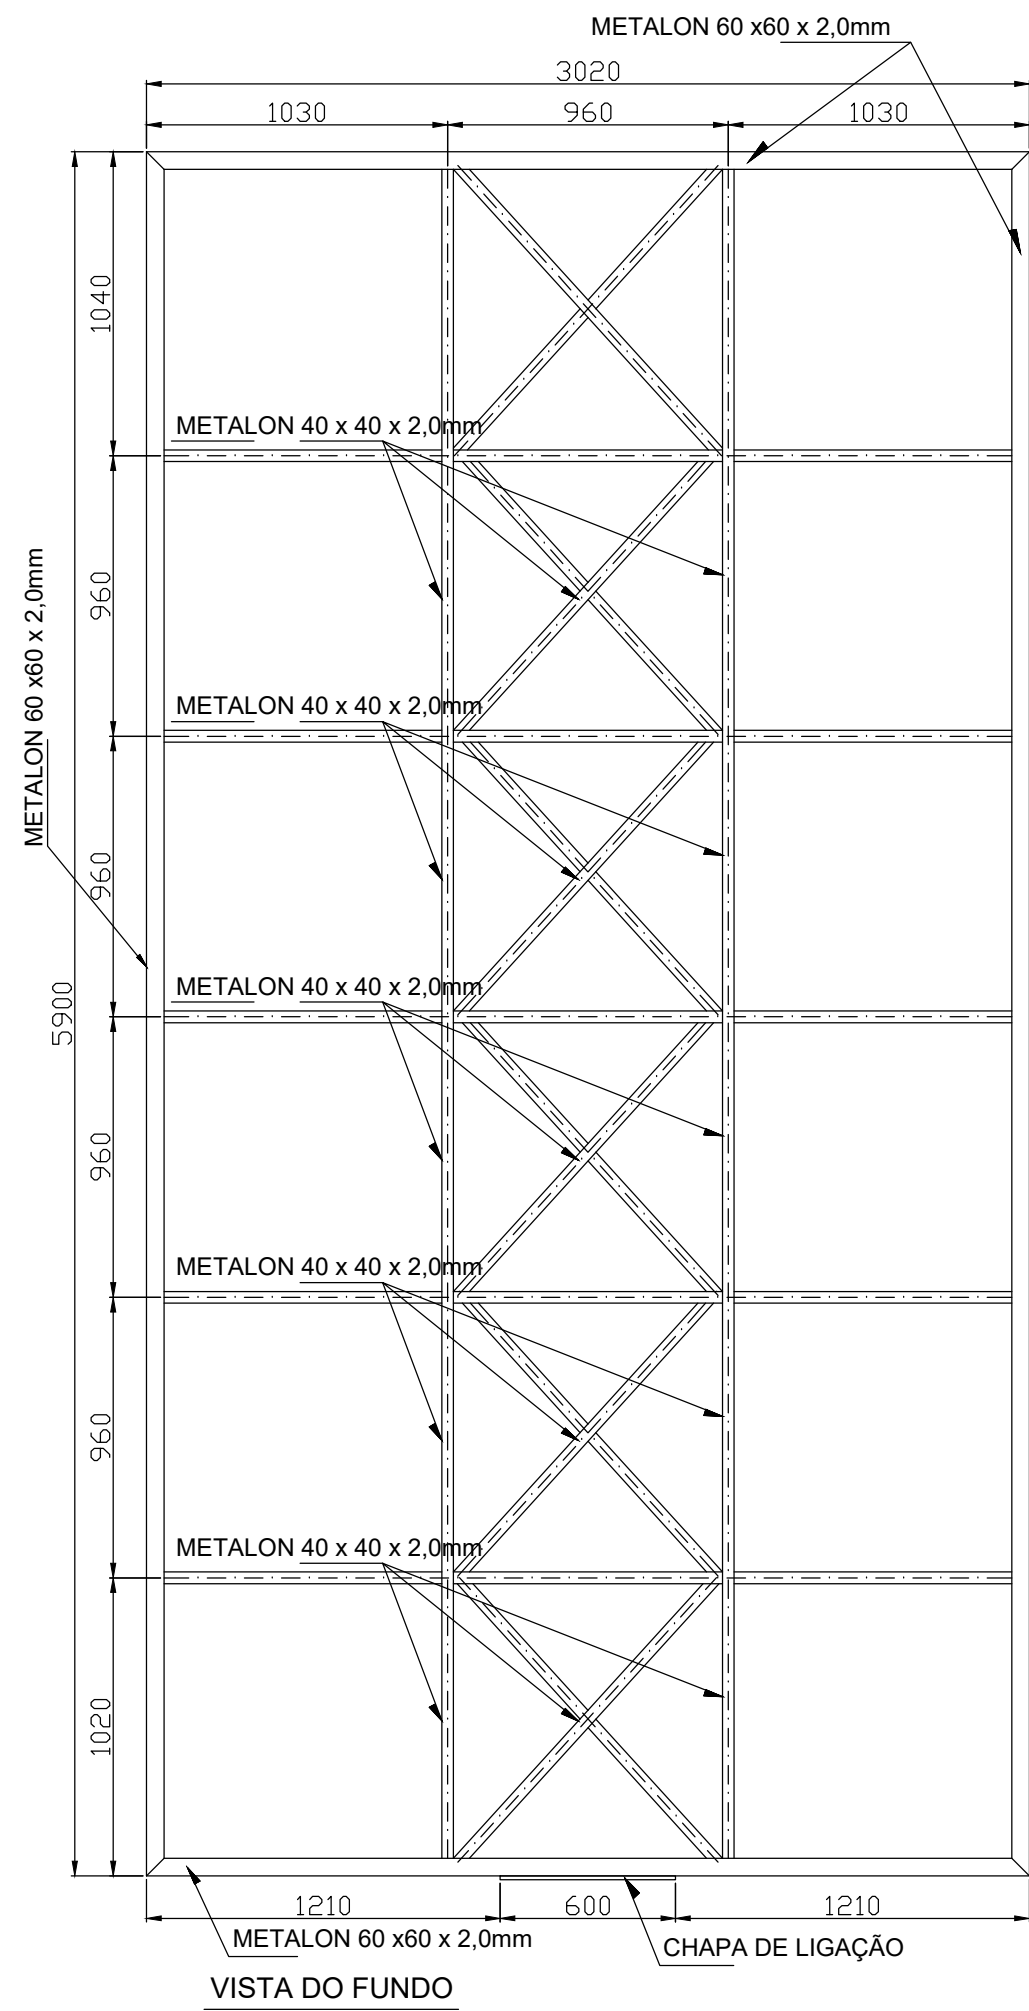
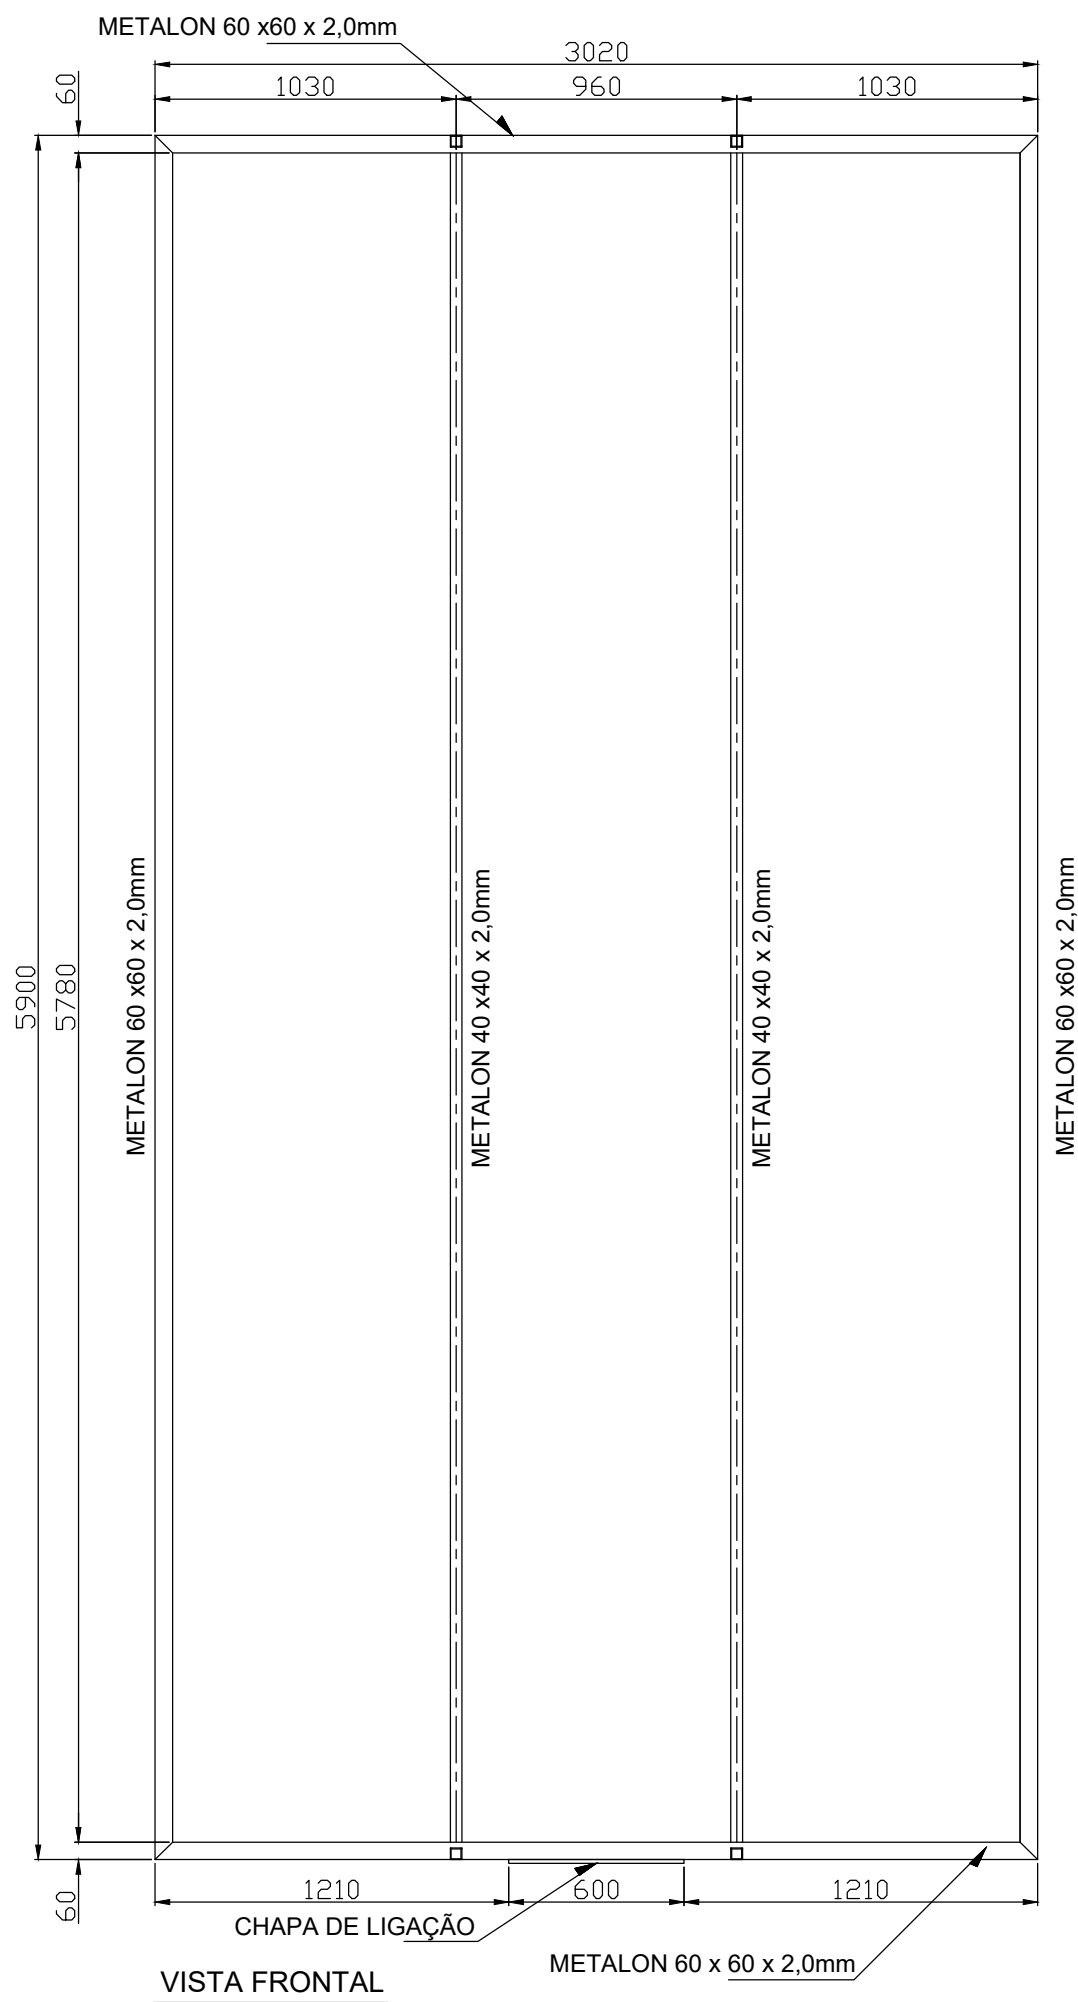
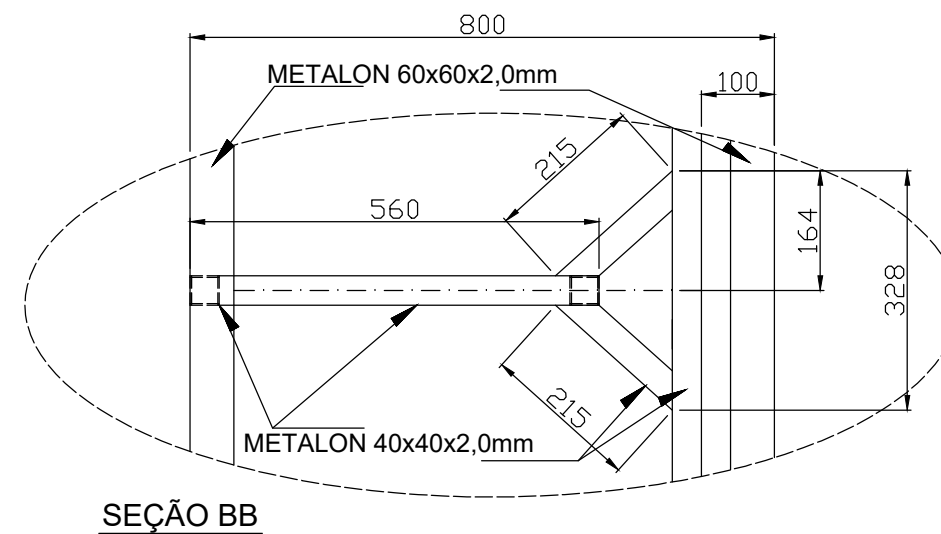


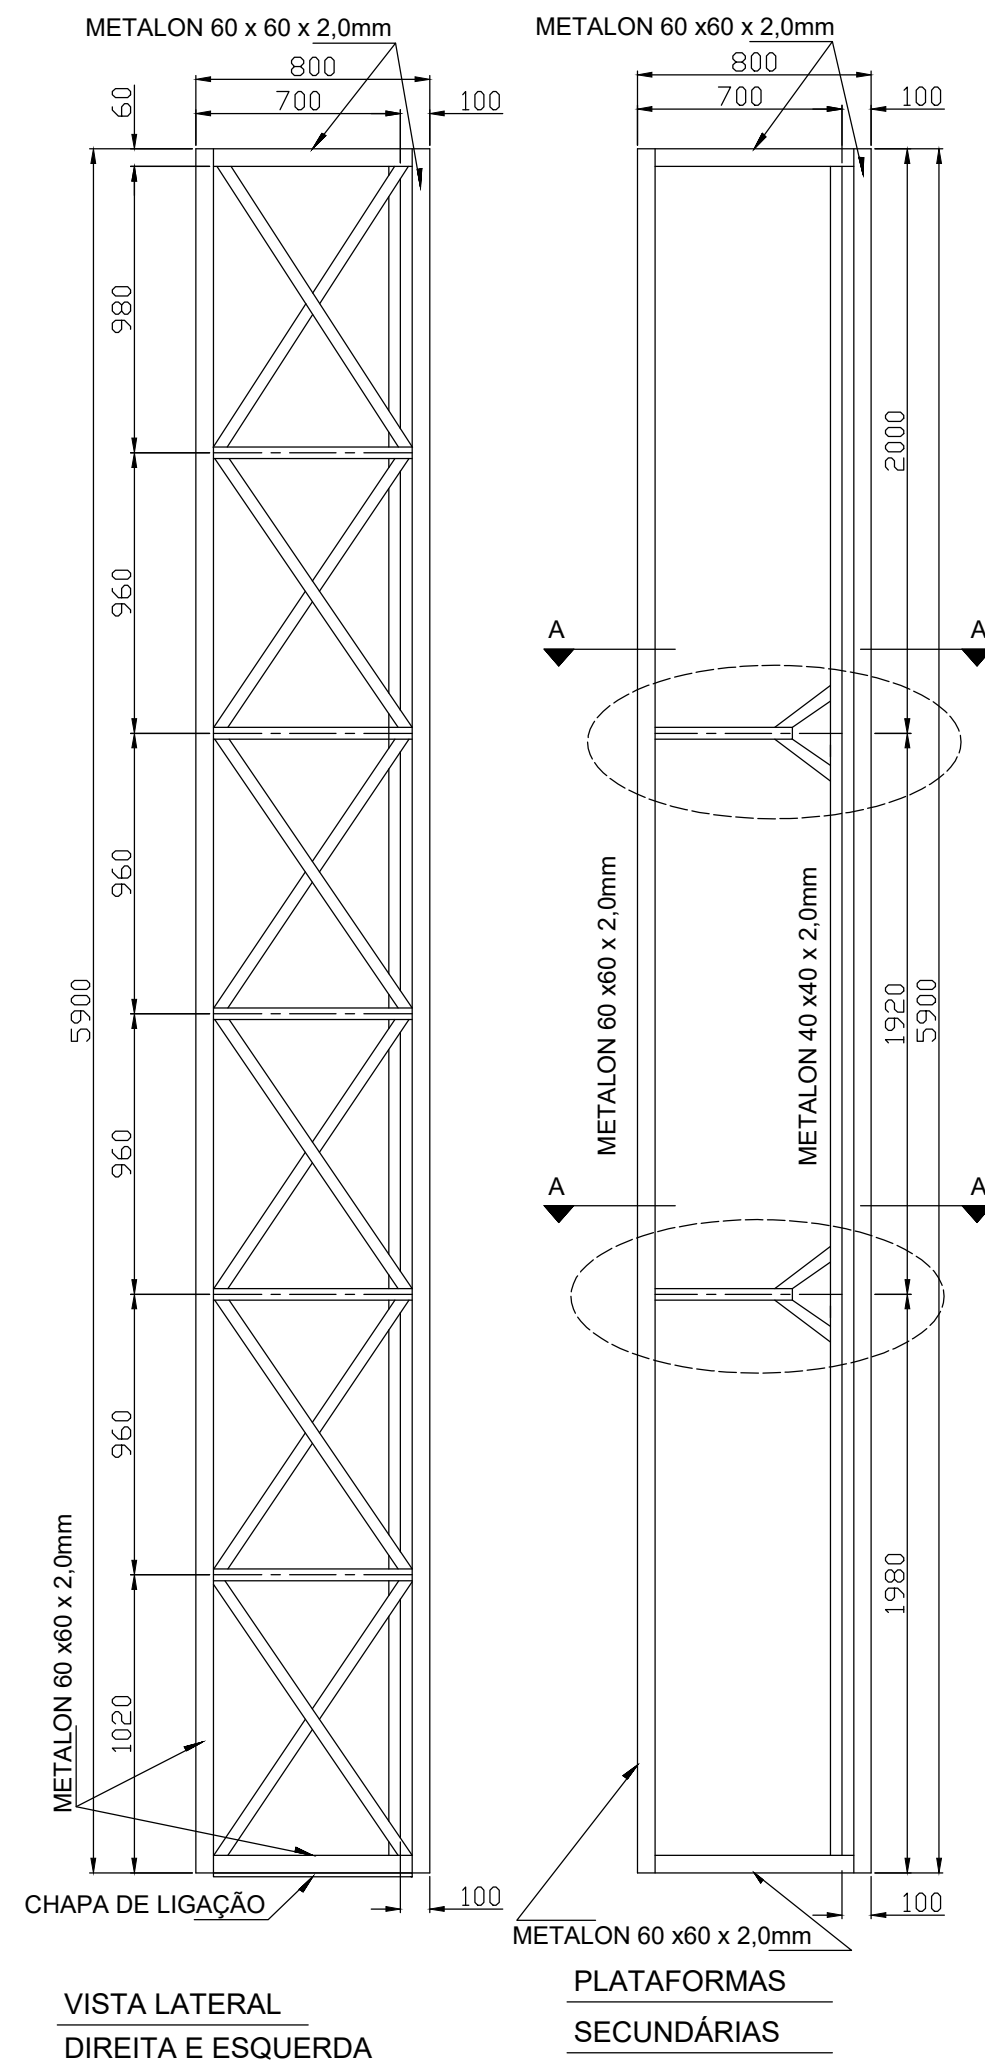

NOTAS: MEDIDAS EM MILIMETRO;					
2					
1	REVISÃO	F.G.S		20/09/23	
0	INICIAL	F.G.S		18/09/23	
N°	DESCRIÇÃO	DES.	RESP.	DATA	
LED EXPERT					
PROJETO SOMENTE PARA ORÇAMENTO NÃO UTILIZAR PARA FABRICAÇÃO					
OBRA PAINEL 3 x 6 GB RENTAL OUTDOOR		Data: 18-09-2023	Desenhista: FABIAN		
CONTÉM: PROJETO DE ESTRUTURA METÁLICA					
ESCALA IND.	SE --	R.T.: --	N° LED EXPERT: 183-2023-09-FL01	FORMATO: A2	REVISÃO 00

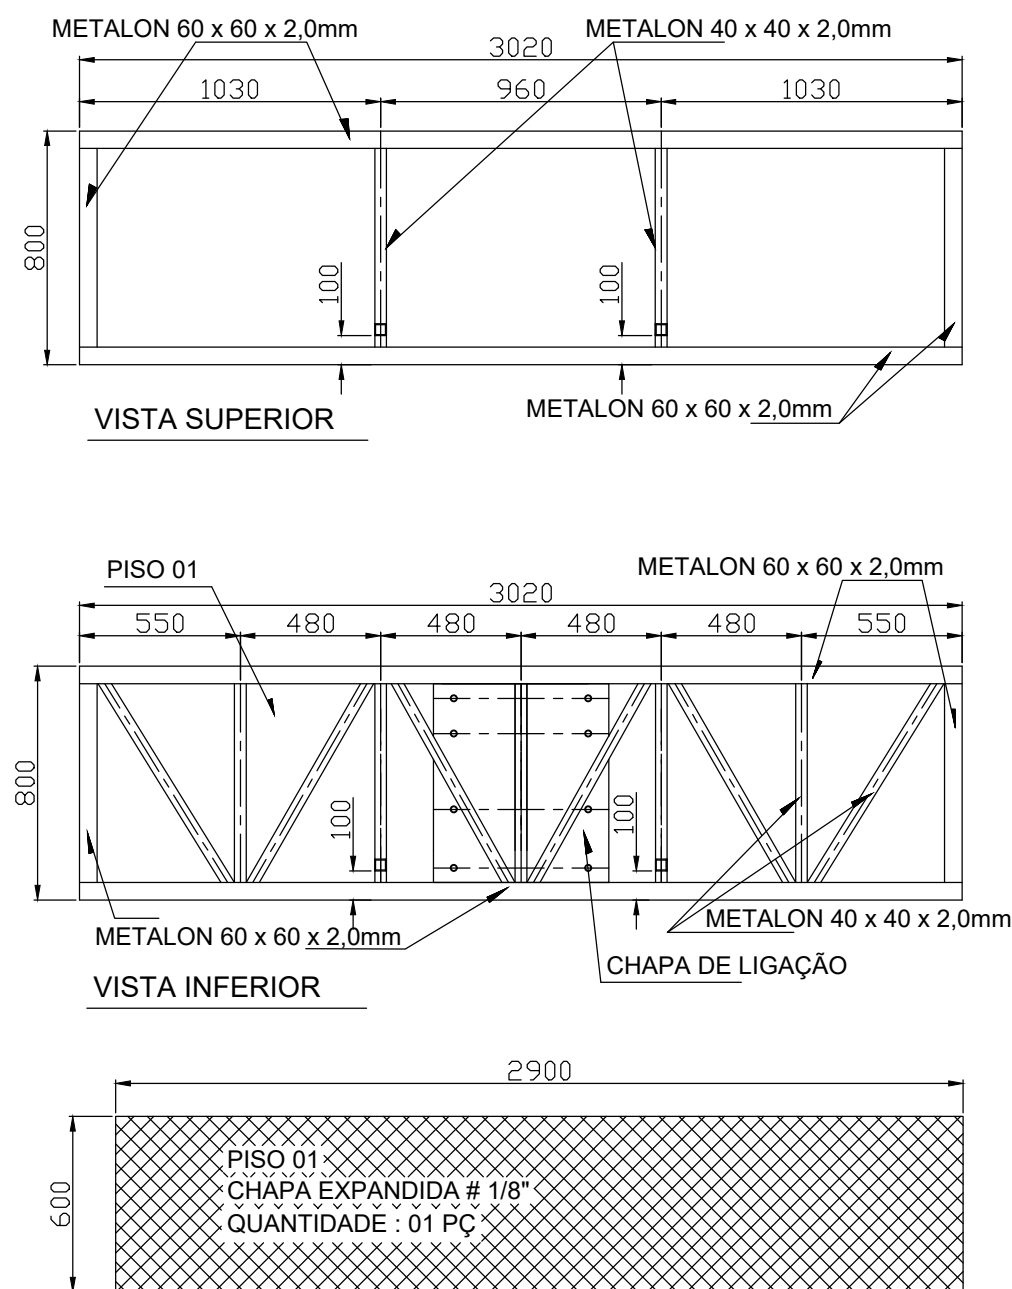

LISTA DE MATERIAIS						
Cliente: AGÊNCIA IMPULSONE				DATA: 18/09/2023		
Obra: PAINEL 3x6 GB RENTAL OUTDOOR PILAR 2,1 METROS				REVISÃO 01: 20/09/2023		
	ESTRUTURA METÁLICA					
	DESCRIÇÃO	COMPR.	UNID.	QUANT.	PESO UNIT.	PESO TOTAL.
01	METALON 60x60x2,0mm	6000mm	PÇS	12	3,66 KG	263,52 KG
02	METALON 40x40x2,0mm	6000mm	PÇS	15	2,41 KG	216,90 KG
03	CHAPA EXPANDIDA # 1/8" x 600mm (PISO 01)	2900mm	PÇS	01	4,2 KG/M2	7,30 KG
04	CHAPA EXPANDIDA # 1/8" x 560mm (PISO 02)	3020mm	PÇS	02	4,2 KG/M2	14,20 KG
05	CHAPA BASE # 1" Ø 680mm	Ø 680mm	PÇS	01	196,00 KG/M2	71,14 KG
06	CHAPA DE LIGAÇÃO # 5/8" x 600mm	680mm	PÇS	02	125,44 KG/M2	102,40 KG
07	CHAPA # 5/8" x 140mm (PEÇA A)	250mm	PÇS	08	125,50 KG/M2	17,57 KG
08	CHAPA # 5/8" x 130mm (PEÇA B)	200mm	PÇS	08	125,50 KG/M2	13,05 KG
09	CHAPA # 5/16" x 1200mm (PILAR)	2100mm	PÇS	01	62,72 KG/M2	131,71 KG
10	CHAPA # 14 Ø 680mm (GABARITO)	Ø 680mm	PÇS	01	16,00 KG/M2	5,80 KG
11	BARRA ROSQUEADA Ø 1" (CHUMBADORES)	1000mm	PÇS	08	3,98 KG/M	31,84 KG
12	CHAPA # 3/8" x 100mm (PEÇA 03)	100mm	PÇS	08	74,48 KG/M2	5,95 KG
PESO TOTAL GERAL :					880,98 KG	


NOTAS: MEDIDAS EM MILIMETRO;

2				
1	REVISÃO	F.G.S		20/09/23
0	INICIAL	F.G.S		18/09/23
N°	DESCRIÇÃO	DES.	RESP.	DATA





LED EXPERT

PROJETO SOMENTE PARA ORÇAMENTO
NÃO UTILIZAR PARA FABRICAÇÃO


OBRA PAINEL 3 x 6 GB RENTAL OUTDOOR			Data: 18-09-2023	Desenhista: FABIAN	
CONTÉM: PROJETO DE ESTRUTURA METÁLICA					
ESCALA IND.	SE --	R.T.: --	Nº LED EXPERT: 183-2023-09-FL02	FORMATO: A2	REVISÃO 00

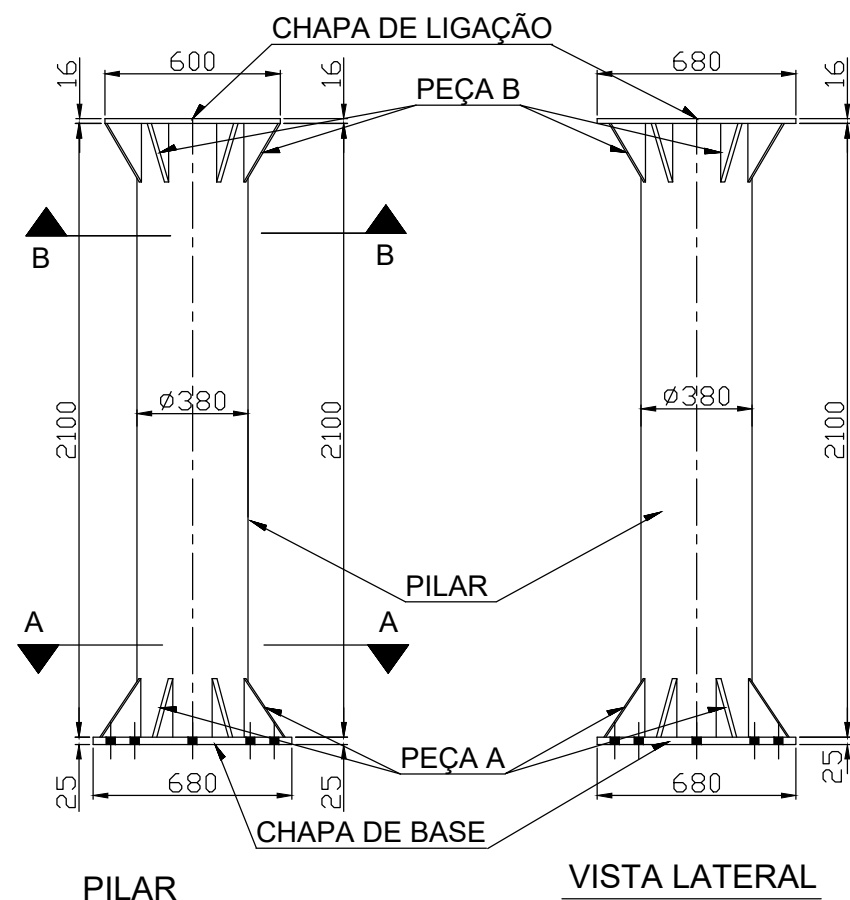


PILAR
VISTA DA FRENTE
QUANTIDADE: 01 PÇ

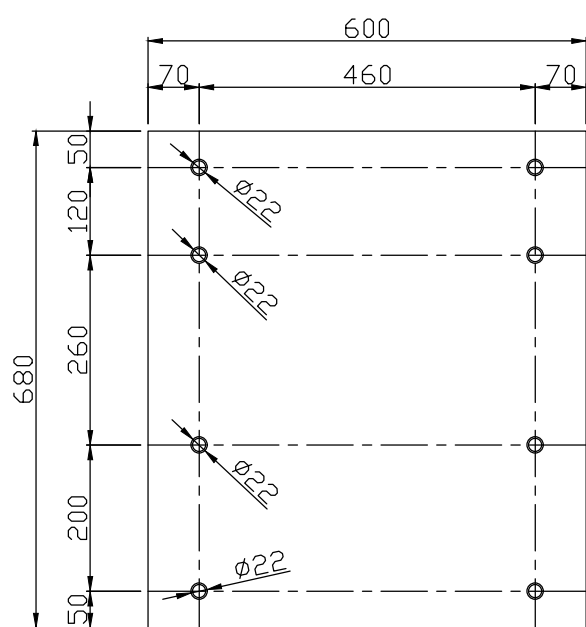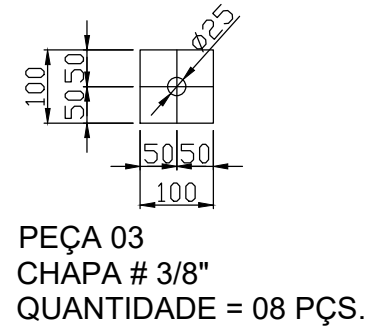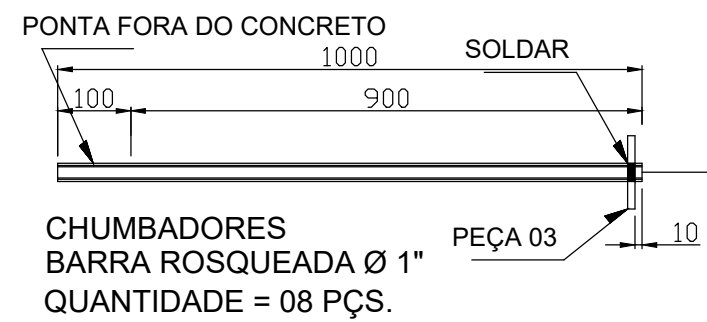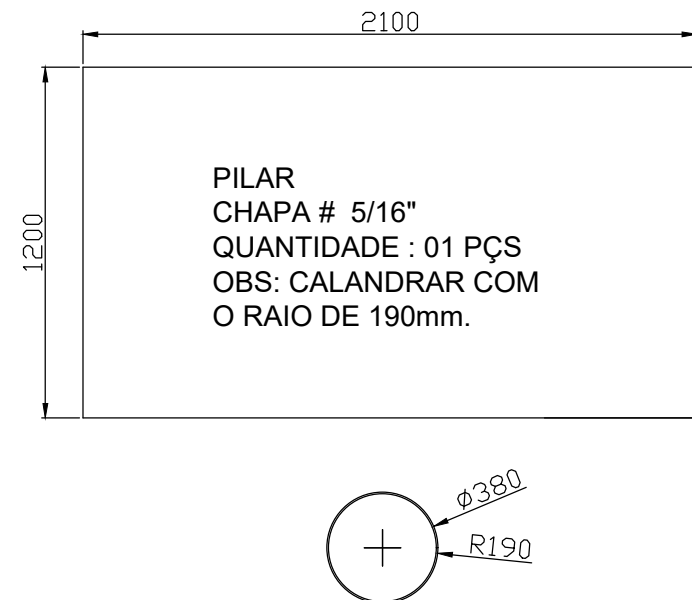


CHAPA DE LIGAÇÃO
CHAPA # 1/2"
QUANTIDADE: 02 PÇS

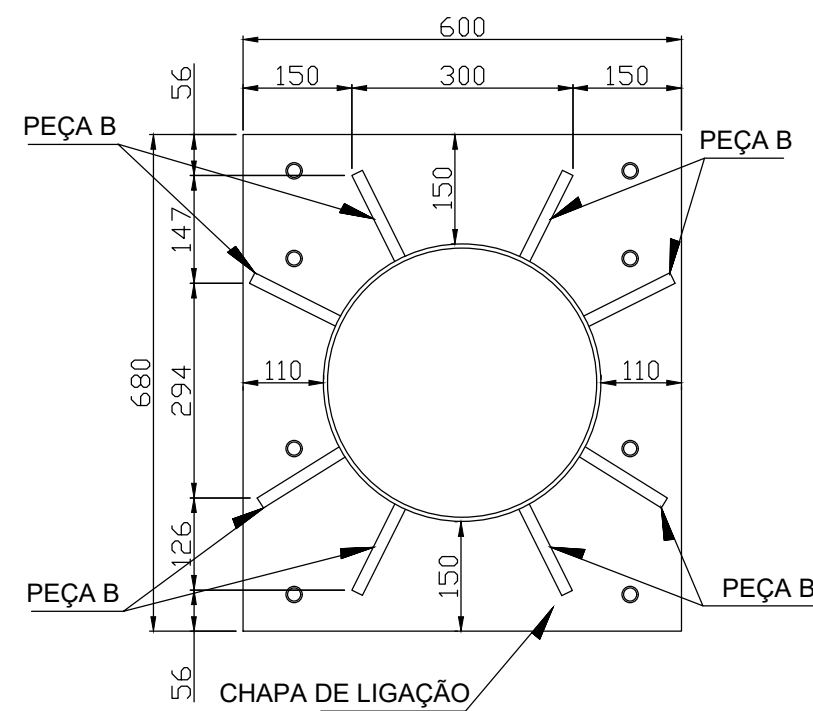


SEÇÃO BB

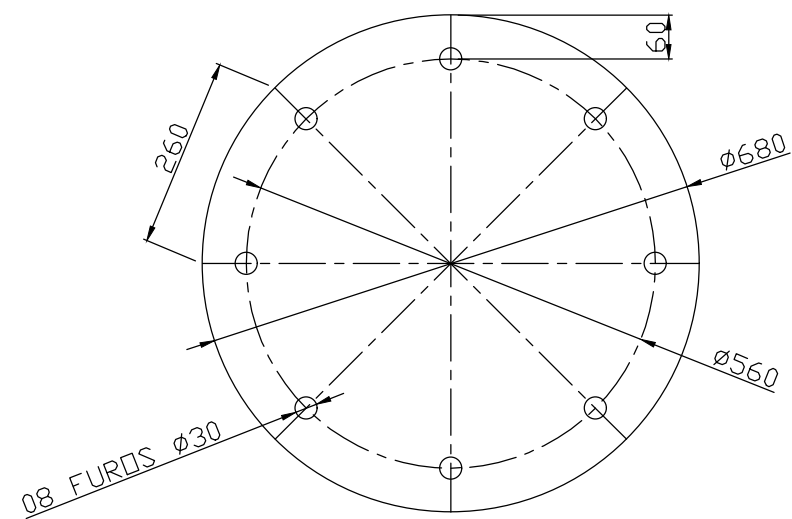


CHAPA DE BASE
CHAPA # 1"
QUANTIDADE: 01 PÇ

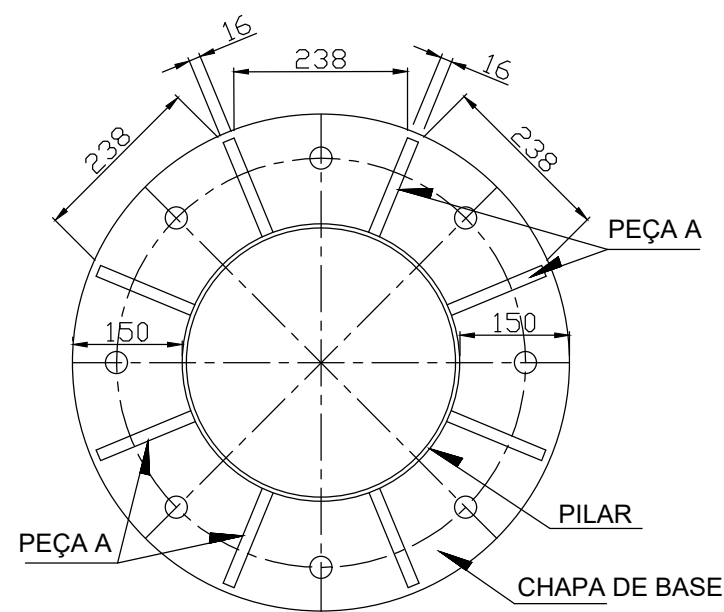


SEÇÃO AA

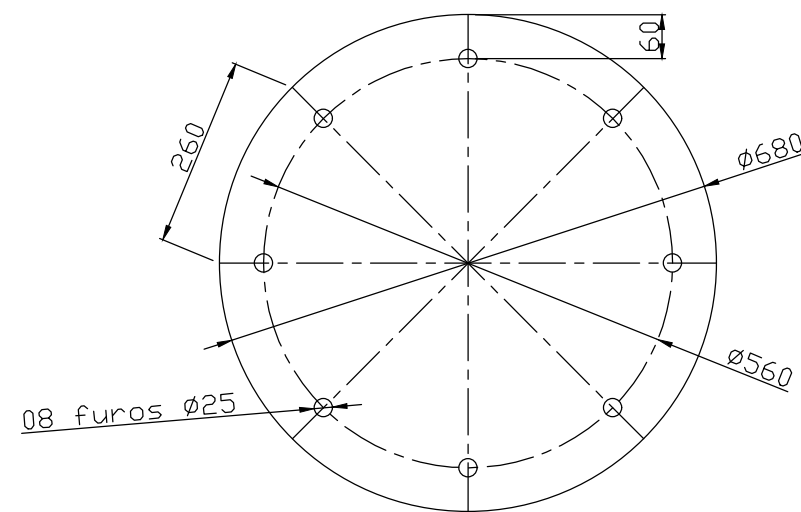

CHAPA GABARITO
CHAPA # 14"
QUANTIDADE: 01 PÇ

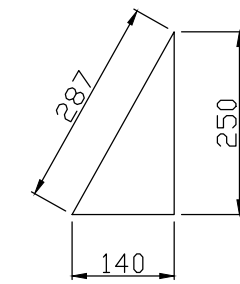

PEÇA A
CHAPA # 5/8"
QUANTIDADE : 08 PÇS

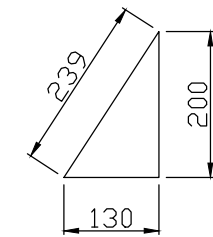

PEÇA B
CHAPA # 5/8"
QUANTIDADE : 08 PÇS

NOTAS: MEDIDAS EM MILIMETRO;

2				
1	REVISÃO	F.G.S		20/09/23
0	INICIAL	F.G.S		18/09/23
N°	DESCRIÇÃO	DES.	RESP.	DATA

LED EXPERT

PROJETO SOMENTE PARA ORÇAMENTO
NÃO UTILIZAR PARA FABRICAÇÃO

OBRA PAINEL 3 x 6 GB RENTAL OUTDOOR			Data: 18-09-2023	Desenhista: FABIAN	
CONTÉM: PROJETO DE ESTRUTURA METÁLICA – PILAR 2,1mm					
ESCALA	SE	R.T.:	Nº LED EXPERT:	FORMATO:	REVISÃO
IND.	--	--	183-2023-09-FL03	A2	00