




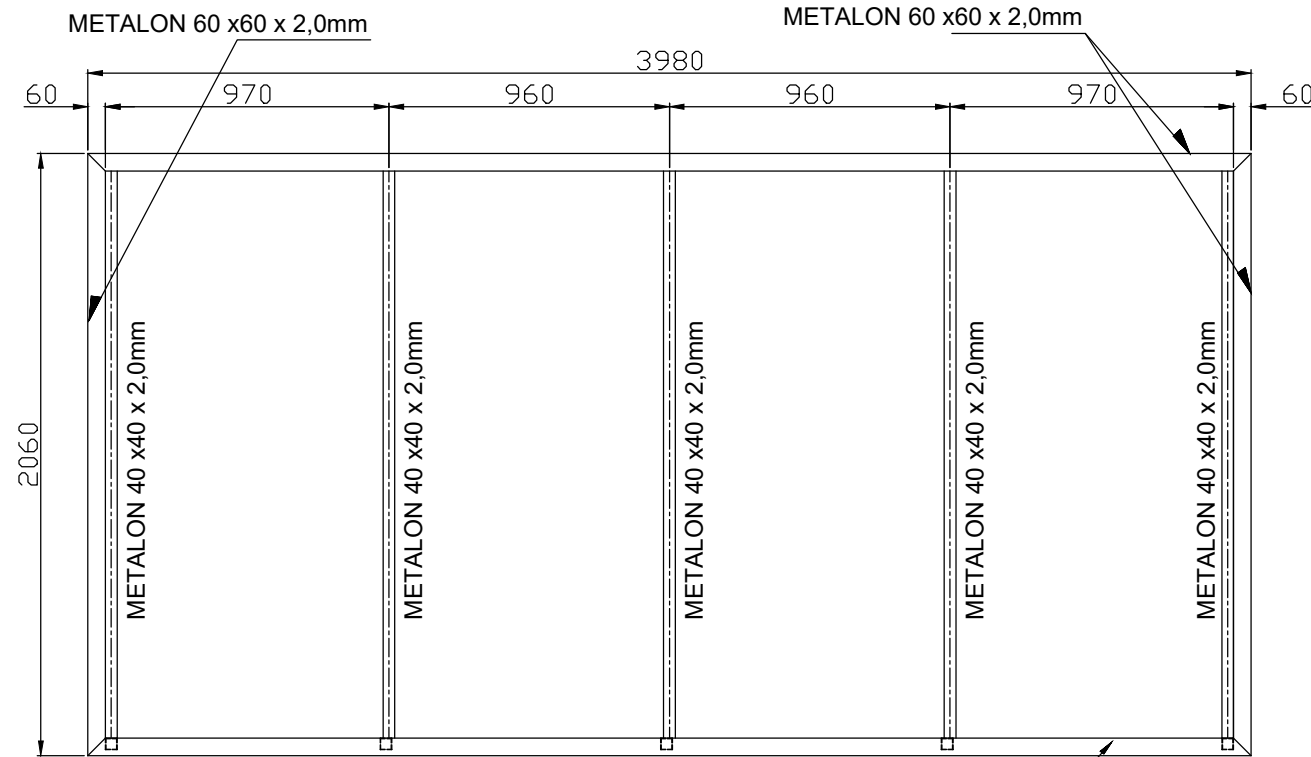


VISTA FRONTAL

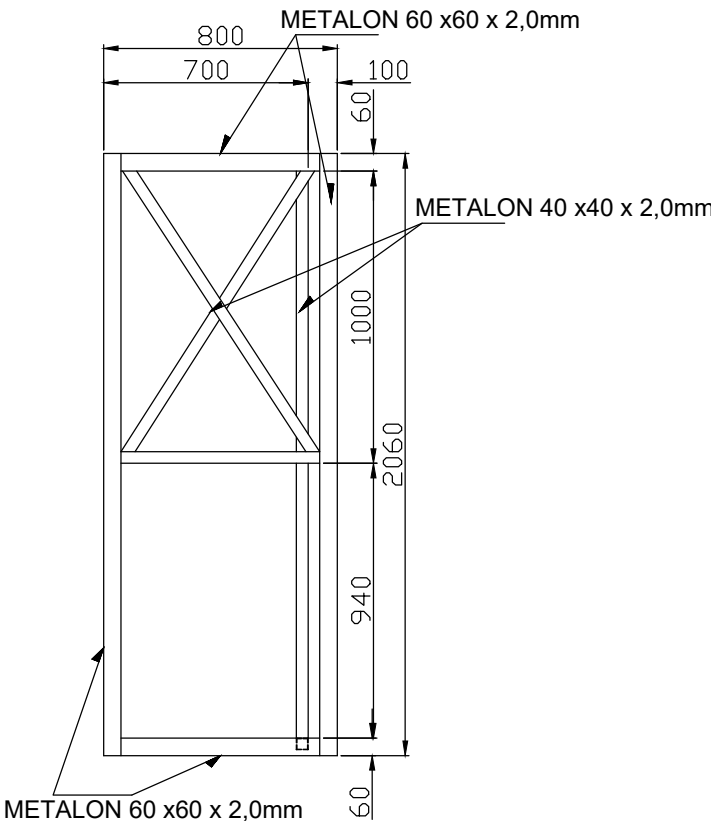


VISTA LATERAL

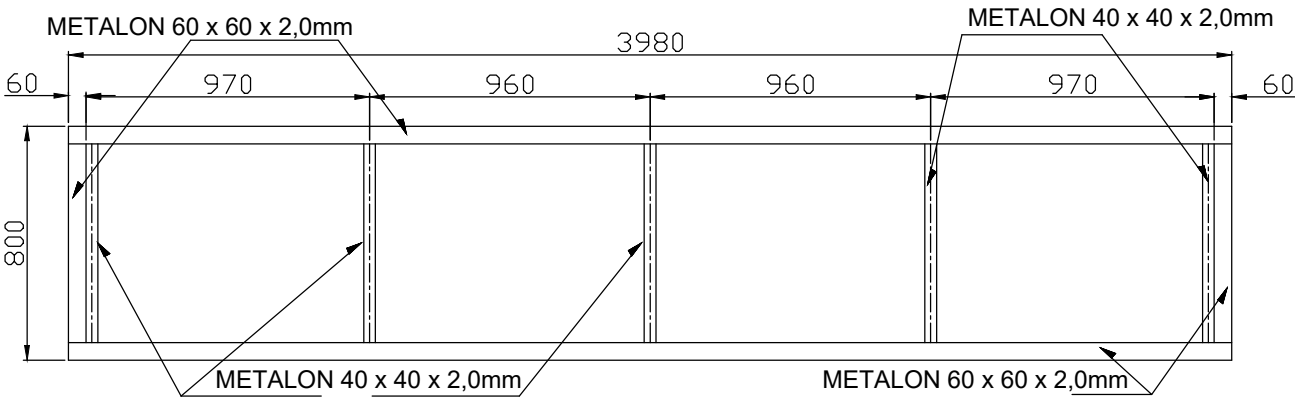



VISTA SUPERIOR

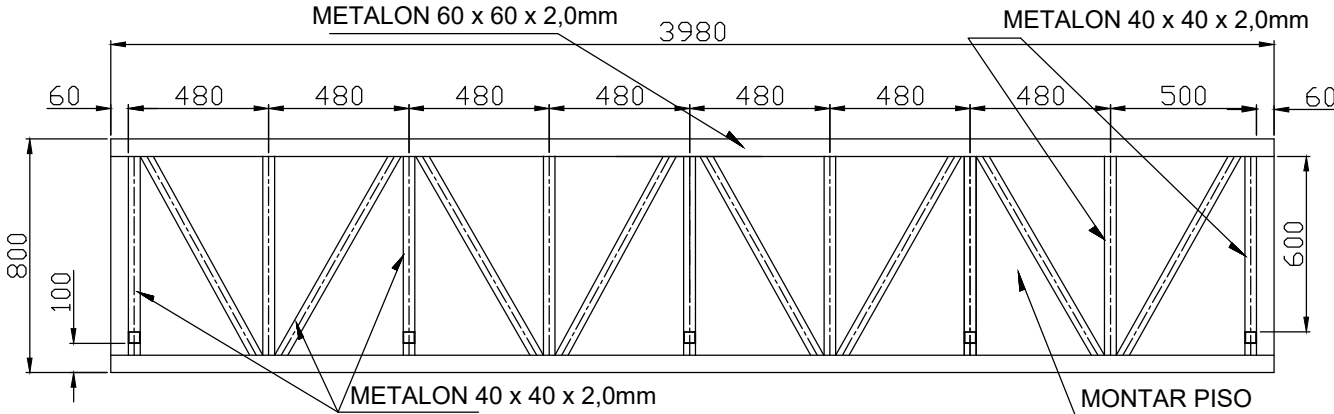


VISTA INFERIOR

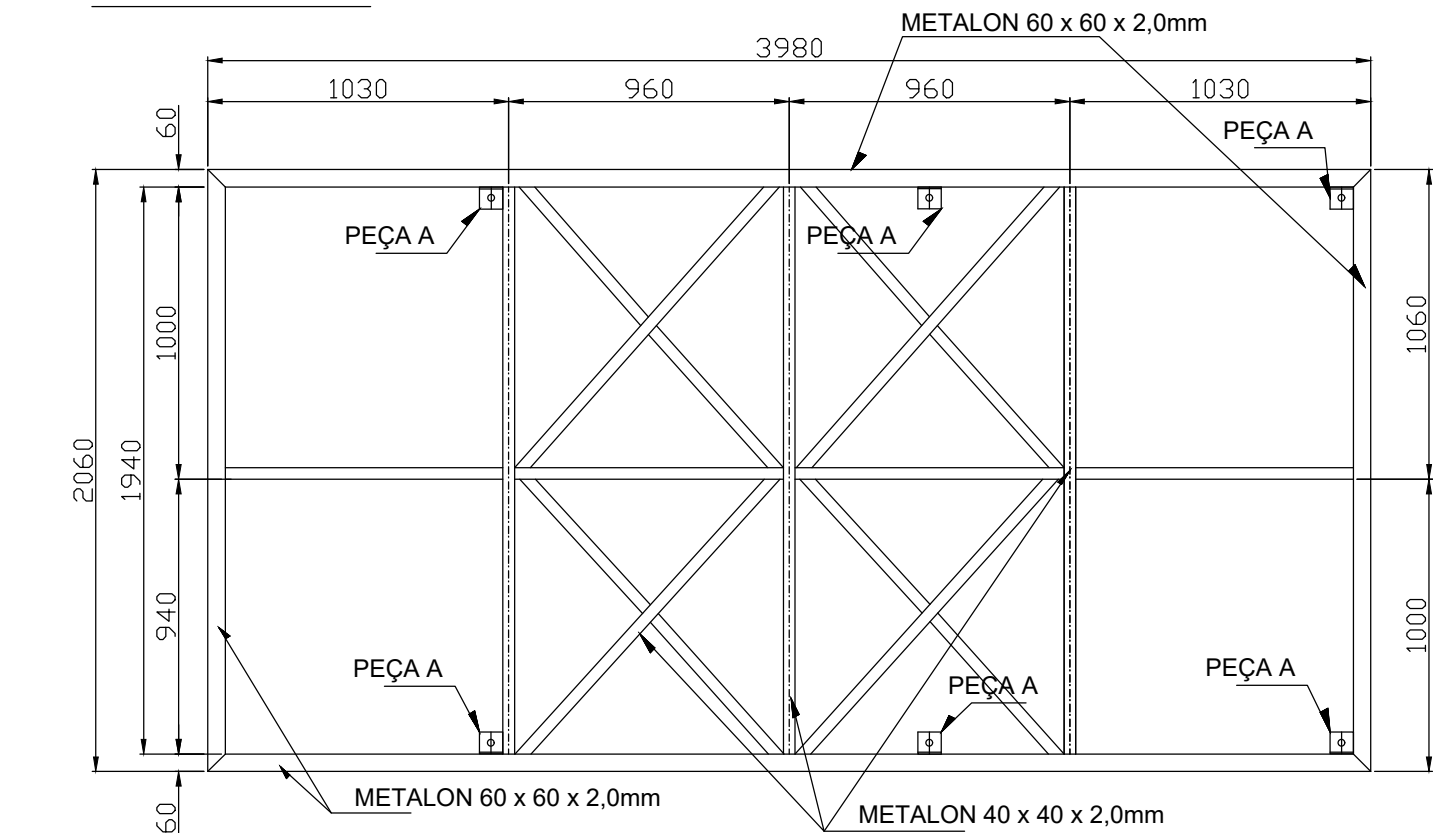

VISTA DO FUNDO

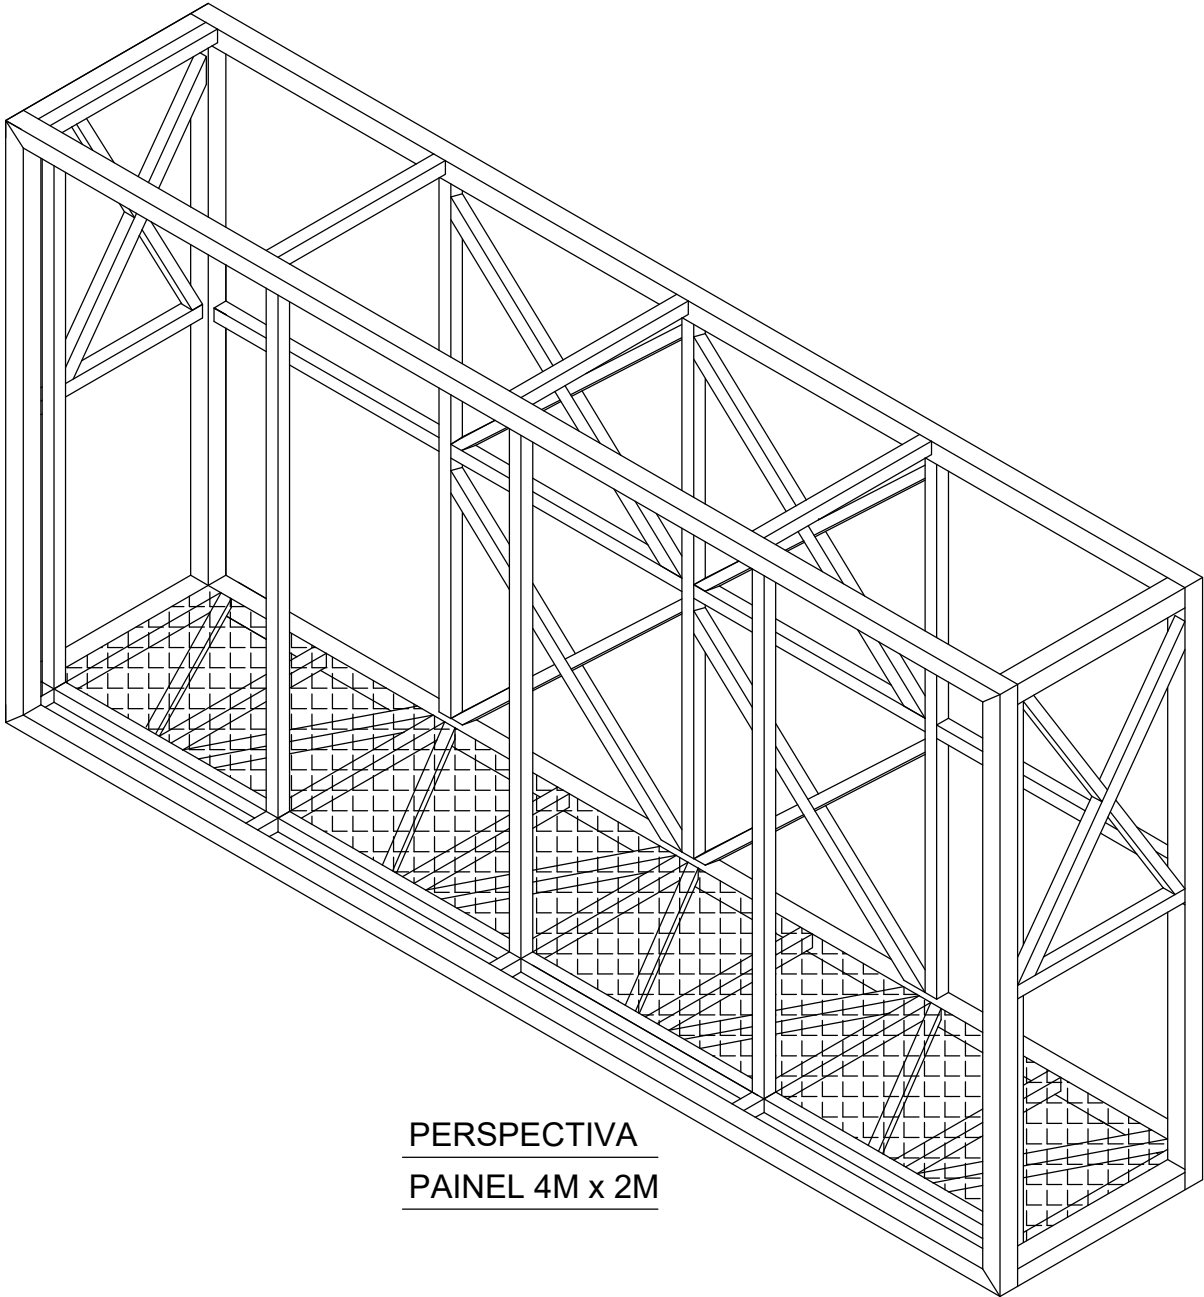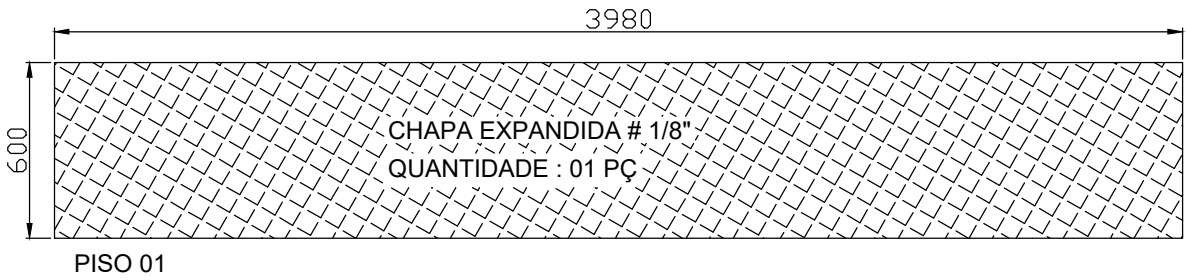

PERSPECTIVA
PAINEL 4M x 2M

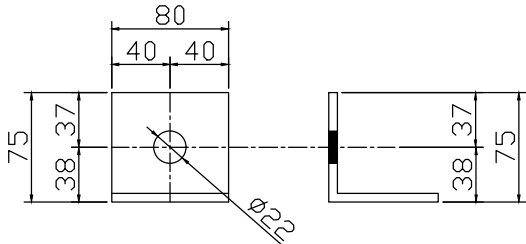

PEÇA A (FIXAÇÃO)
CANTONEIRA L 3"x # 1/4"
QUANTIDADE : 06 PÇS
OBS: localizar pontos de fixação,
e montar no fundo do painel.

LISTA DE MATERIAIS						
POS.	ESTRUTURA METÁLICA	DESCRİÇÃO	COMPR.	UNID.	QUANT.	PESO UNIT. PESO TOTAL
01	METALON 60x60x2,0mm		6000mm	PÇS	05	3,66 KG/M 109,80 KG
02	METALON 40x40x2,0mm		6000mm	PÇS	11	2,41 KG/M 159,06 KG
03	CHAPA EXPANDIDA # 1/8" x 600mm (PISO 01)		3980mm	PÇS	01	4,2 KG/M2 10,00 KG
04	CANTONEIRA L 3" x # 1/4"		80mm	PÇS	06	7,35 KG/M 3,52 KG
05						
06						
07						
08						
09						
10						
11						
PESO TOTAL GERAL :						282,38 KG

NOTAS: MEDIDAS EM MILIMETRO;

2				
1				
0	INICIAL	F.G.S		27/06/23
N°	DESCRİÇÃO	DES.	RESP.	DATA

LED EXPERT

PROJETO SOMENTE PARA ORÇAMENTO
NÃO UTILIZAR PARA FABRICAÇÃO

OBRA			Data:	Desenhista:	
PAINEL 4 x 2 GB RENTAL OUTDOOR			27-06-2023	FABIAN	
CONTÉM: PROJETO DE ESTRUTURA METÁLICA					
ESCALA	SE	R.T.:	Nº LED EXPERT:	FORMATO:	REVISÃO
IND.	--	--	127-2023-06-FL-01	A2	0