

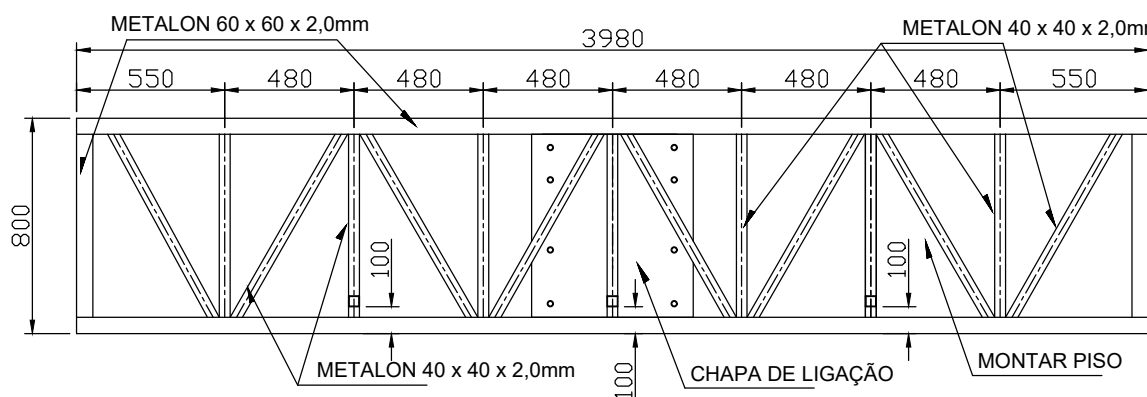
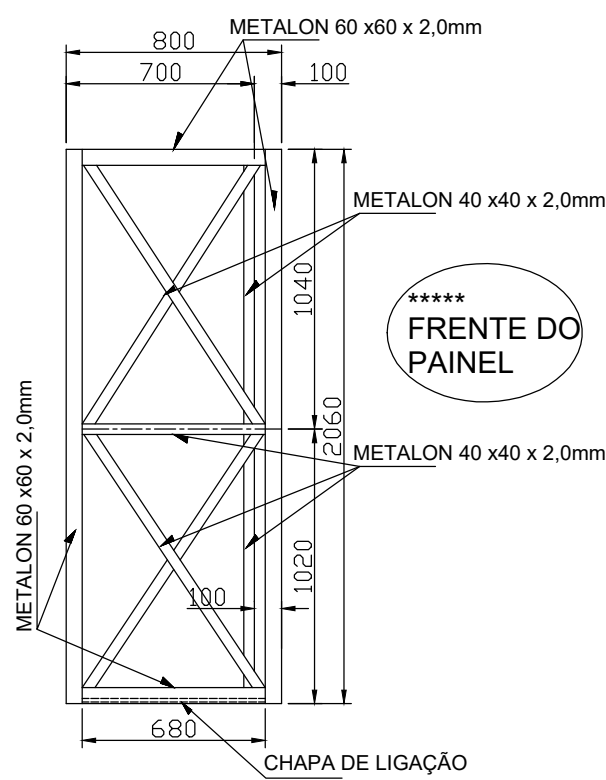
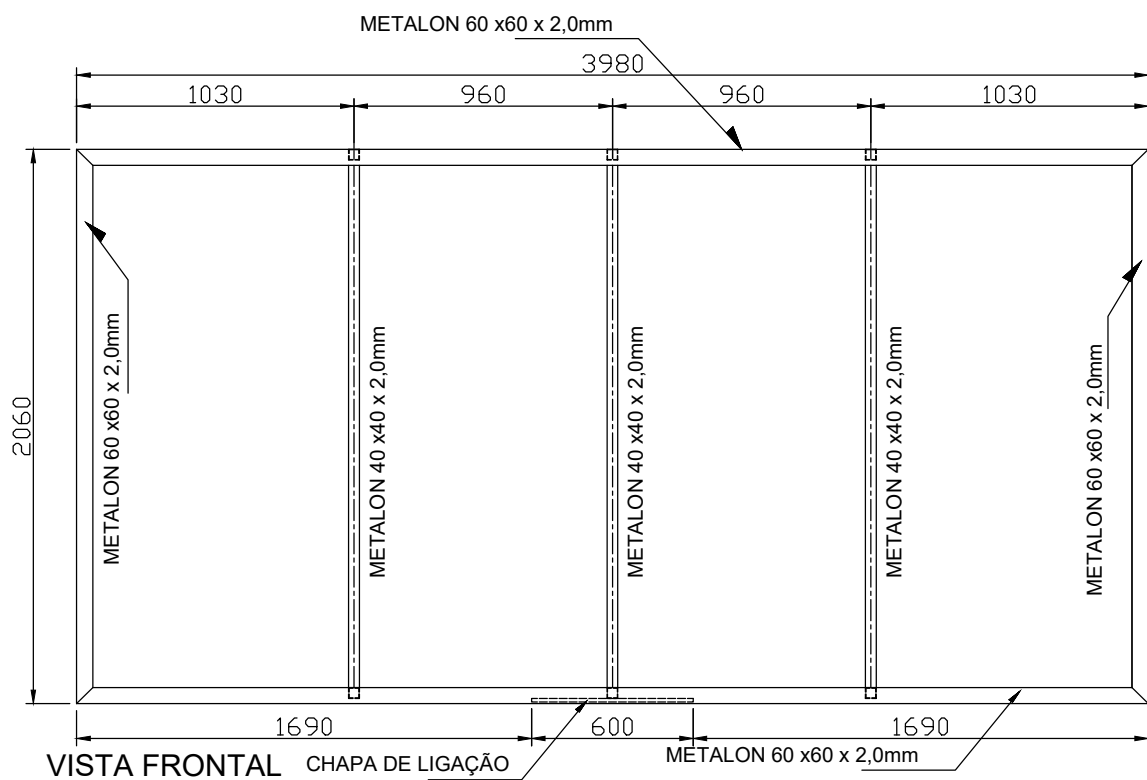
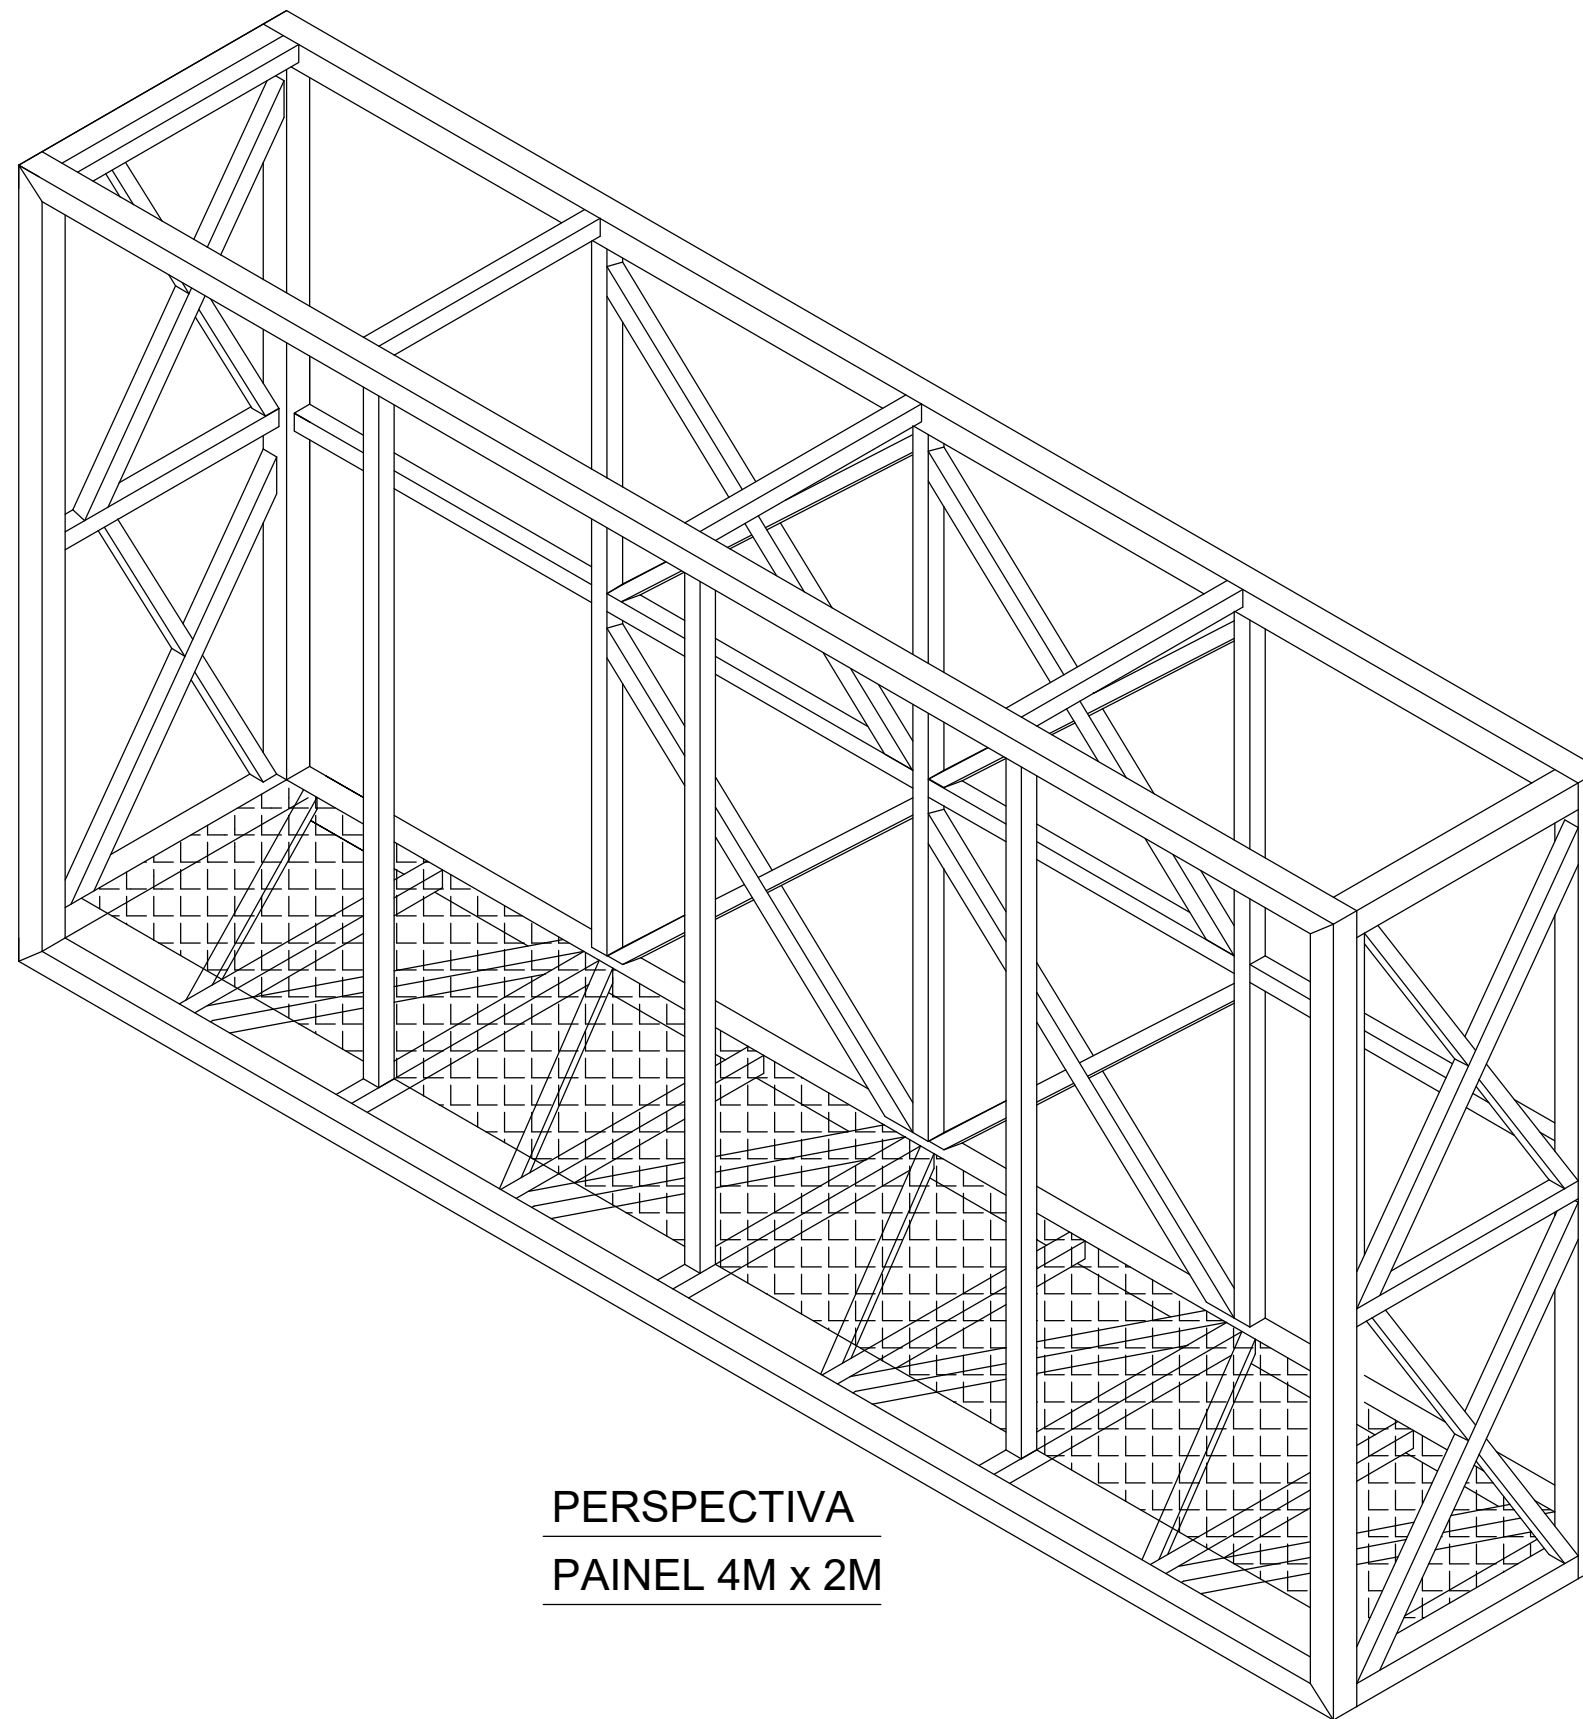
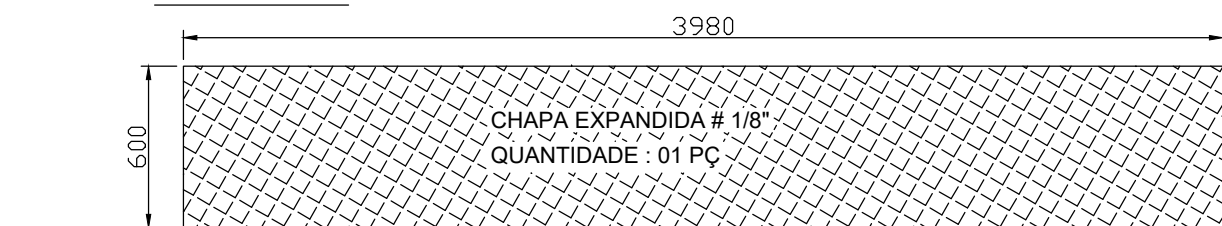


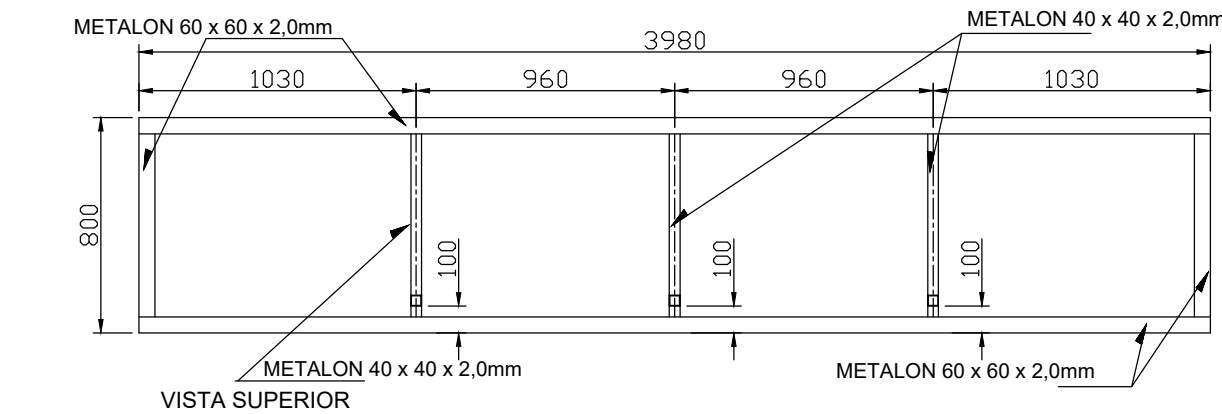

VISTA LATERAL

VISTA INFERIOR

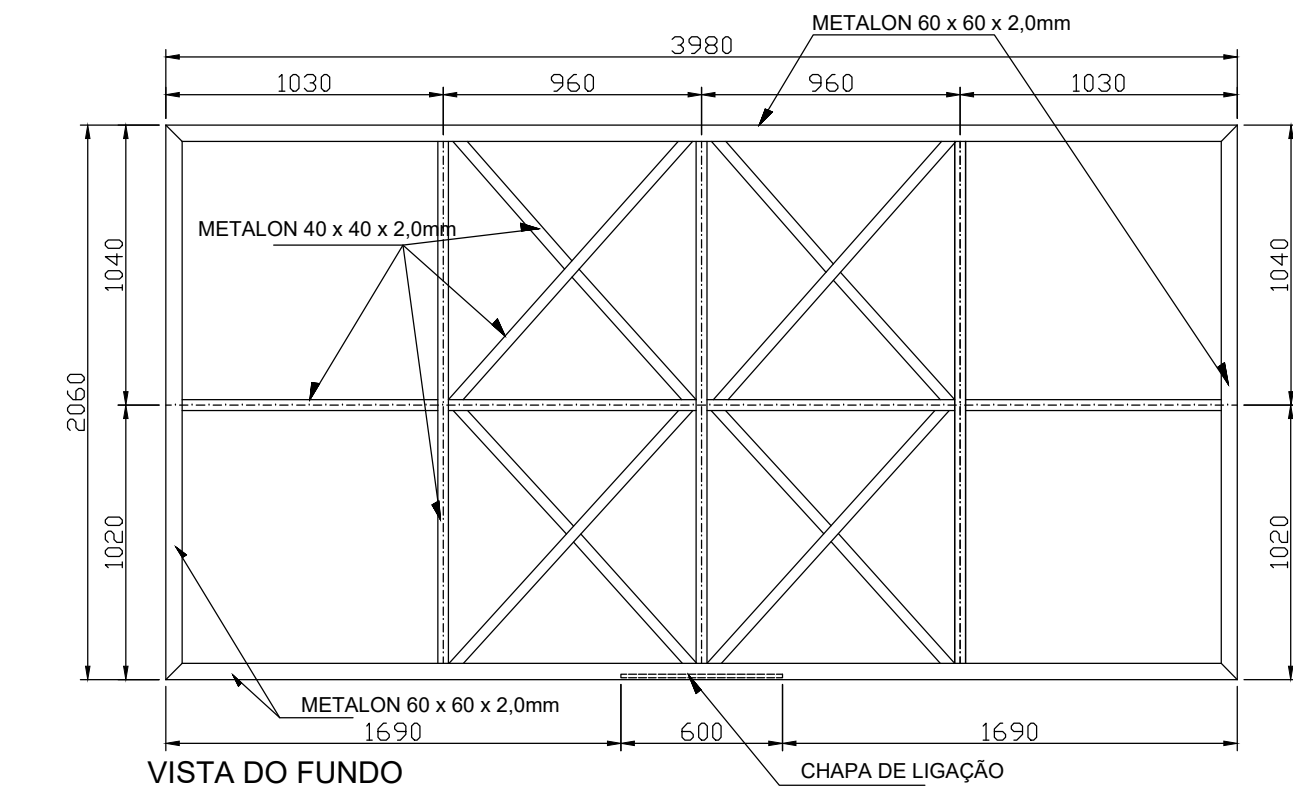

PERSPECTIVA
PAINEL 4M x 2M

NOTAS: MEDIDAS EM MILIMETRO; SEGUIR TODAS AS COTAS DO PROJETO.



4				
3				
2				
1				
0	INICIAL	F.G.S		13/11/23
N°	DESCRIÇÃO	DES.	RESP.	DATA

LED EXPERT


PROJETO SOMENTE PARA ORÇAMENTO
NÃO UTILIZAR PARA FABRICAÇÃO

OBRA			Data:	Desenhista:	
PAINEL 4 x 2 GB RENTAL OUTDOOR			13-11-2023	FABIAN	
CONTÉM:					
PROJETO DE ESTRUTURA METÁLICA – PILAR 3,0 METROS					
ESCALA	SE	R.T.:	Nº LED EXPERT:	FORMATO:	REVISÃO
IND.	--	--	222-2023-11-FL01	A2	00


LISTA DE MATERIAIS						
Cliente: KARLUS HEDUARDO				DATA: 13/11/2023		
Obra: PAINEL 4x2 GB RENTAL OUTDOOR POSTE 3,0 METROS						
ESTRUTURA METÁLICA						
POS.	DESCRIÇÃO	COMPR.	UNID.	QUANT.	PESO UNIT.	PESO TOTAL
01	METALON 60x60x2,0mm	6000mm	PÇS	05	3,66 KG/M	109,50 KG
02	METALON 40x40x2,0mm	6000mm	PÇS	11	2,41 KG/M	159,06 KG
03	CHAPA EXPANDIDA # 1/8" x 600mm (PISO)	3980mm	PÇS	01	4,2 KG/M2	10,02 KG
04	CHAPA BASE # 1" ø 680mm	ø 680mm	PÇS	01	196,00 KG/M2	71,14 KG
05	CHAPA DE LIGAÇÃO # 5/8" x 600mm	680mm	PÇS	02	125,44 KG/M2	102,00 KG
06	CHAPA # 3/8" x 140mm (PEÇA A)	250mm	PÇS	08	74,48 KG/M2	10,42 KG
07	CHAPA # 3/8" x 130mm (PEÇA B)	200mm	PÇS	08	74,48 KG/M2	7,74 KG
08	CHAPA # 3/16" x 1200mm (PILAR)	3000mm	PÇS	01	38,00 KG/M2	136,80 KG
09	CHAPA # 14 ø 680mm (GABARITO)	ø 680mm	PÇS	01	16,00 KG/M2	5,30 KG
10	BARRA ROSQUEADA ø 1" (CHUMBADORES)	1000mm	PÇS	08	3,98 KG/M	31,84 KG
11	CHAPA # 3/8" x 100mm (PEÇA 03)	100mm	PÇS	08	74,48 KG/M2	7,44 KG
12						
13						
PESO TOTAL GERAL :					651,26 KG	

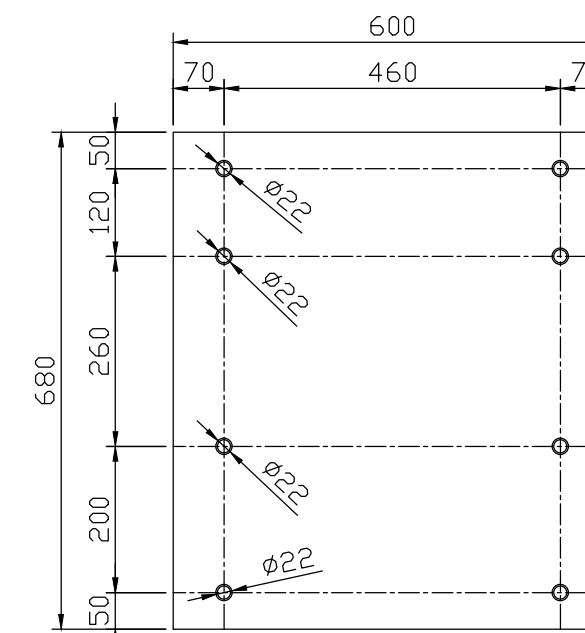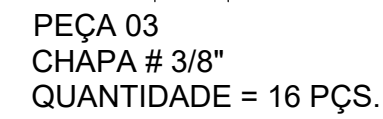


CHAPA DE LIGAÇÃO
CHAPA # 5/8"
QUANTIDADE: 04 PÇS

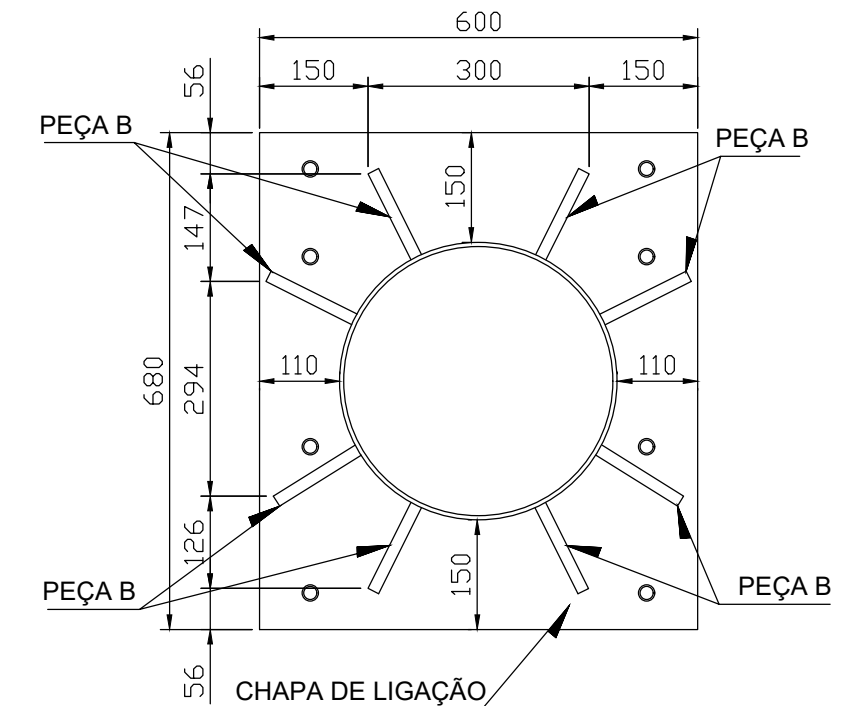


SEÇÃO BB

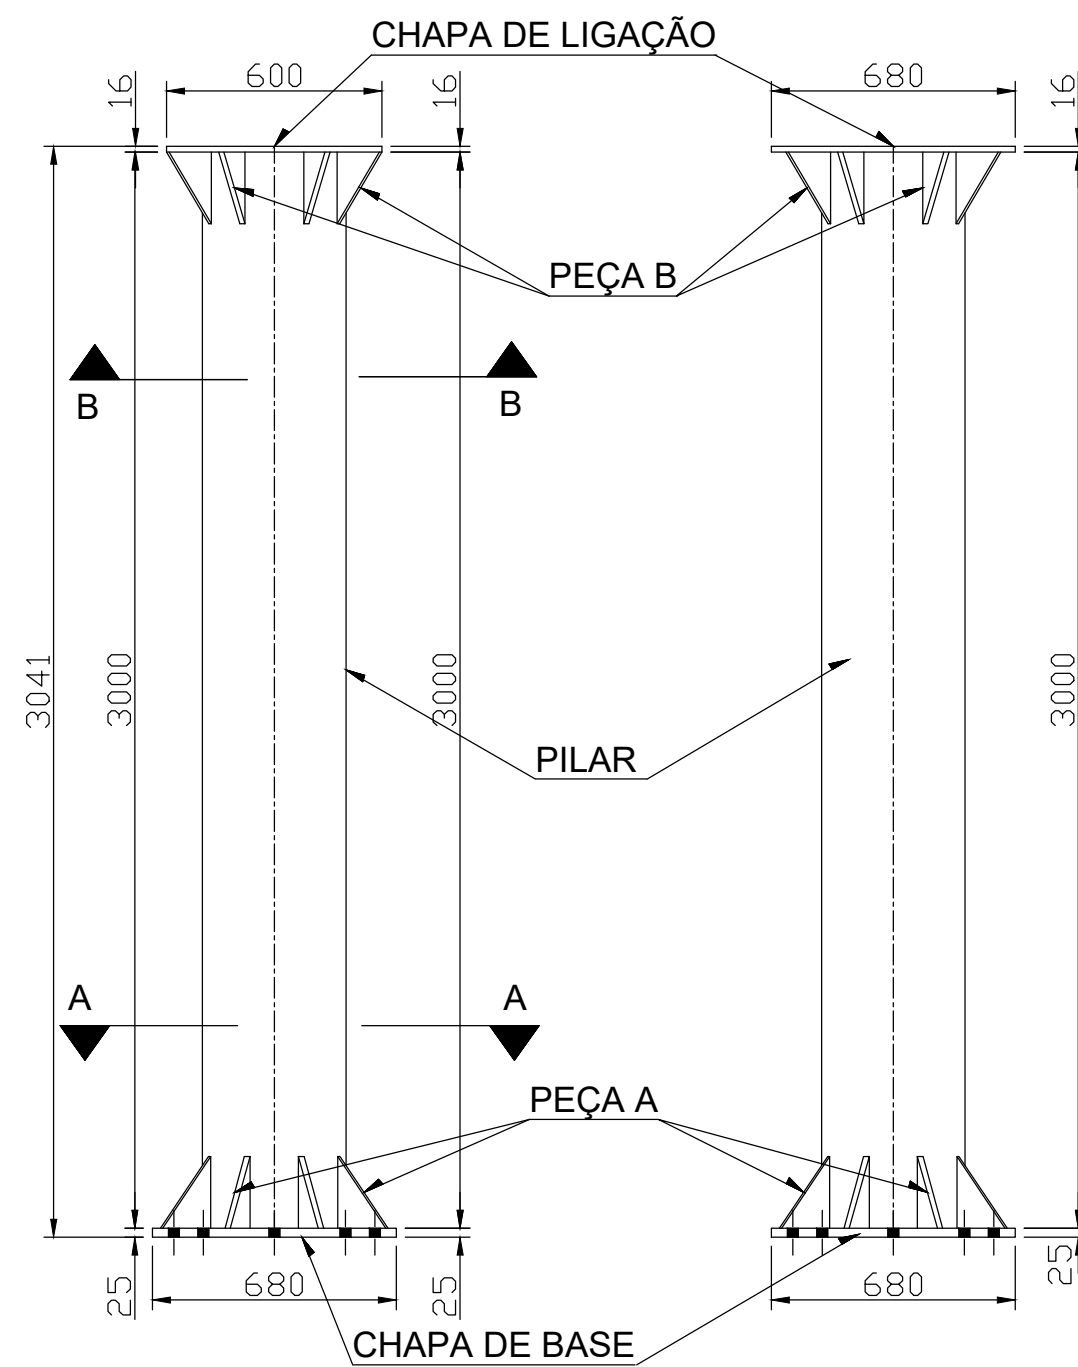


PILAR
VISTA DA FRENTE
QUANTIDADE: 01 PÇ

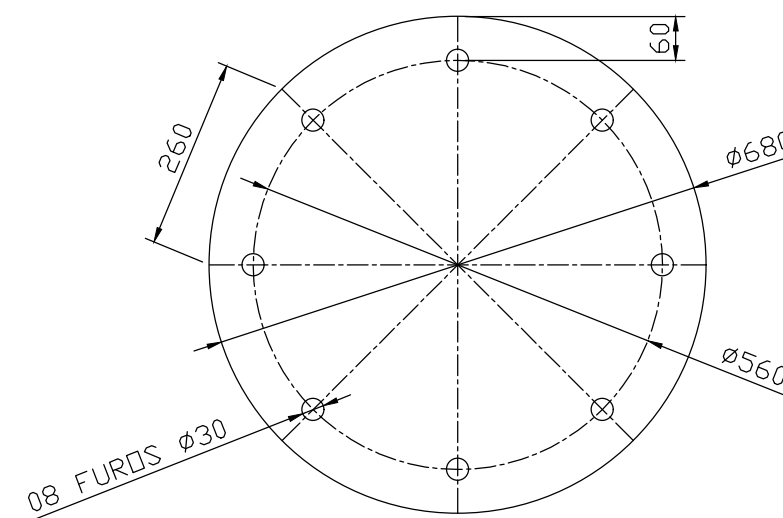




CHAPA DE BASE
CHAPA # 1"
QUANTIDADE: 02 PÇS

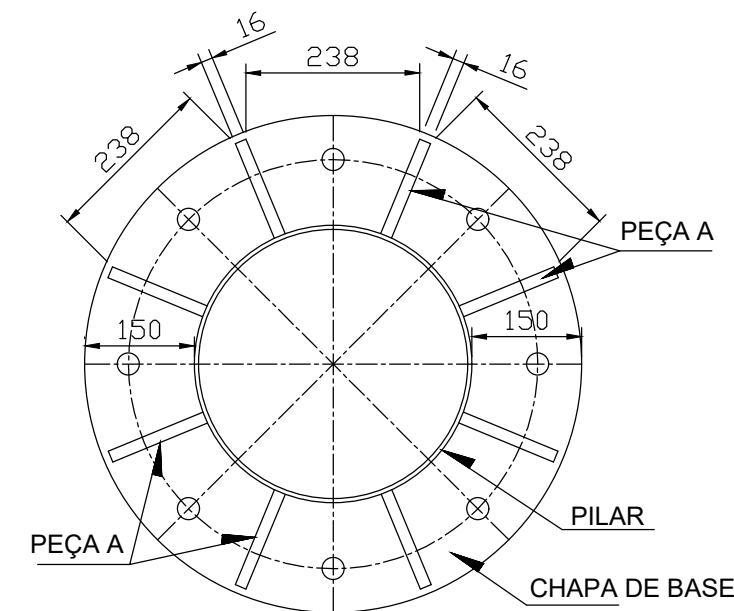


SEÇÃO AA

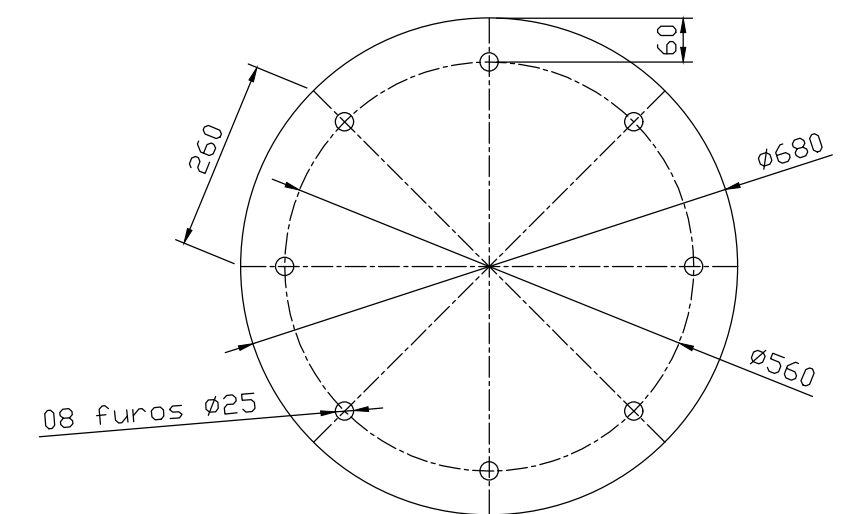

CHAPA GABARITO
CHAPA # 14"
QUANTIDADE: 02 PÇS

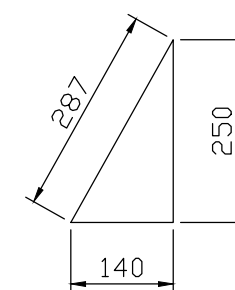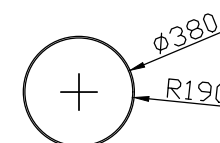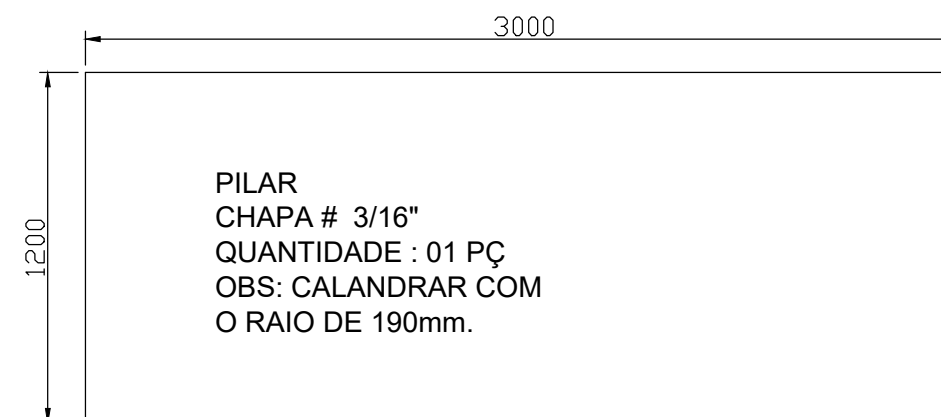

PEÇA A
CHAPA # 3/8"
QUANTIDADE : 16 PÇS

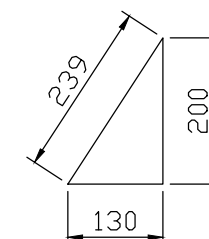

PEÇA B
CHAPA # 3/8"
QUANTIDADE : 16 PÇS

NOTAS: MEDIDAS EM MILIMETRO;

4				
3				
2				
1				
0	INICIAL	F.G.S		13/11/23
N°	DESCRIÇÃO	DES.	RESP.	DATA

LED EXPERT

PROJETO SOMENTE PARA ORÇAMENTO
NÃO UTILIZAR PARA FABRICAÇÃO

OBRA PAINEL 4 x 2 GB RENTAL OUTDOOR			Data: 13-11-2023	Desenhista: FABIAN	
CONTÉM: PROJETO DE ESTRUTURA METÁLICA – PILAR 3,0 METROS					
ESCALA	SE	R.T.:	Nº LED EXPERT:	FORMATO:	REVISÃO
IND.	--	--	222-2023-11-FL02	A2	00