




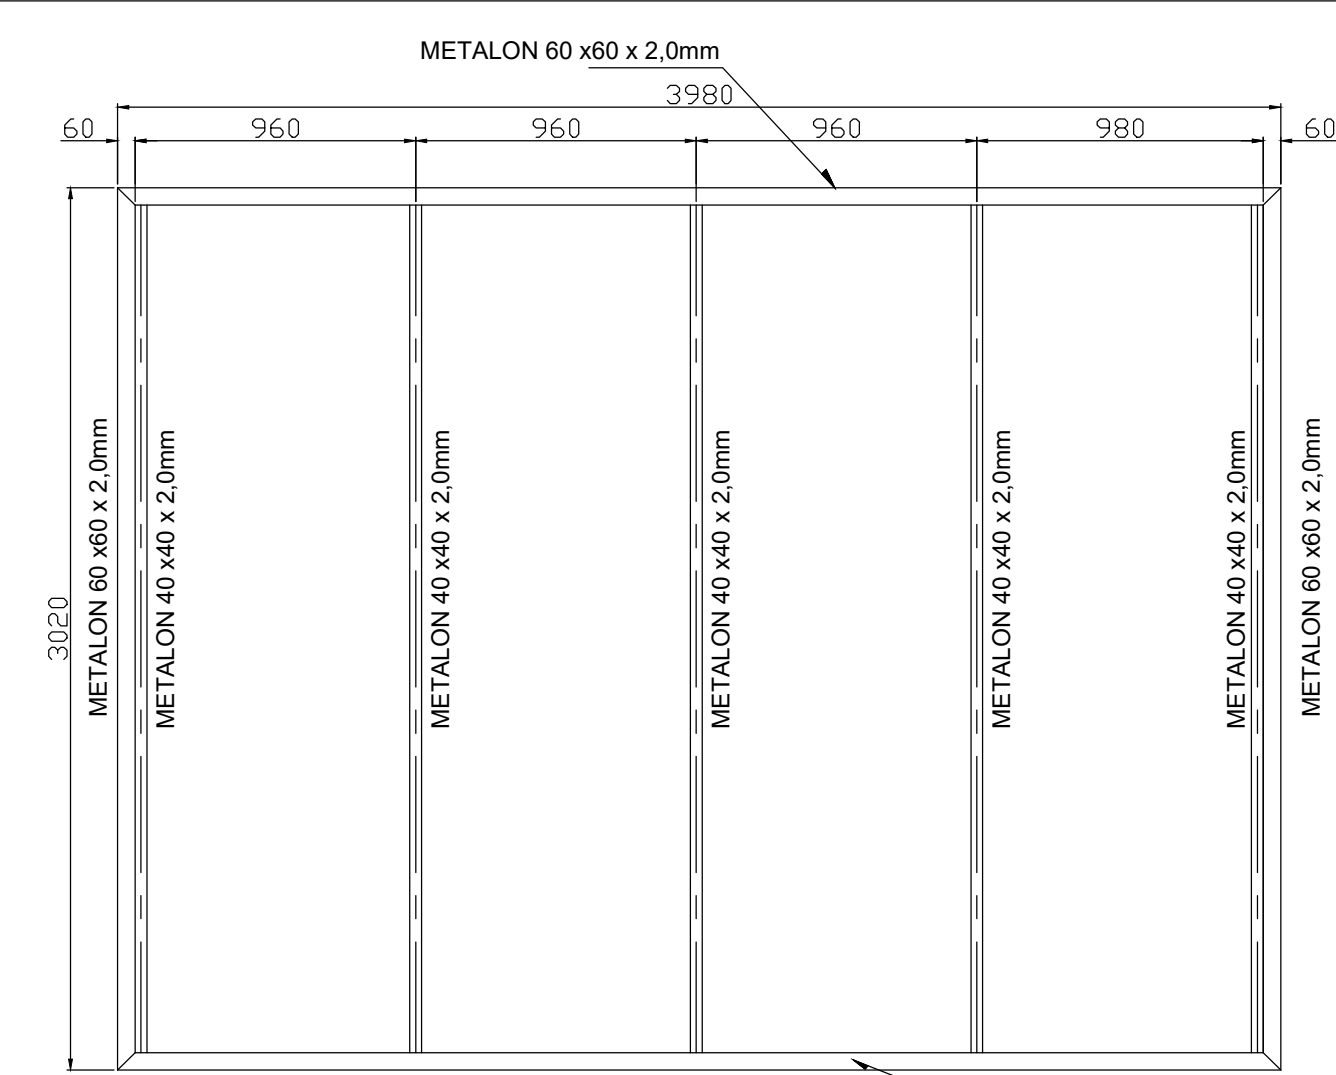


VISTA FRONTAL

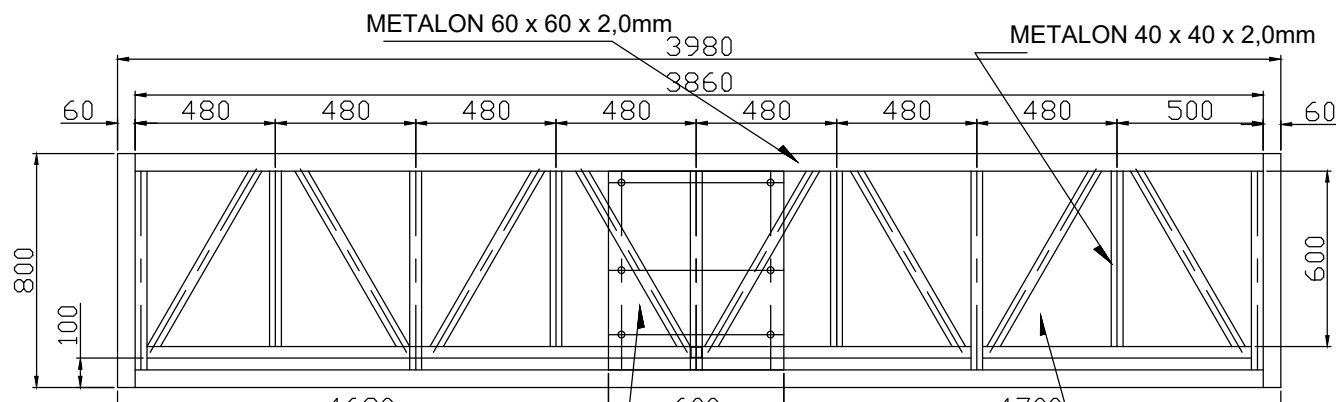


VISTA INFERIOR

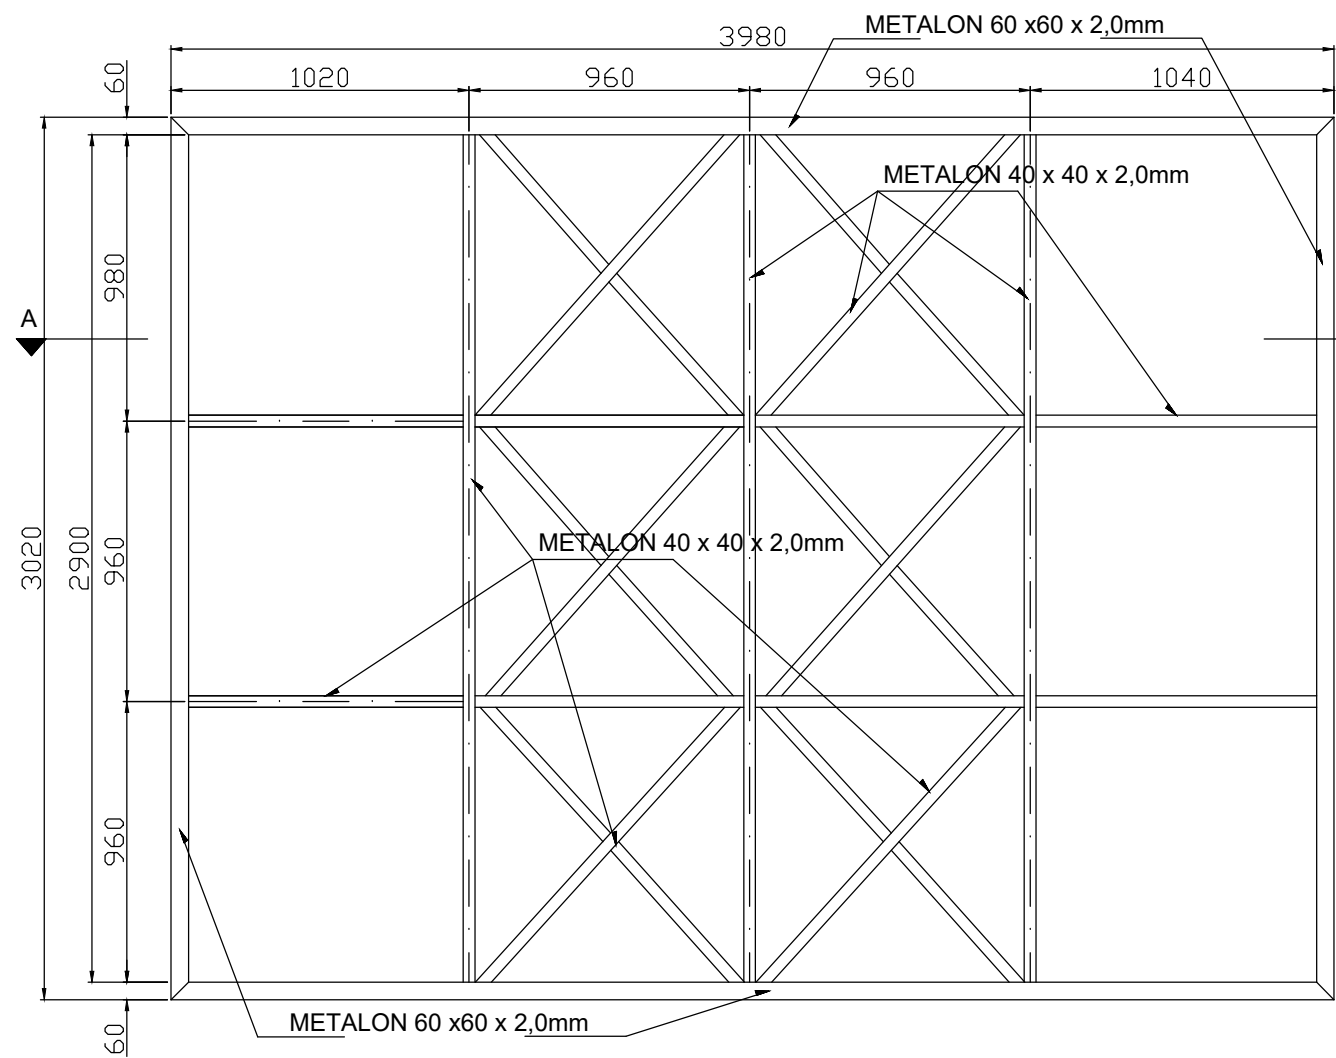




VISTA DO FUNDO

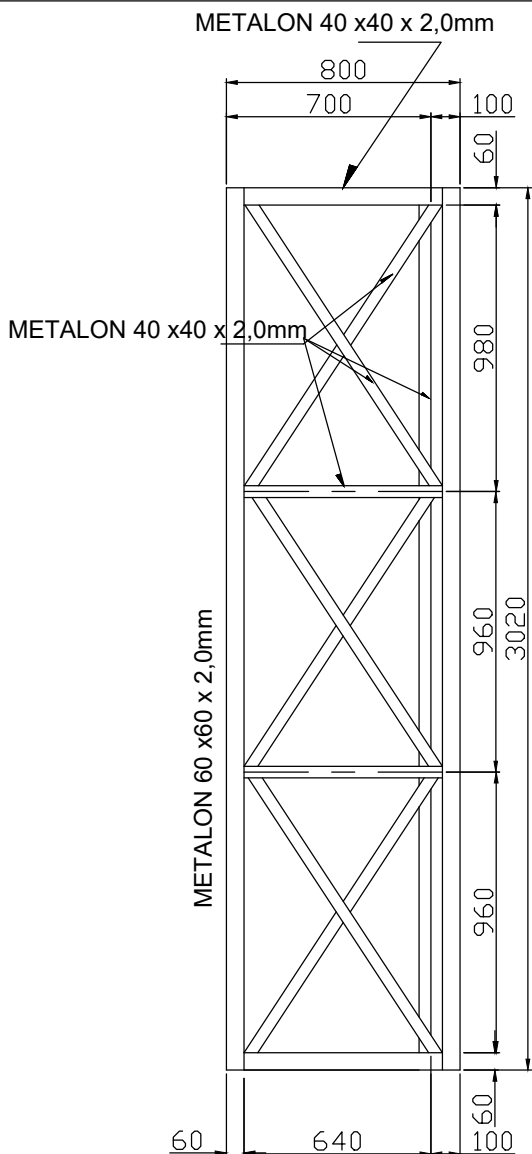


VISTA LATERAL

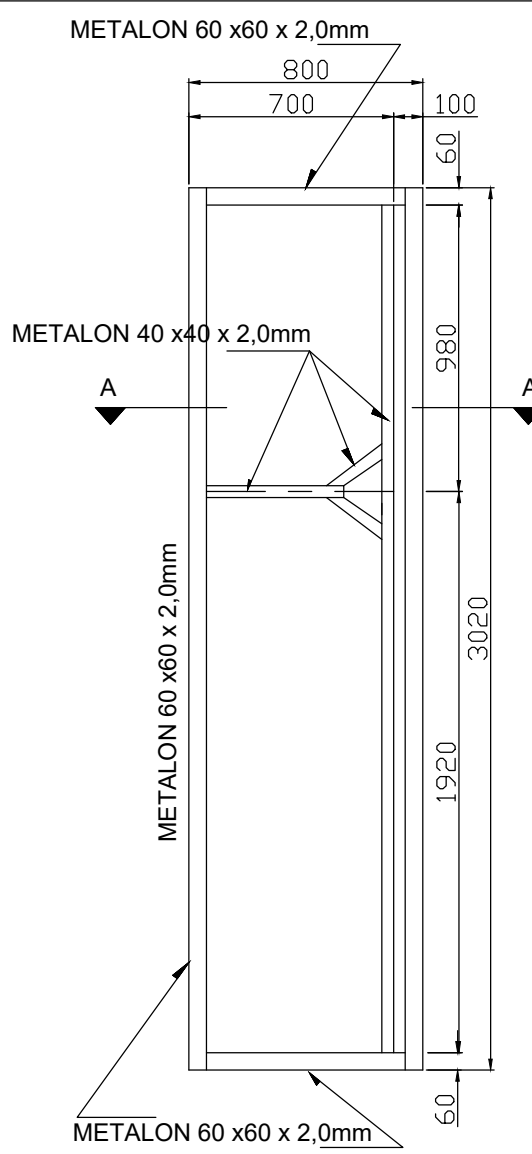

PLATAFORMA
SECUNDÁRIA

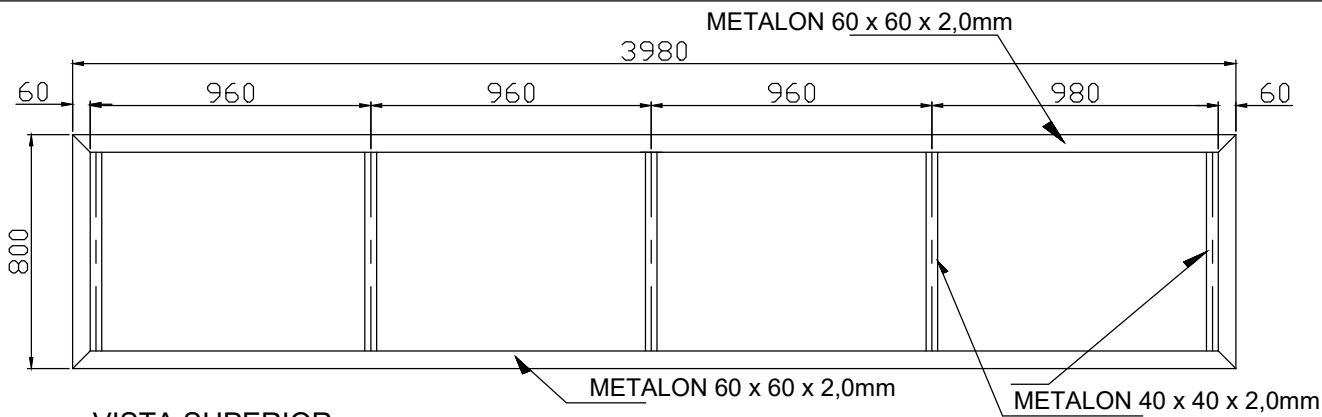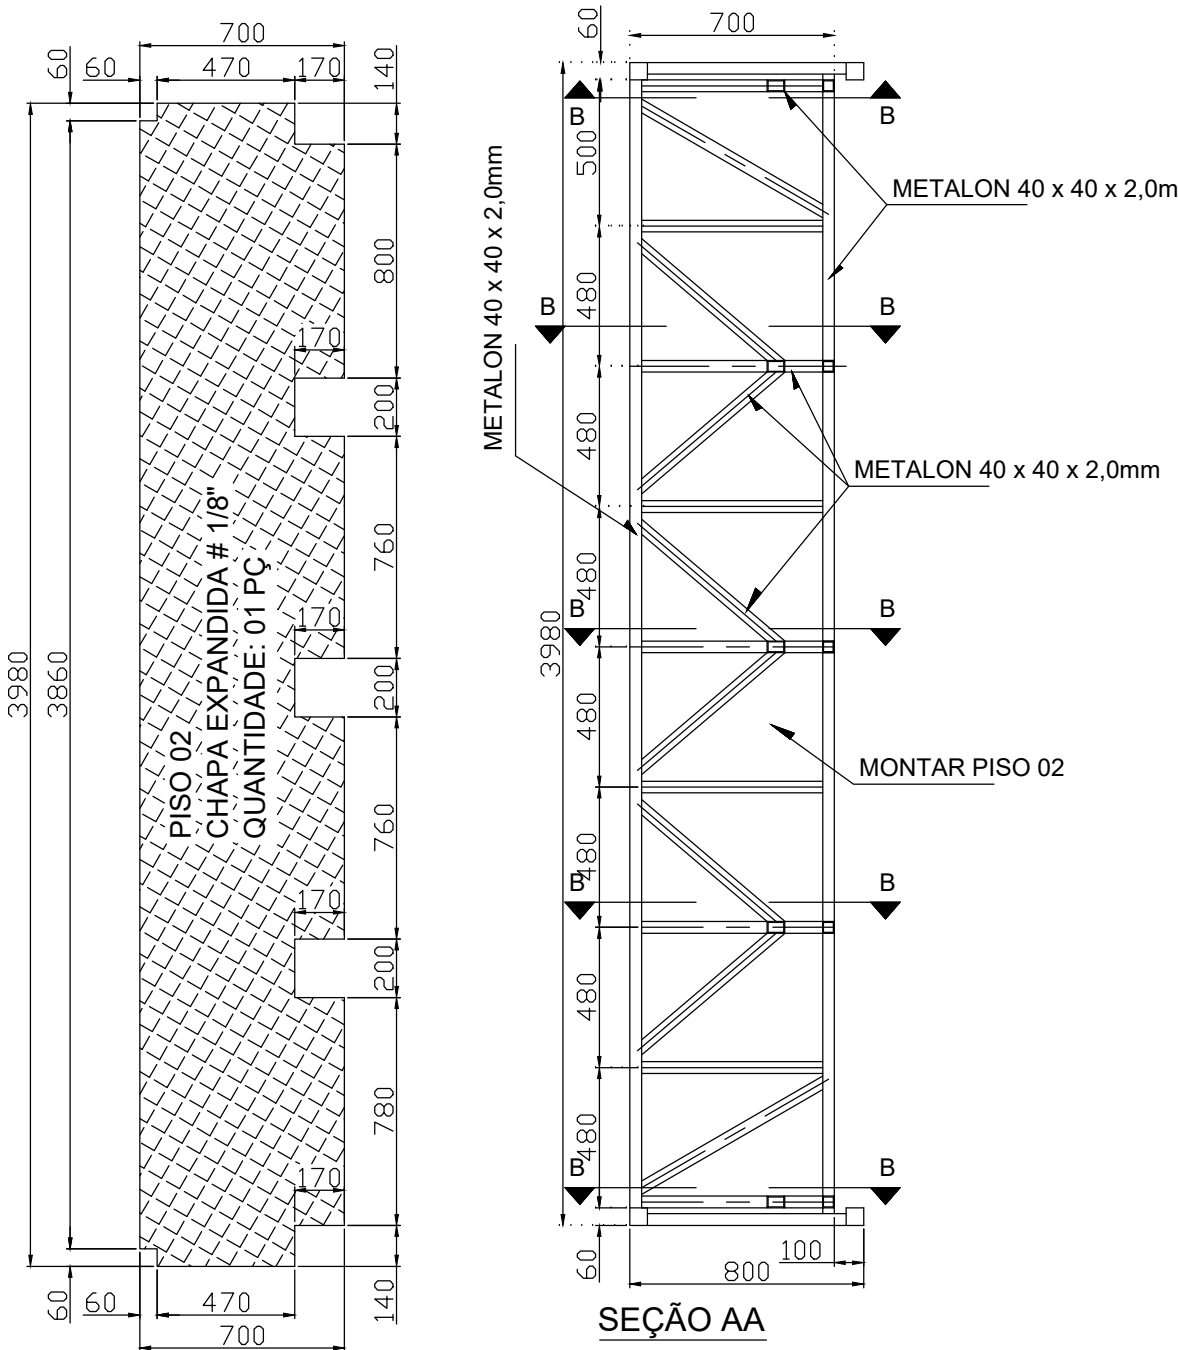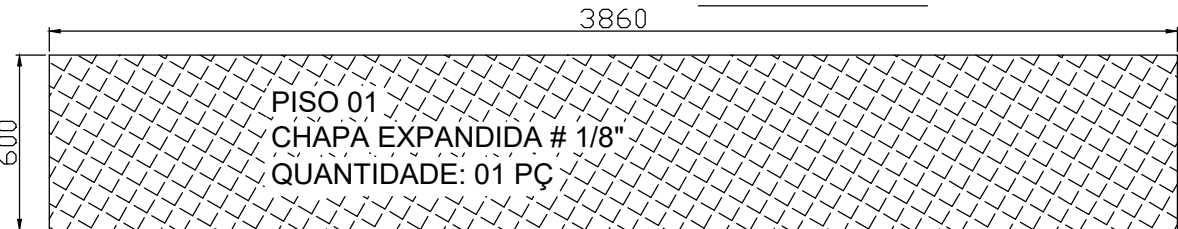

VISTA SUPERIOR

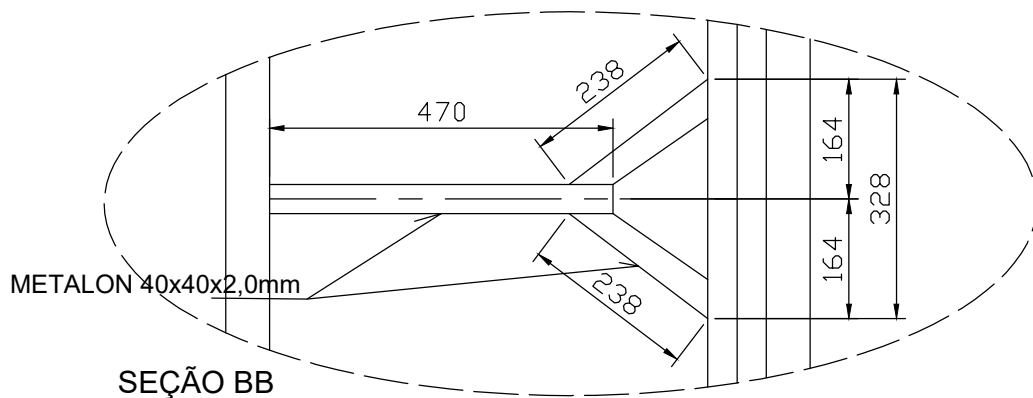

SEÇÃO BB

LISTA DE MATERIAIS						
Cliente: JORDY				DATA: 10/02/2023		
Obra: PAINEL 4x3 GB RENTAL OUTDOOR						
	ESTRUTURA METÁLICA					
	DESCRIÇÃO	COMPR.	UNID.	QUANT.	PESO UNIT.	PESO TOTAL.
01	METALON 60x60x2,0mm	6000mm	PÇS	06	3,61 KG/M	129,96 KG
02	METALON 40x40x2,0mm	6000mm	PÇS	17	2,41 KG/M	245,82 KG
03	CHAPA BASE # 1" x ø 680mm	/////	PÇS	01	196,00 KG/M2	90,00 KG
04	CHAPA DE LIGAÇÃO # 5/8" x 600mm	680mm	PÇS	02	125,44 KG/M2	102,00 KG
05	CHAPA # 5/8" x 140mm NERVURA A	250mm	PÇS	08	125,50 KG/M2	35,00 KG
06	CHAPA # 5/8" x 130mm NERVURA B	200mm	PÇS	08	125,50 KG/M2	26,00 KG
07	CHAPA PILAR # 1/4" x 1200mm	2000mm	PÇS	02	49,39 KG/M2	237,00 KG
08	CHAPA PILAR # 1/4" x 1200mm	1500mm	PÇS	01	49,39 KG/M2	88,90 KG
09	CHAPA EXPANDIDA # 1/8" x 600mm (PISO 01)	3860mm	PÇS	01	4,2 KG/M2	9,72 KG
10	CHAPA EXPANDIDA # 1/8" x 700mm (PISO 02)	3980mm	PÇS	01	4,2 KG/M2	11,70 KG
11	CHAPA # 14 x 680mm (GABARITO)	680mm	PÇS	01	16,00 KG/M2	7,40 KG
12	BARRA ROSQUEADA ø 1"	1000mm	PÇS	08	3,98 KG/M	31,84 KG
13	CHAPA # 3/8" x 100mm (PEÇA 03)	100mm	PÇS	08	74,48 KG/M2	6,00 KG
14	FERRO REDONDO ø 5/8"	950mm	PÇS	10	1,56 KG/M	14,80 KG
PESO TOTAL GERAL :					1.036,14 KG	


NOTAS: MEDIDAS EM MILIMETRO;

4				
3				
2				
1				
0	INICIAL	F.G.S		10/02/23
N°	DESCRIÇÃO	DES.	RESP.	DATA

LED EXPERT

PROJETO SOMENTE PARA ORÇAMENTO
NÃO UTILIZAR PARA FABRICAÇÃO


OBRA			Data:		Desenhista:	
PAINEL 4 x 3 OUTDOOR GB RENTAL			10-02-2023		FABIAN	
CONTÊM:						
PROJETO DE ESTRUTURA METÁLICA						
ESCALA	SE	R.T.:	N° LED EXPERT:		FORMATO:	REVISÃO
IND.	--	--	85-2023-02-FL-01		A2	00

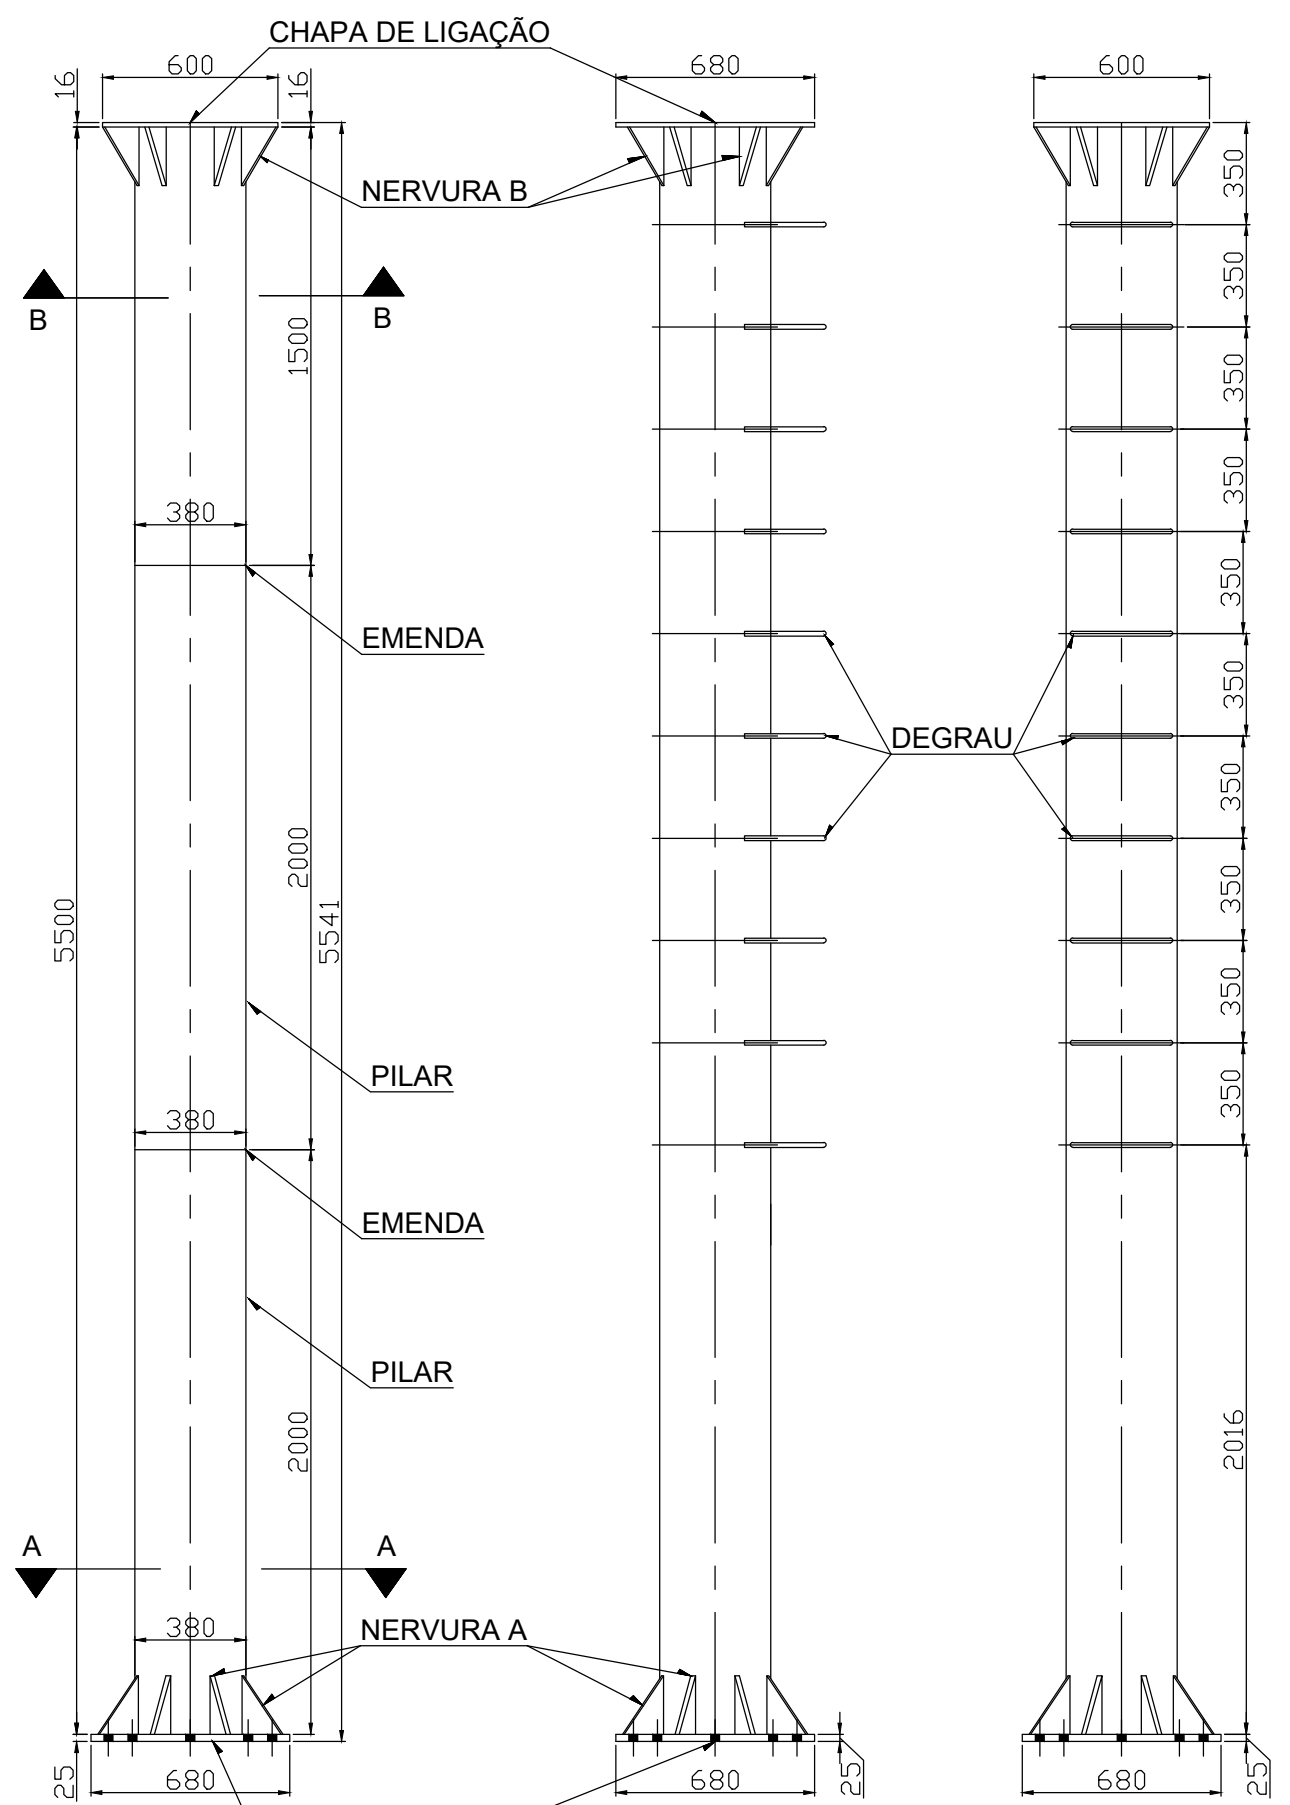


PILAR
VISTA DA FRENTE
QUANTIDADE: 01 PÇ

PILAR
VISTA LATERAL


ESCALA DO PILAR
VISTA DO FUNDO

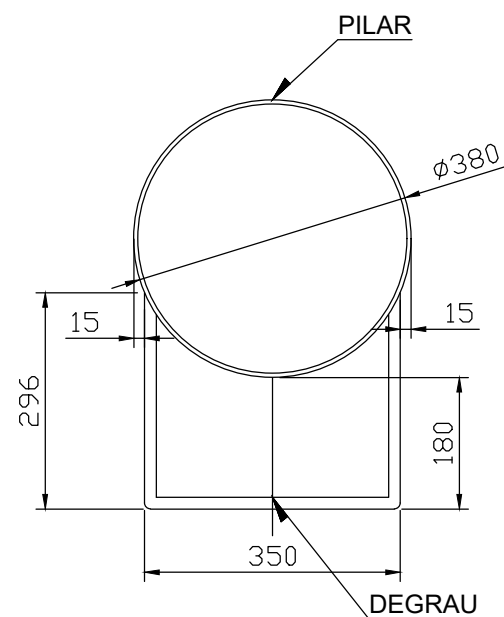


CORTE DO PILAR

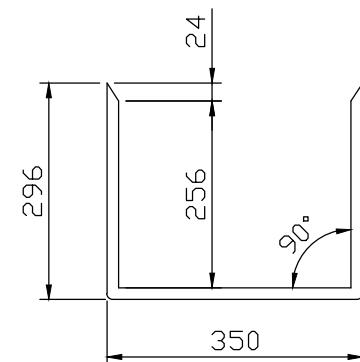


DEGRAU
FERRO REDONDO Ø 5/8"
QUANTIDADE: 10 PÇS

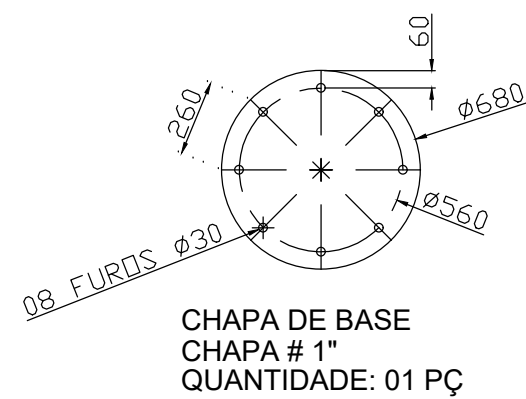


CHAPA DE BASE
CHAPA # 1"
QUANTIDADE: 01 PÇ

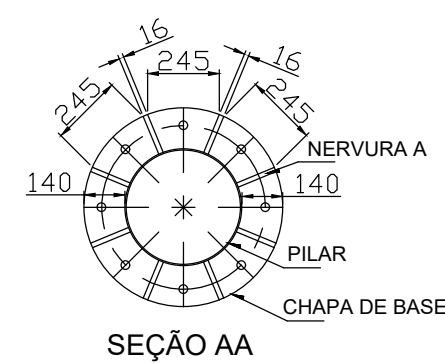


SEÇÃO AA

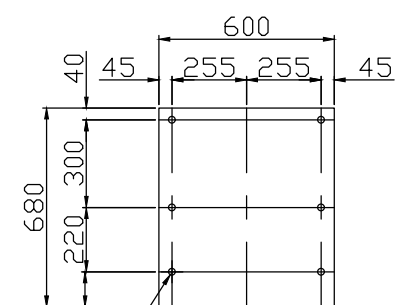


CHAPA DE LIGAÇÃO
CHAPA # 5/8"
QUANTIDADE: 02 PÇ

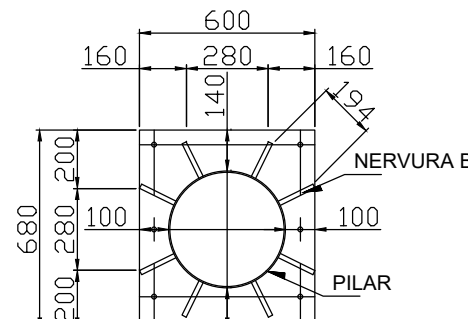


SEÇÃO BB

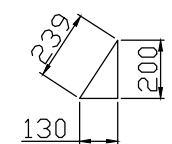


NERVURA B
CHAPA # 5/8"
QUANTIDADE : 08 PÇS

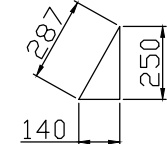


NERVURA A
CHAPA # 5/8"
QUANTIDADE : 08 PÇS

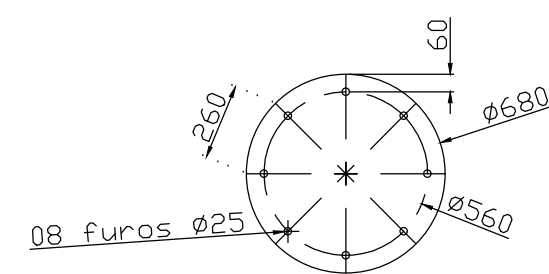


CHAPA GABARITO
CHAPA # 1/8"
QUANTIDADE: 01 PÇ

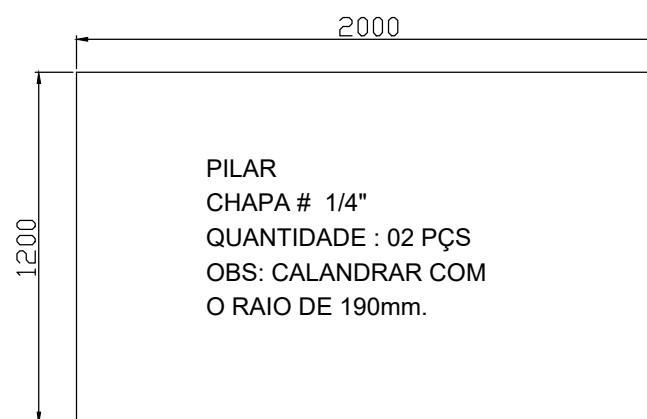


PILAR
CHAPA # 1/4"
QUANTIDADE : 02 PÇS
OBS: CALANDRAR COM
O RAIOS DE 190mm.

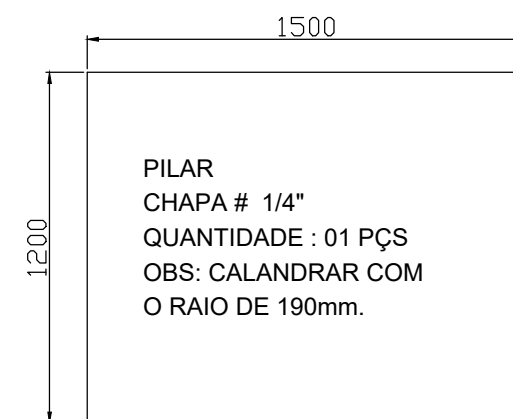


PILAR
CHAPA # 1/4"
QUANTIDADE : 01 PÇS
OBS: CALANDRAR COM
O RAIOS DE 190mm.

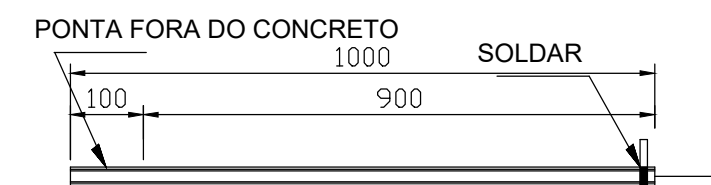

CHUMBADORES
BARRA ROSQUEADA Ø 1"
QUANTIDADE = 08 PÇS.

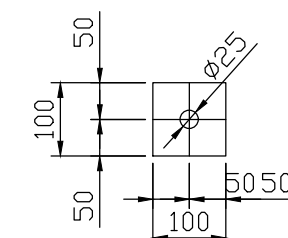

PEÇA 03
CHAPA # 3/8"
QUANTIDADE = 08 PÇS.

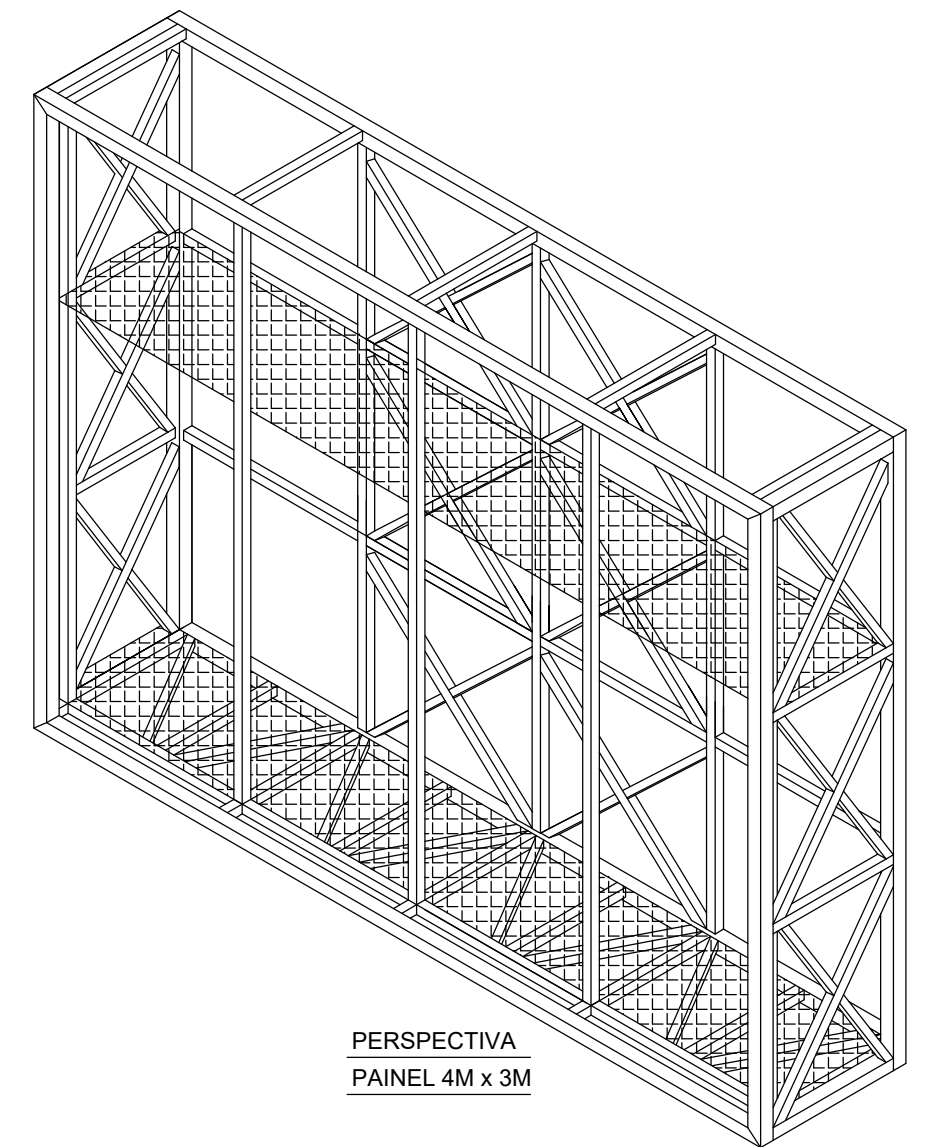

PERSPECTIVA
PAINEL 4M x 3M

NOTAS: MEDIDAS EM MILIMETRO;

4				
3				
2				
1				
0	INICIAL	F.G.S		10/02/23
N°	DESCRIÇÃO	DES.	RESP.	DATA

LED EXPERT

PROJETO SOMENTE PARA ORÇAMENTO
NÃO UTILIZAR PARA FABRICAÇÃO

OBRA PAINEL 4 x 3 OUTDOOR GB RENTAL			Data: 10-02-2023	Desenhista: FABIAN	
CONTÉM: PROJETO DE ESTRUTURA METÁLICA – PILAR; PERSPECTIVA					
ESCALA IND.	SE --	R.T.: --	N° LED EXPERT: 85-2023-02-FL-02	FORMATO: A2	REVISÃO 00