



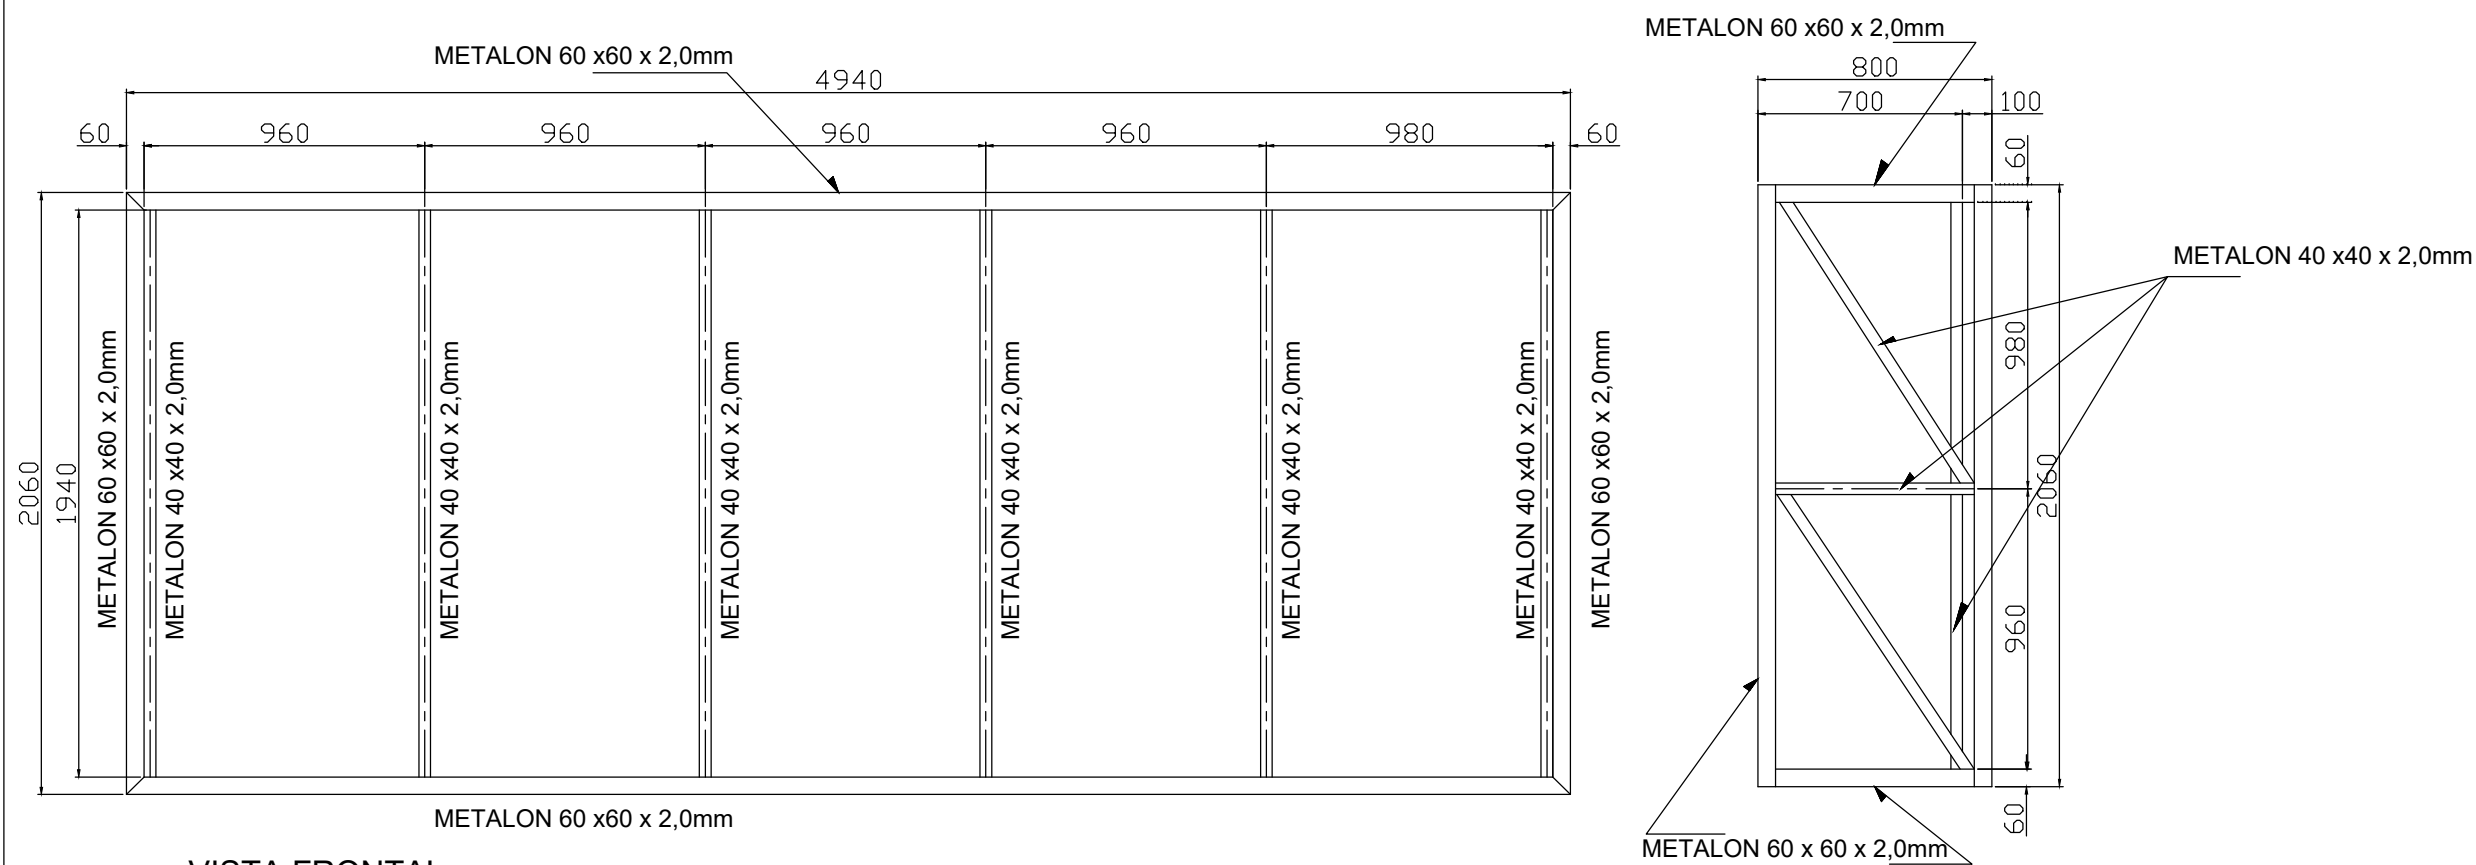


VISTA FRONTAL


VISTA LATERAL

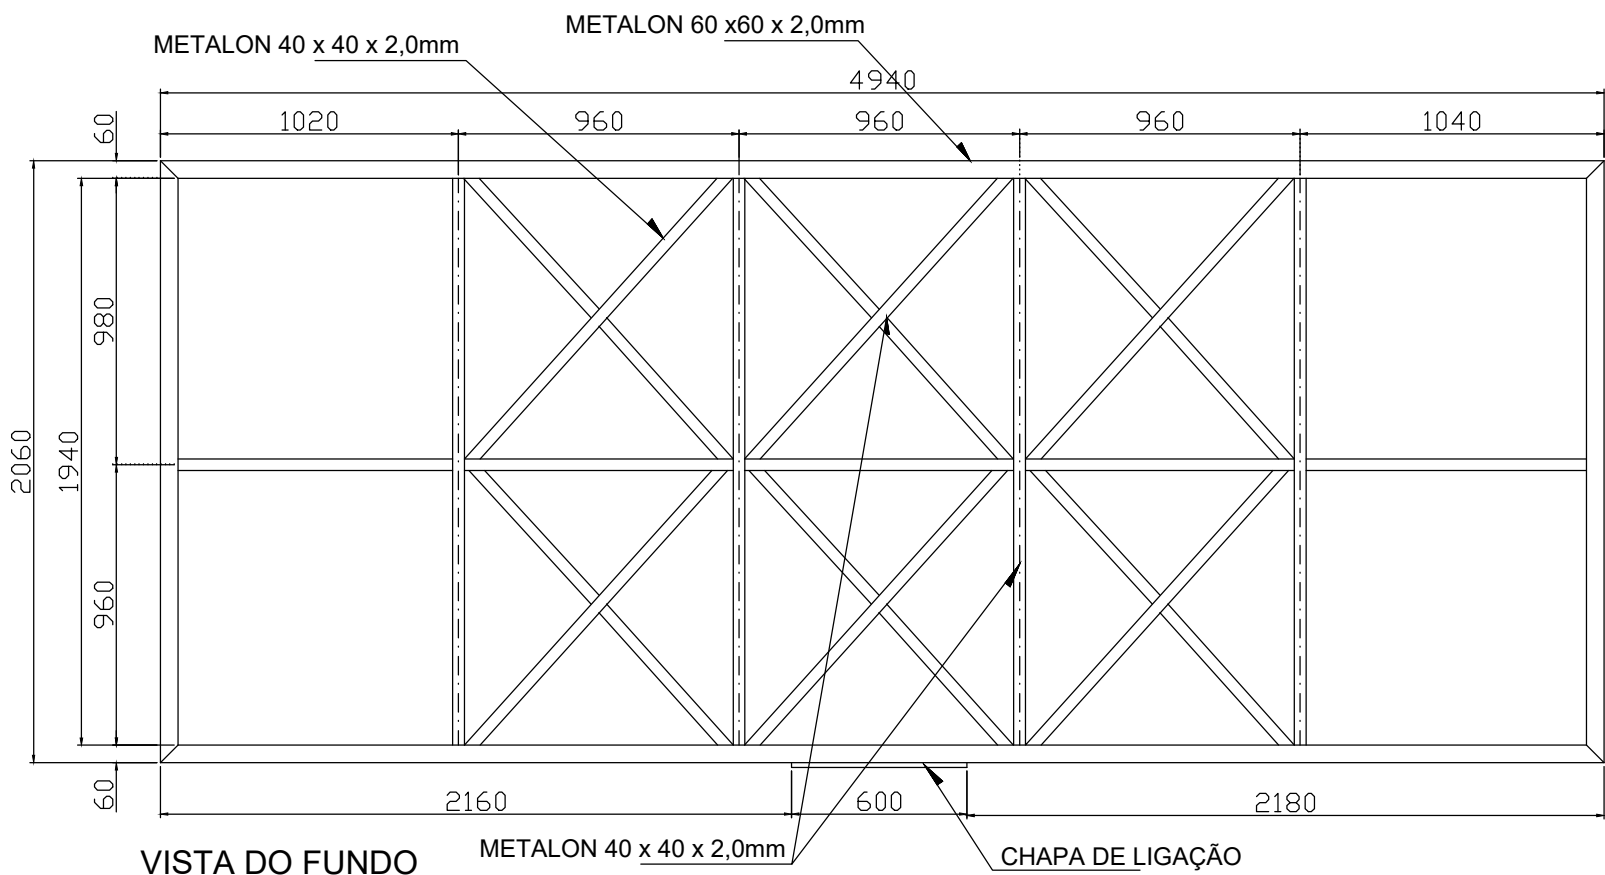


VISTA DO FUNDO

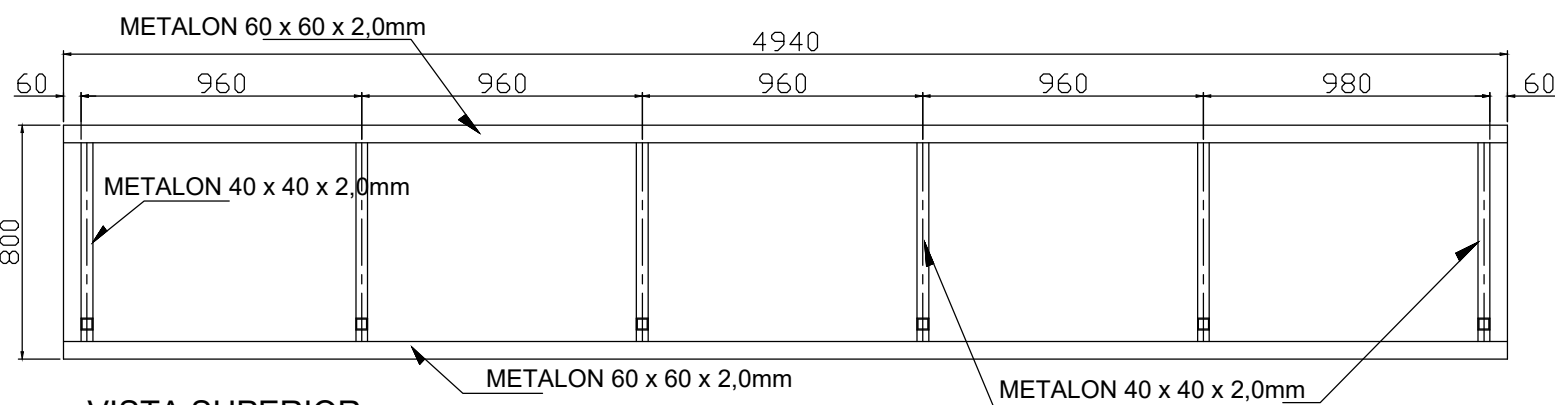

VISTA SUPERIOR

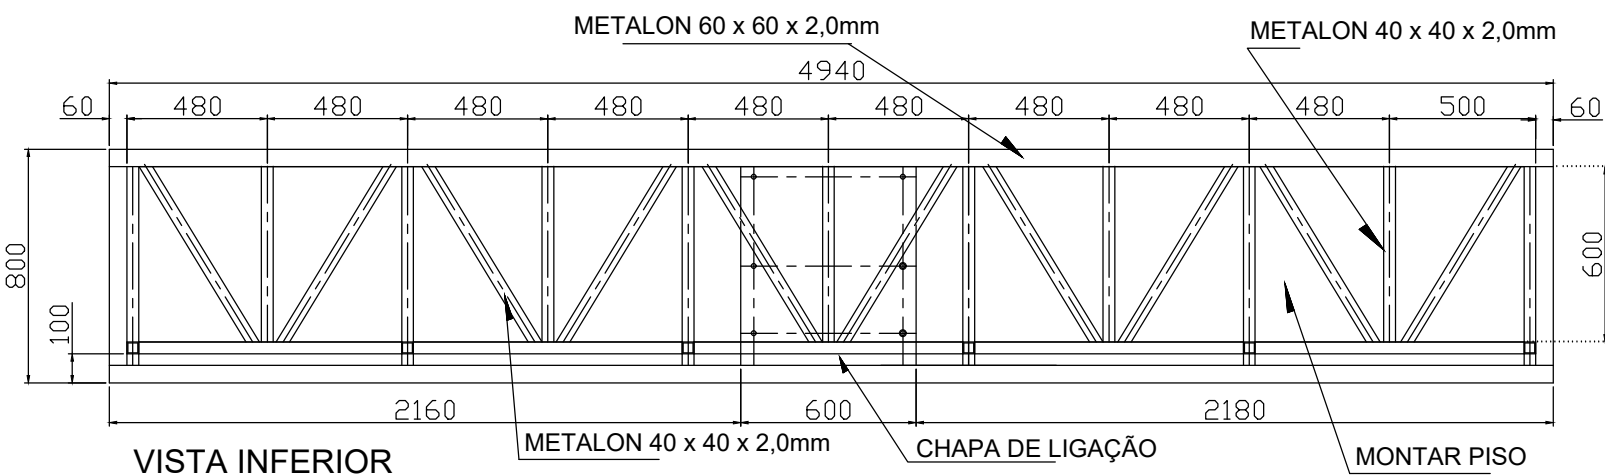

VISTA INFERIOR

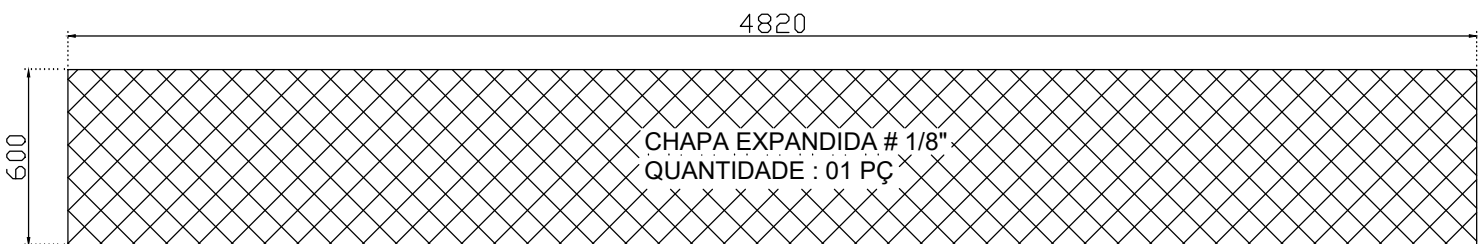

LISTA DE MATERIAIS						
	ESTRUTURA METÁLICA					
	DESCRIÇÃO	COMPR.	UNID.	QUANT.	PESO UNIT.	PESO TOTAL
01	METALON 60x60x2,0mm	6000mm	PÇS	06	21,69 KG	130,00 KG
02	METALON 40x40x2,0mm	6000mm	PÇS	13	14,5 KG	188,50 KG
03	CHAPA BASE # 1" x 680mm	680mm	PÇS	01	196,00 KG/M2	91,00 KG
04	CHAPA DE LIGAÇÃO # 5/8" x 680mm	600mm	PÇS	02	125,44 KG/M2	102,00 KG
05	CHAPA NERVURA A # 5/8" x 140mm	250mm	PÇS	08	125,50 KG/M2	35,00 KG
06	CHAPA NERVURA B # 5/8" x 130mm	200mm	PÇS	08	125,50 KG/M2	26,00 KG
07	CHAPA PILAR # 1/4" x 1256mm	2000mm	PÇS	02	49,39 KG/M2	248,00 KG
08	CHAPA EXPANDIDA # 1/8" x 600mm(PISO)	4820mm	PÇS	01	4,2 KG/M2	12,00 KG
09	CHAPA # 1/8" x 680mm (GABARITO)	680mm	PÇS	01	24,00 KG/M2	11,00 KG
10	FERRO REDONDO ø 5/8"	6000mm	PÇ	01	1,56 KG/M	9,36 KG
11	BARRA ROSQUEADA ø 1"	1000mm	PÇS	08	3,72 KG	29,80 KG
12	CHAPA # 3/8" x 100mm	100mm	PÇS	08	74,48 KG/M2	6,00 KG
13						
PESO TOTAL GERAL :						888,66 KG






NOTAS: MEDIDAS EM MILIMETRO;

2				
1				
0	INICIAL	F.G.S		08/02/23
N°	DESCRIÇÃO	DES.	RESP.	DATA

LED EXPERT

PROJETO SOMENTE PARA ORÇAMENTO
NÃO UTILIZAR PARA FABRICAÇÃO

OBRA			Data:		Desenhista:	
PAINEL 5x2 GB RENTAL OUTDOOR			08-02-2023		FABIAN	
CONTÉM: PROJETO DE ESTRUTURA METÁLICA						
ESCALA	PRANCHA	R.T.:	N° LED EXPERT:		FORMATO:	REVISÃO
IND.	01	--	84-2023-02-FL01		A2	0

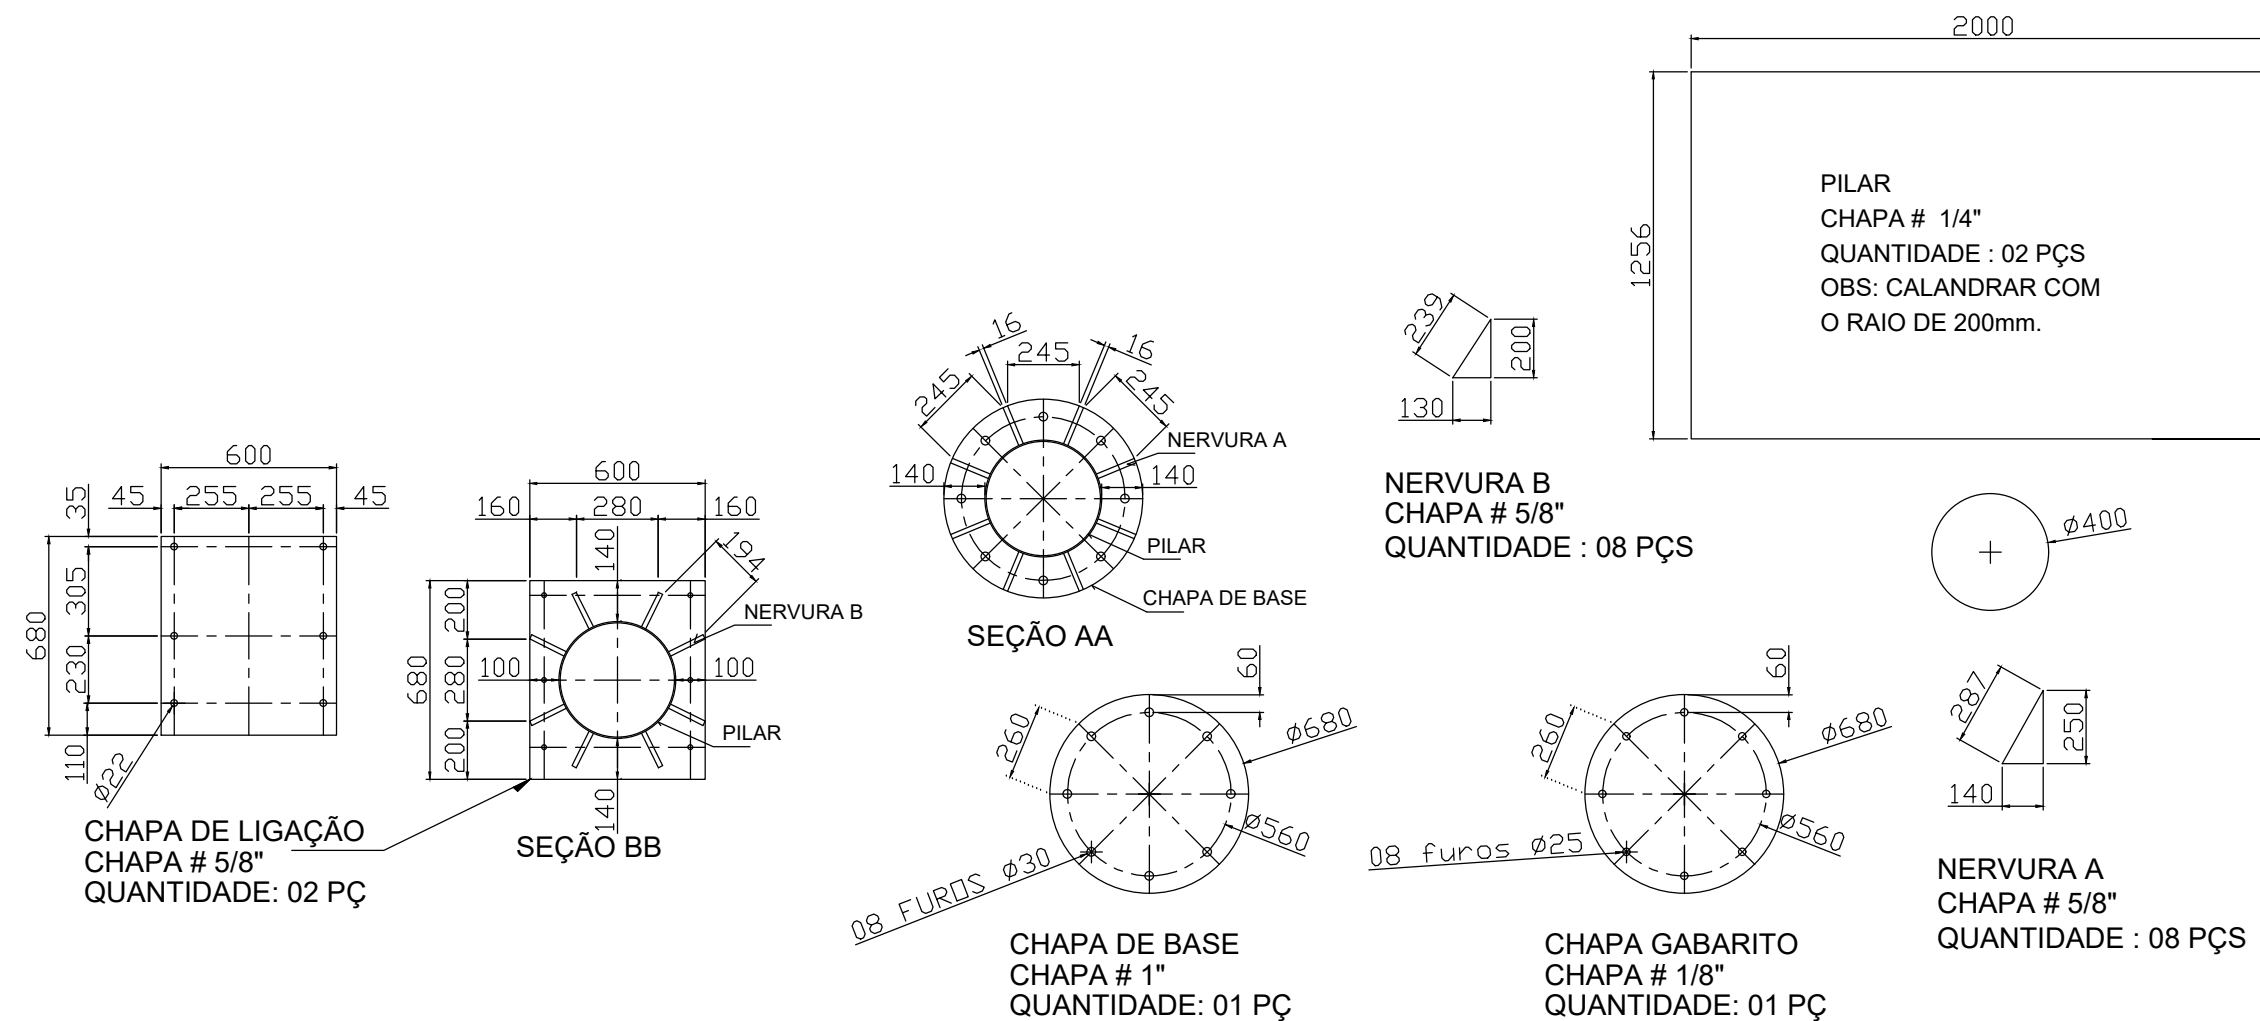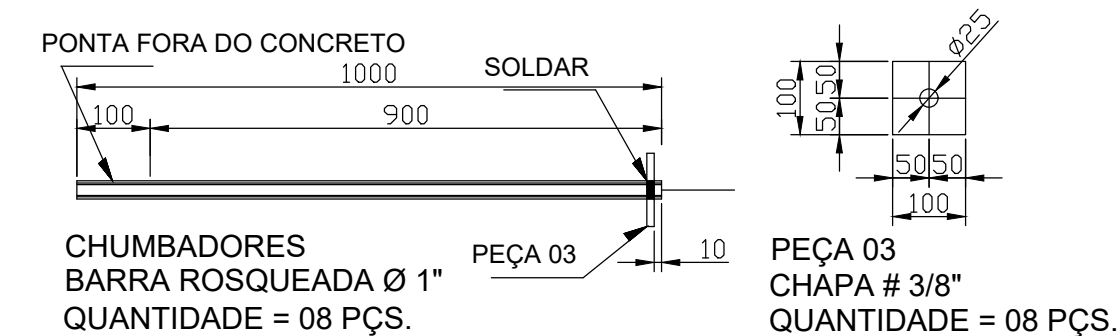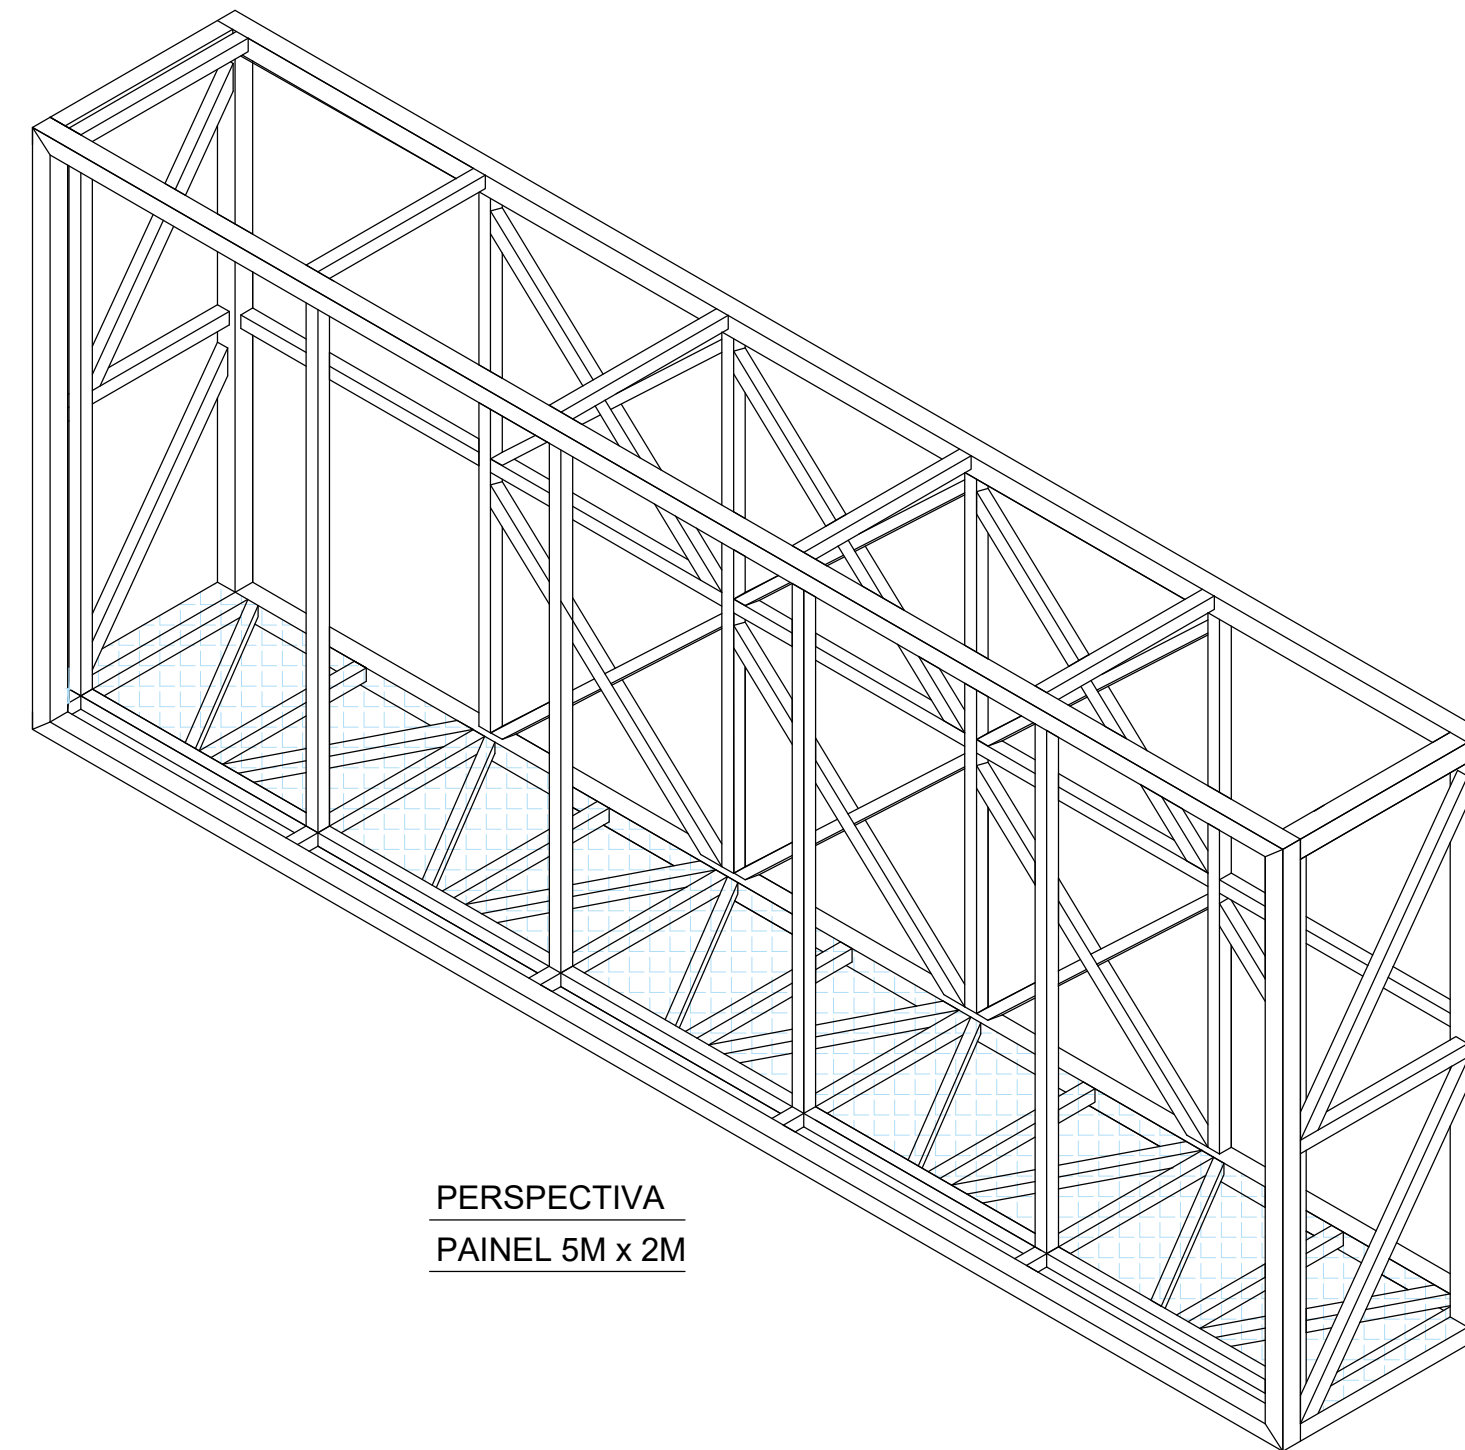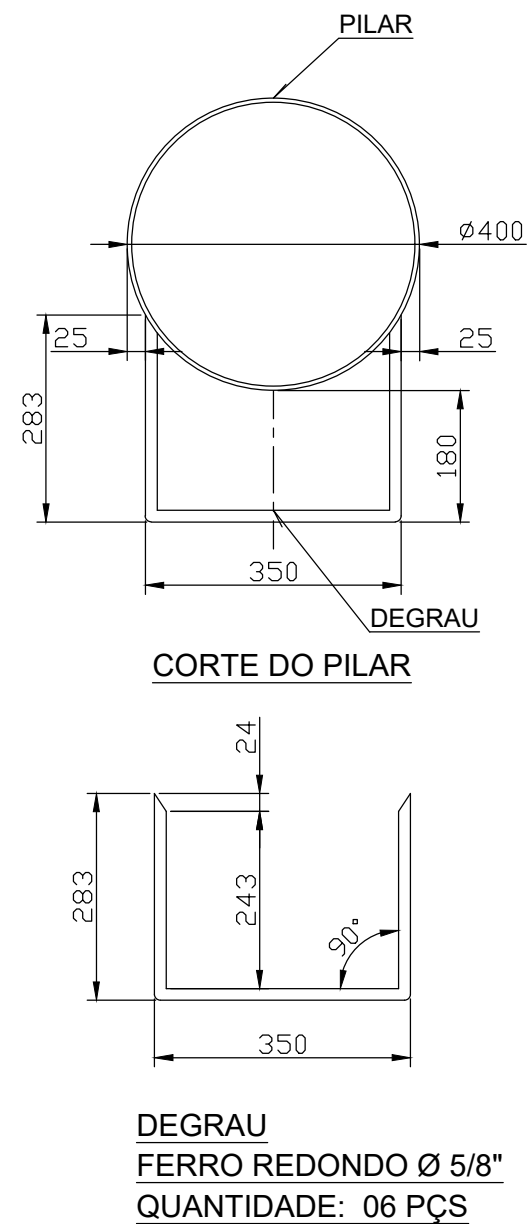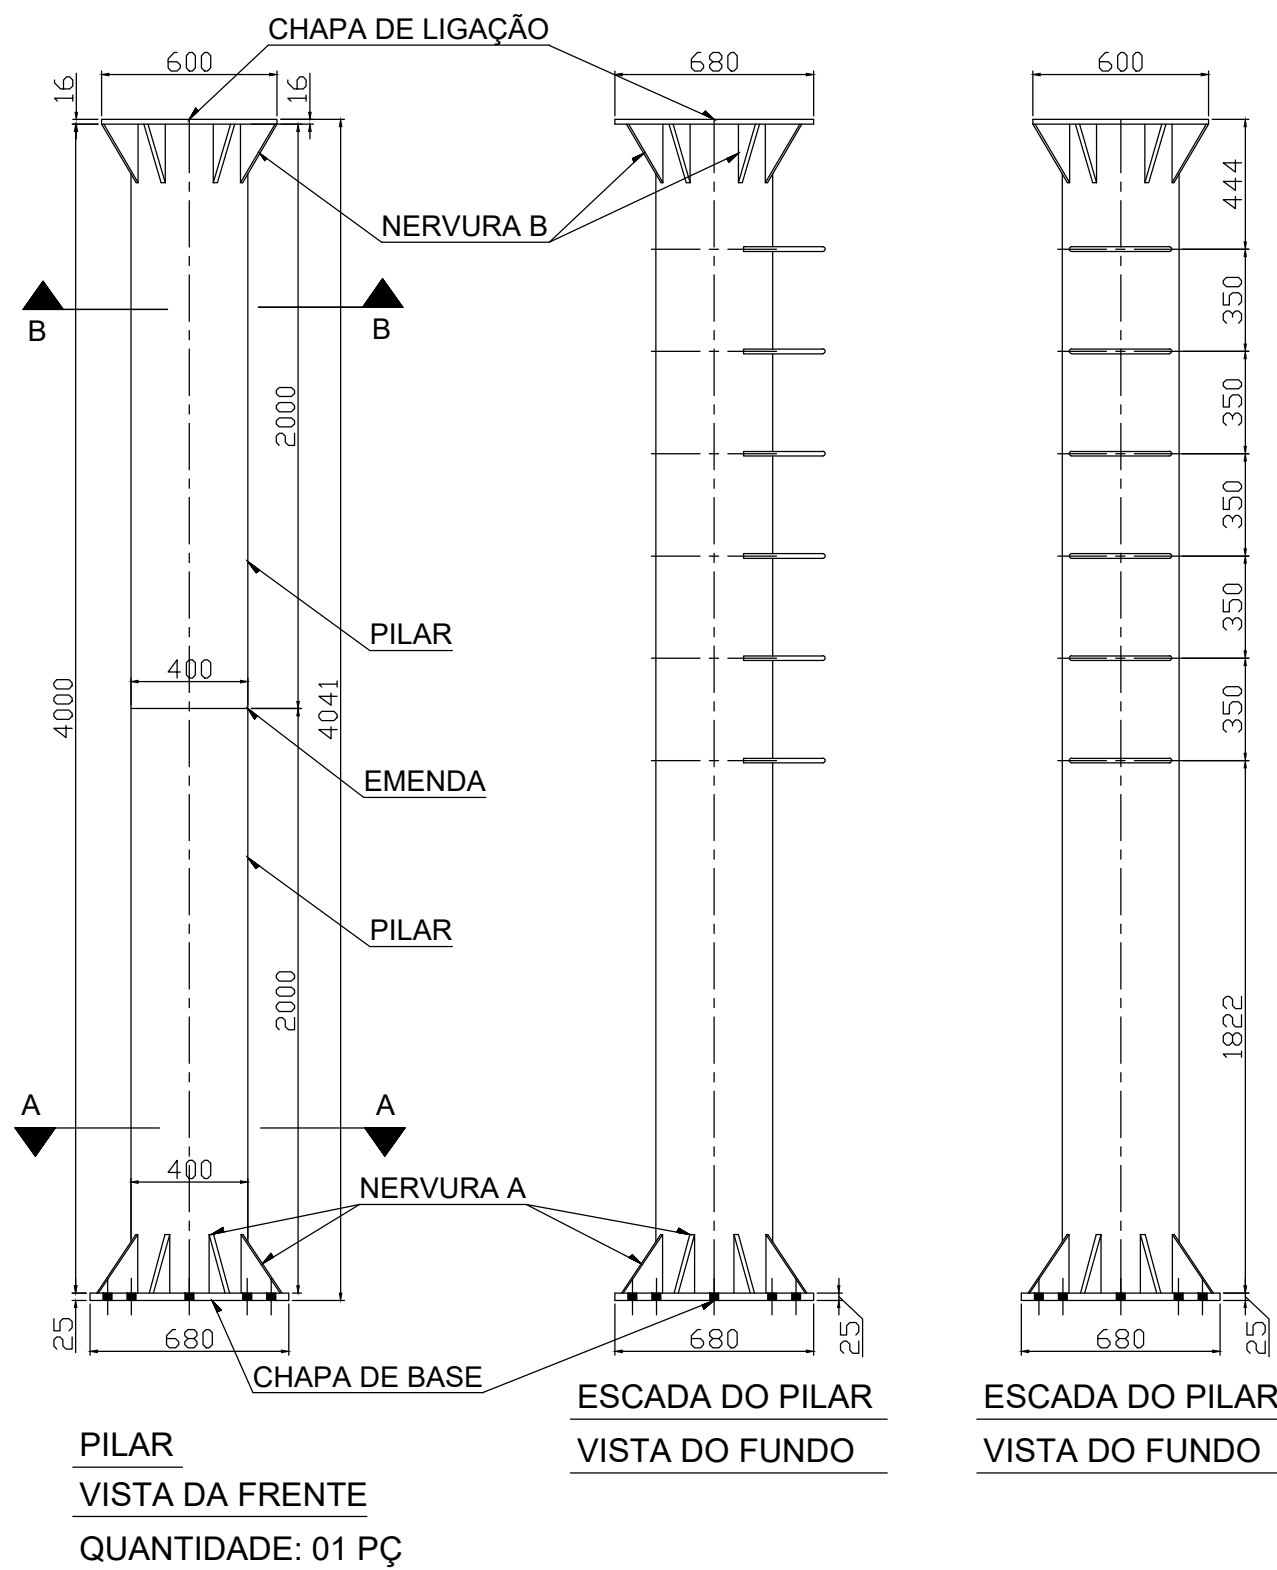

NOTAS: MEDIDAS EM MILIMETRO;				
2				
1				
0	INICIAL	F.G.S		08/02/23
N°	DESCRIÇÃO	DES.	RESP.	DATA
LED EXPERT				
PROJETO SOMENTE PARA ORÇAMENTO NÃO UTILIZAR PARA FABRICAÇÃO				
OBRA	PAINEL 5x2 GB RENTAL	Data:	08-02-2023	Desenhista: FABIAN
CONTÉM:	PROJETO DE ESTRUTURA METÁLICA			
ESCALA	PRANCHA	R.T.:	N° LED EXPERT:	FORMATO:
IND.	01	--	84-202-02-FL02	A2
				REVISÃO
				0