




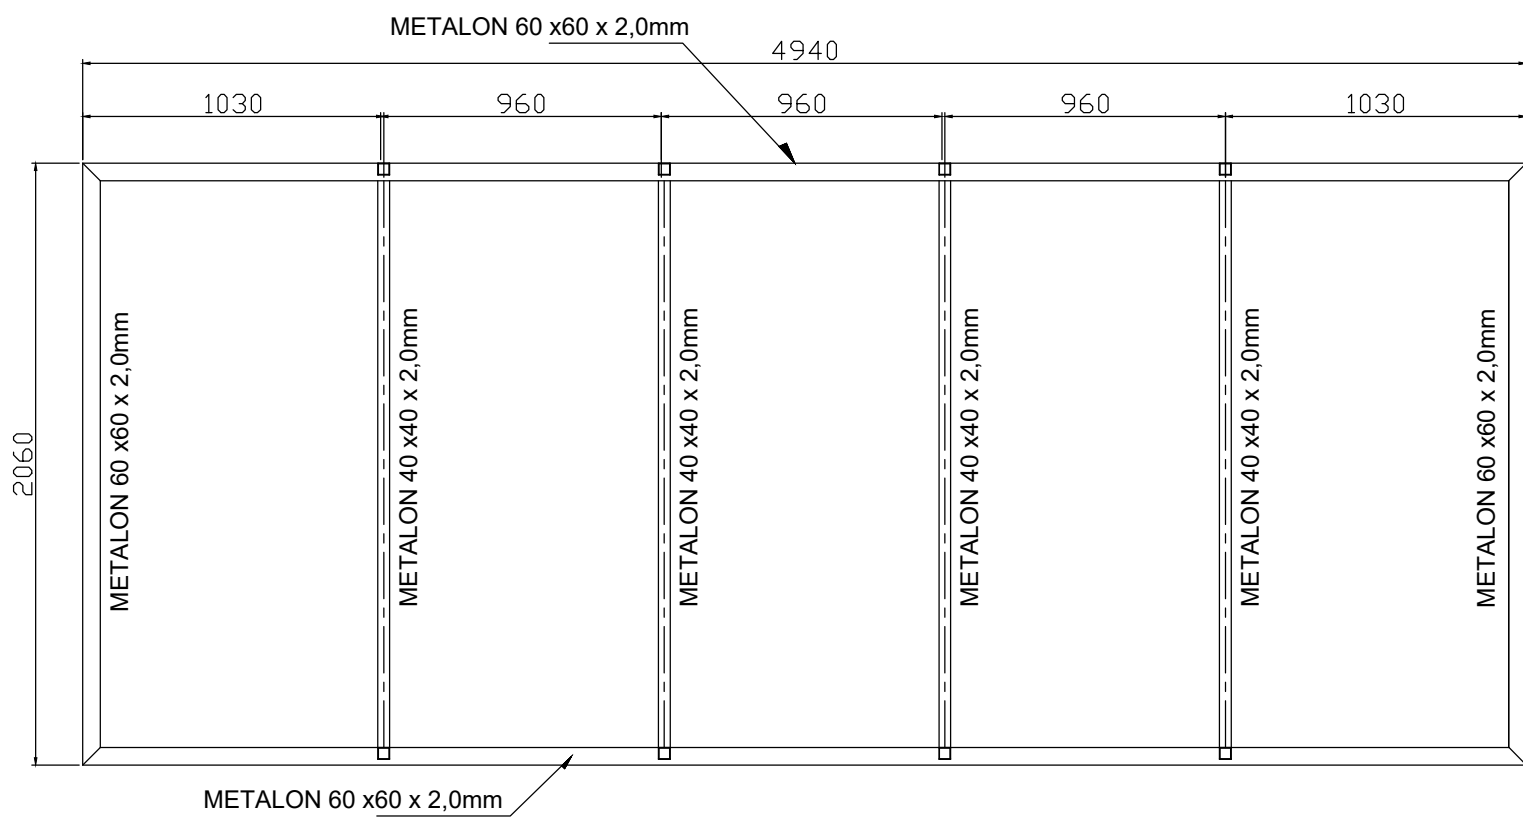


VISTA FRONTAL

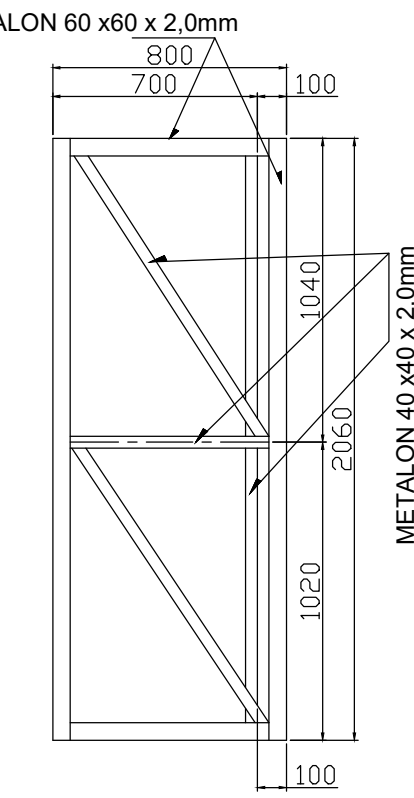


VISTA LATERAL

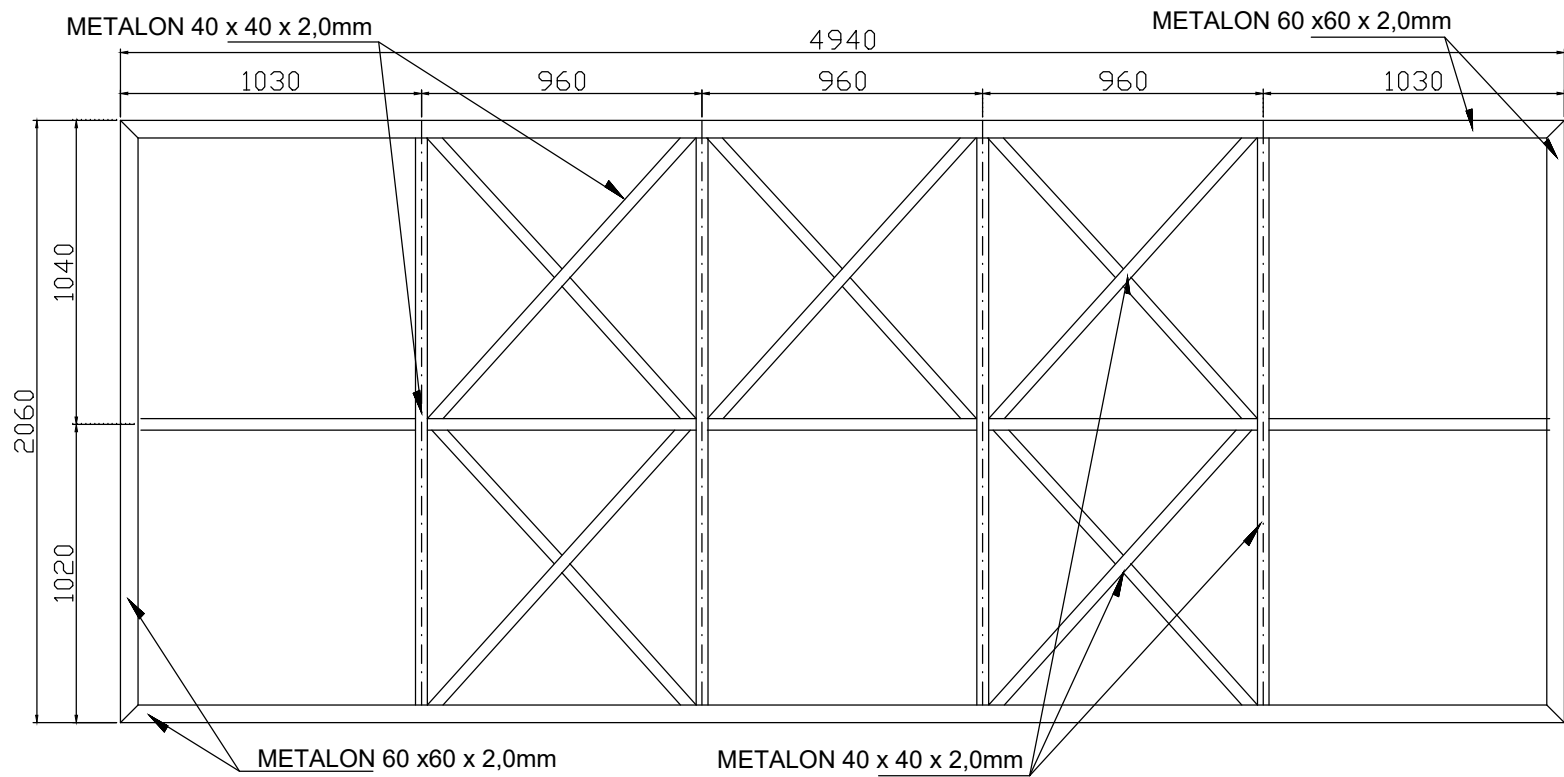


VISTA DO FUNDO

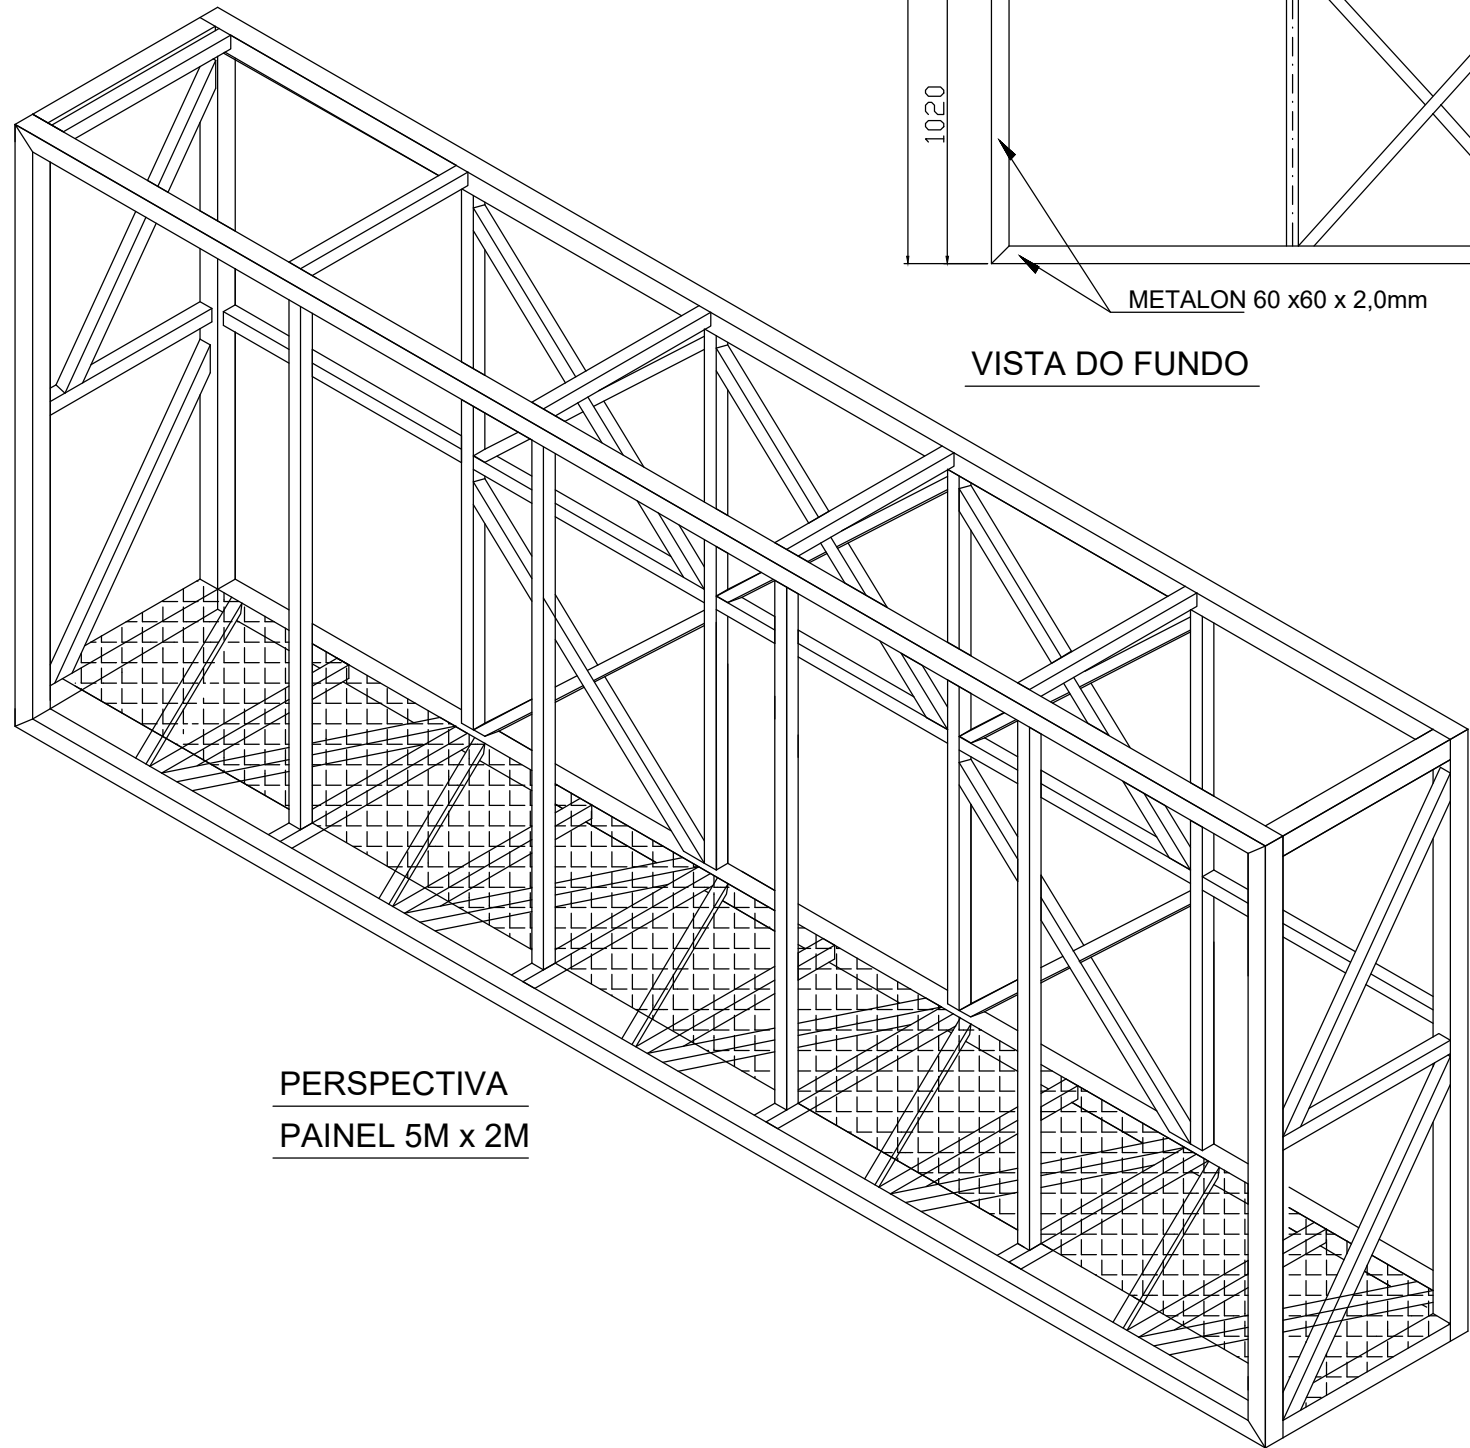


PERSPECTIVA
PAINEL 5M x 2M

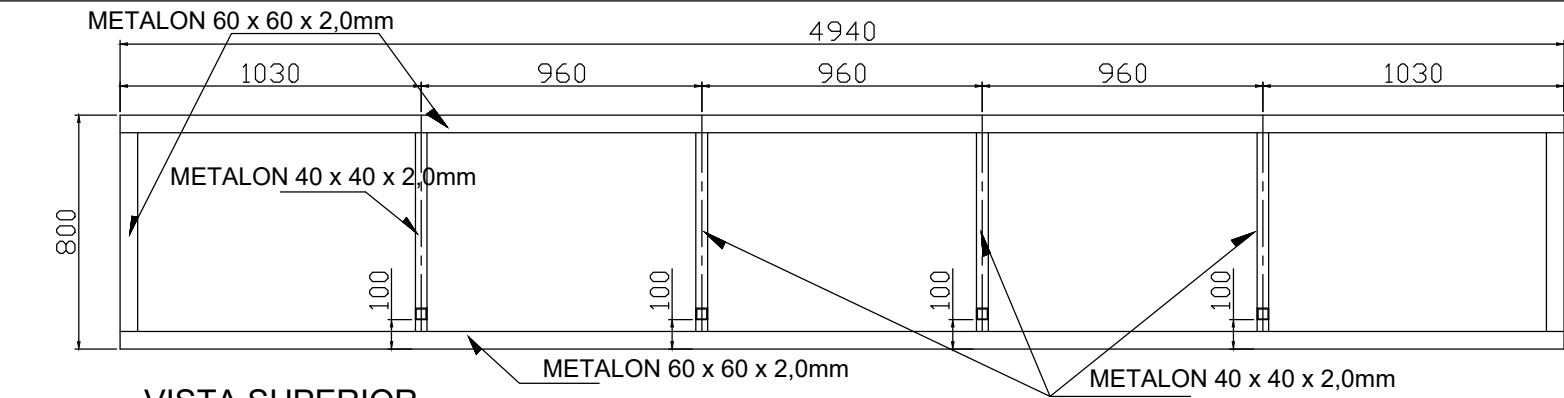

VISTA SUPERIOR

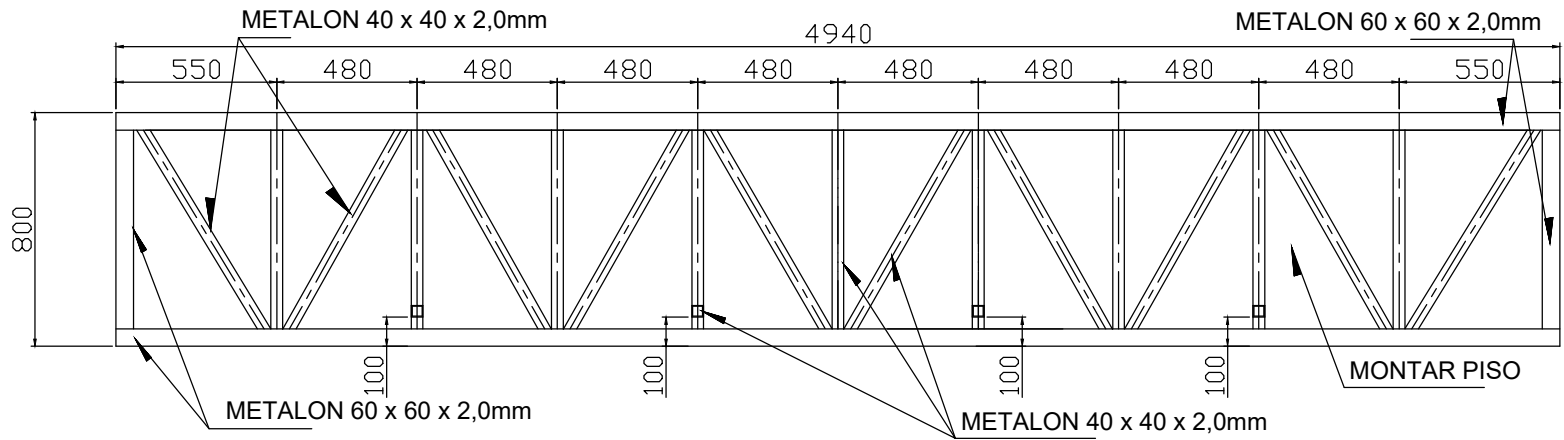

VISTA INFERIOR

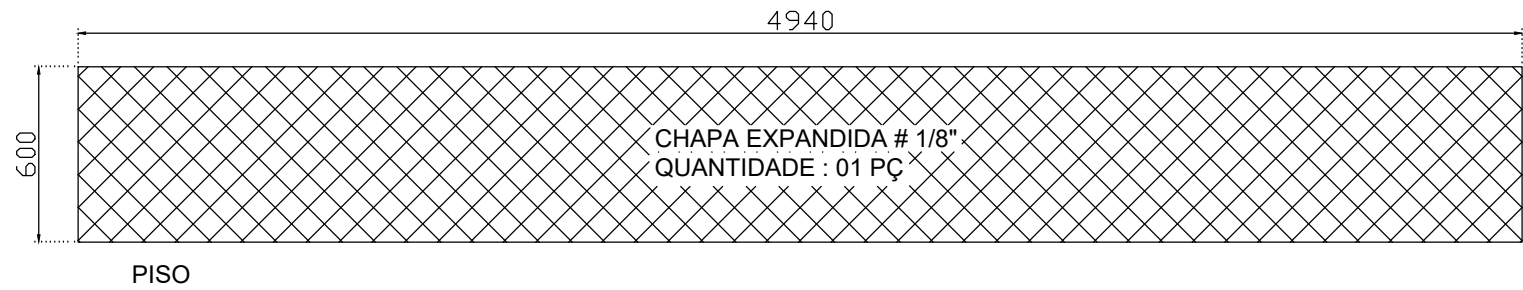

LISTA DE MATERIAIS						
	ESTRUTURA METÁLICA					
	DESCRIÇÃO	COMPR.	UNID.	QUANT.	PESO UNIT.	PESO TOTAL.
01	METALON 60x60x2,0mm	6000mm	PÇS	06	3,61 KG	129,96 KG
02	METALON 40x40x2,0mm	6000mm	PÇS	11	2,41 KG	159,06 KG
03	CHAPA EXPANDIDA # 1/8" x 600mm(PISO)	4940mm	PÇS	01	4,2 KG/M2	12,44 KG
04						
05						
06						
07						
08						
09						
10						
11						
PESO TOTAL GERAL :						301,46 KG

NOTAS: MEDIDAS EM MILIMETRO;

2				
1				
0	INICIAL	F.G.S		13/12/23
N°	DESCRIÇÃO	DES.	RESP.	DATA

LED EXPERT

PROJETO SOMENTE PARA ORÇAMENTO
NÃO UTILIZAR PARA FABRICAÇÃO

OBRA			Data:		Desenhista:	
PAINEL 5x2 GB RENTAL OUTDOOR			13-12-2023		FABIAN	
CONTÉM:						
PROJETO DE ESTRUTURA METÁLICA						
ESCALA	PRANCHA	R.T.:	N° LED EXPERT:		FORMATO:	REVISÃO
IND.	01	--	243-2023-12-FL01		A2	0