



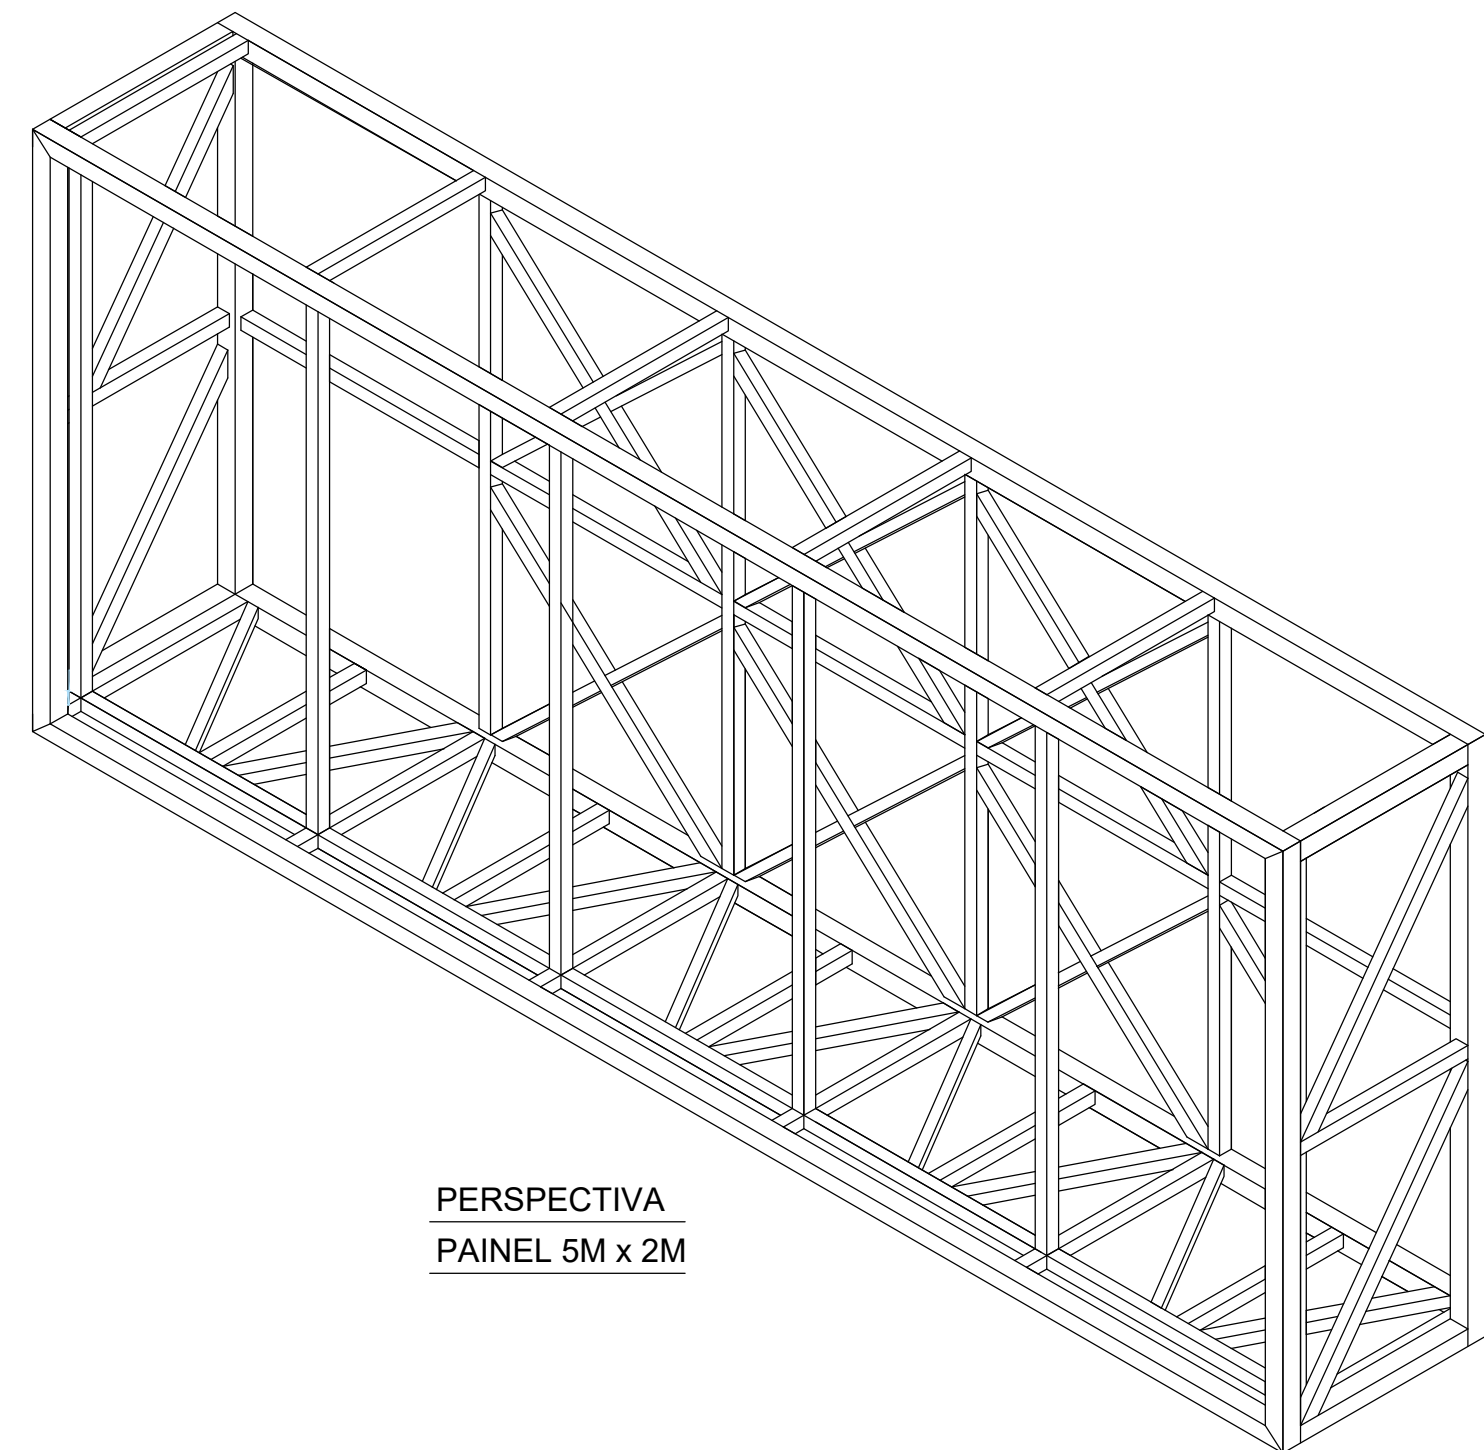


PERSPECTIVA


PAINEL 5M x 2M

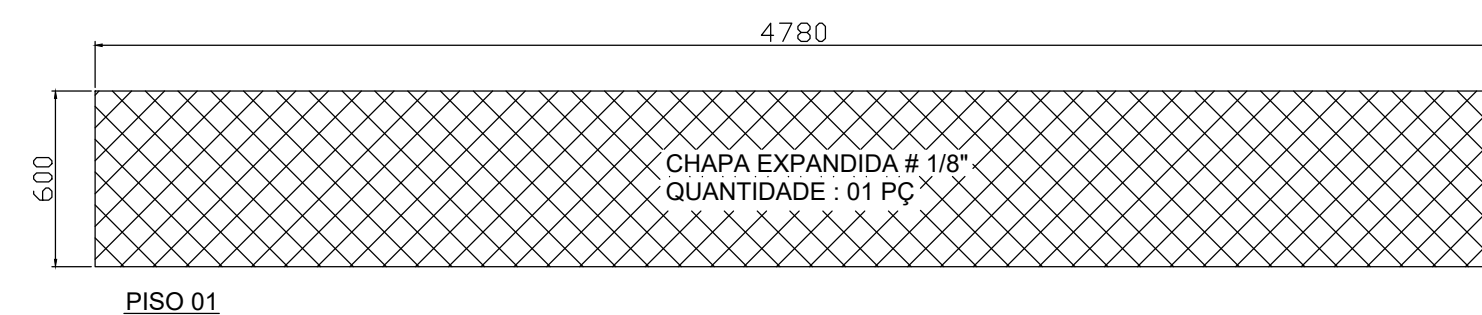

VISTA DO FUNDO



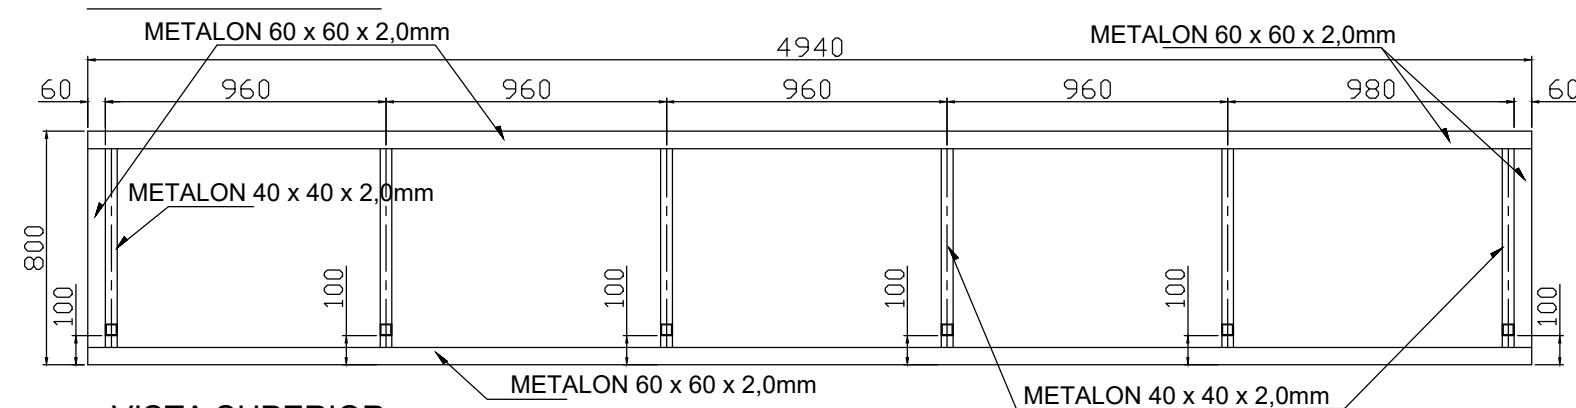


VISTA SUPERIOR

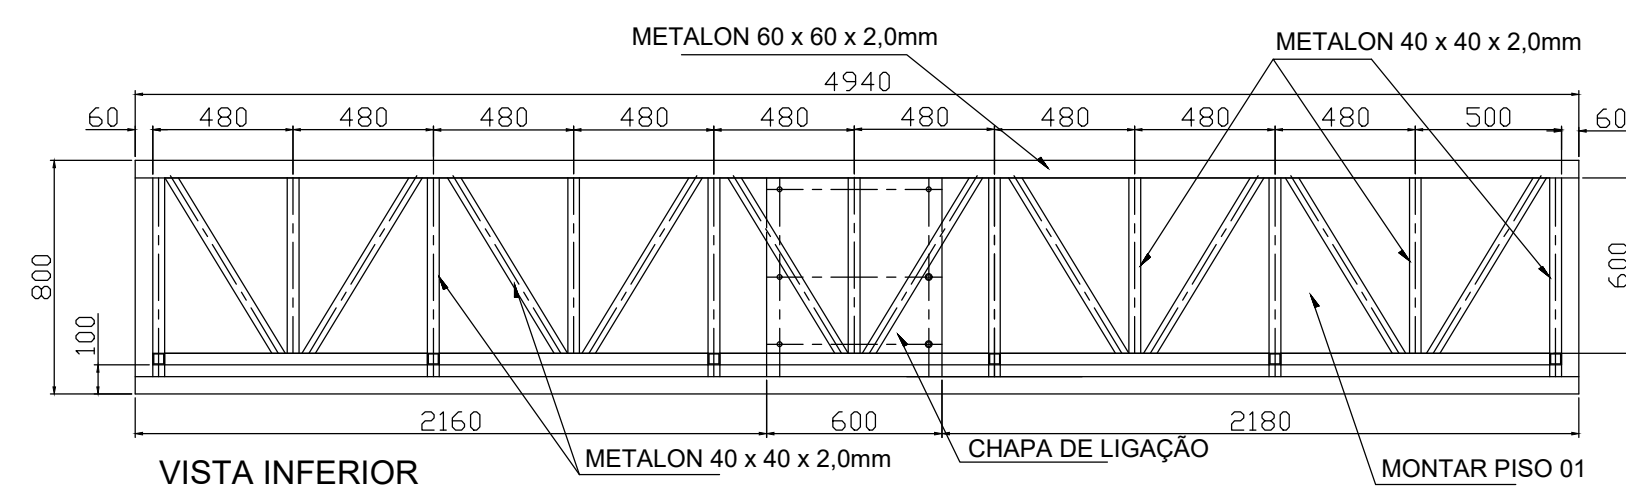

VISTA INFERIOR

NOTAS: MEDIDAS EM CENTIMETRO;					
2					
1					
0	INICIAL	F.G.S		18/05/23	
N°	DESCRIÇÃO	DES.	RESP.	DATA	
LED EXPERT					
PROJETO SOMENTE PARA ORÇAMENTO NÃO UTILIZAR PARA FABRICAÇÃO					
OBRA PAINEL 5x2 GB RENTAL OUTDOOR		Data: 18-04-2023	Desenhista: FABIAN		
CONTEM: PROJETO DE ESTRUTURA METÁLICA					
ESCALA IND.	PRANCHA 01	R.T.: --	N° LED EXPERT: 123-2023-03-FL01	FORMATO: A2	REVISÃO 0

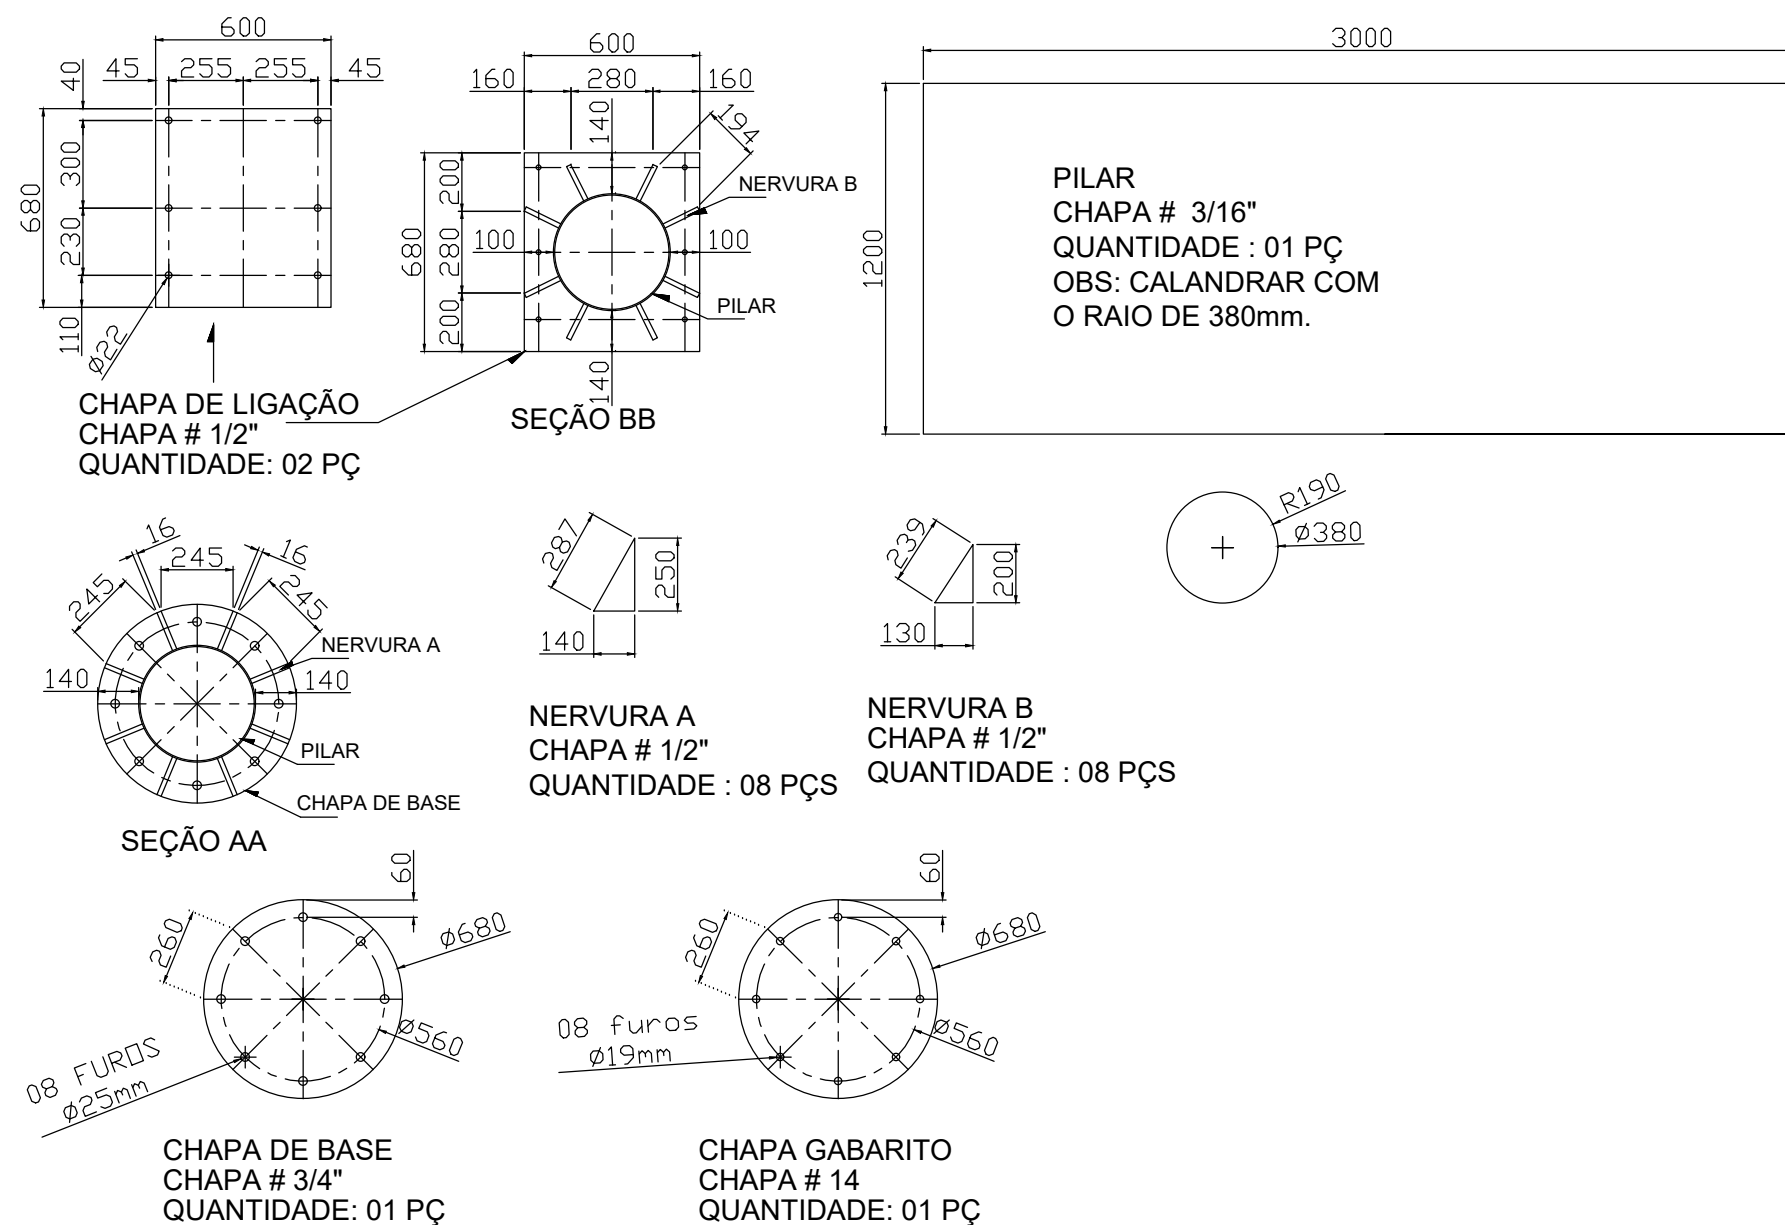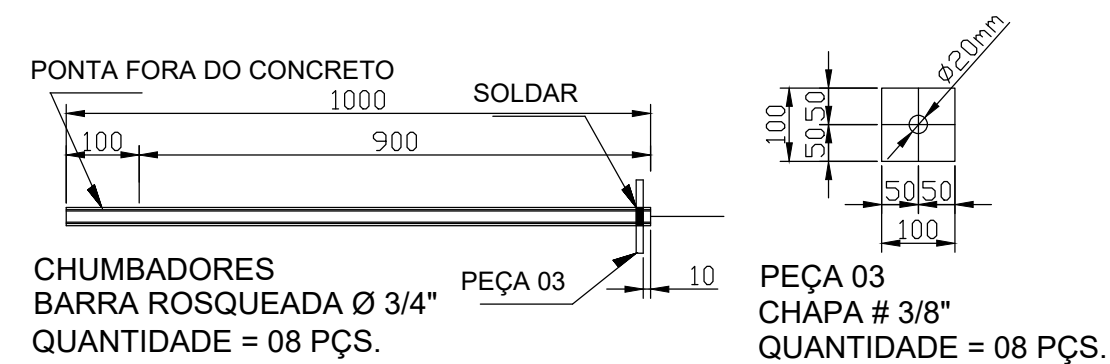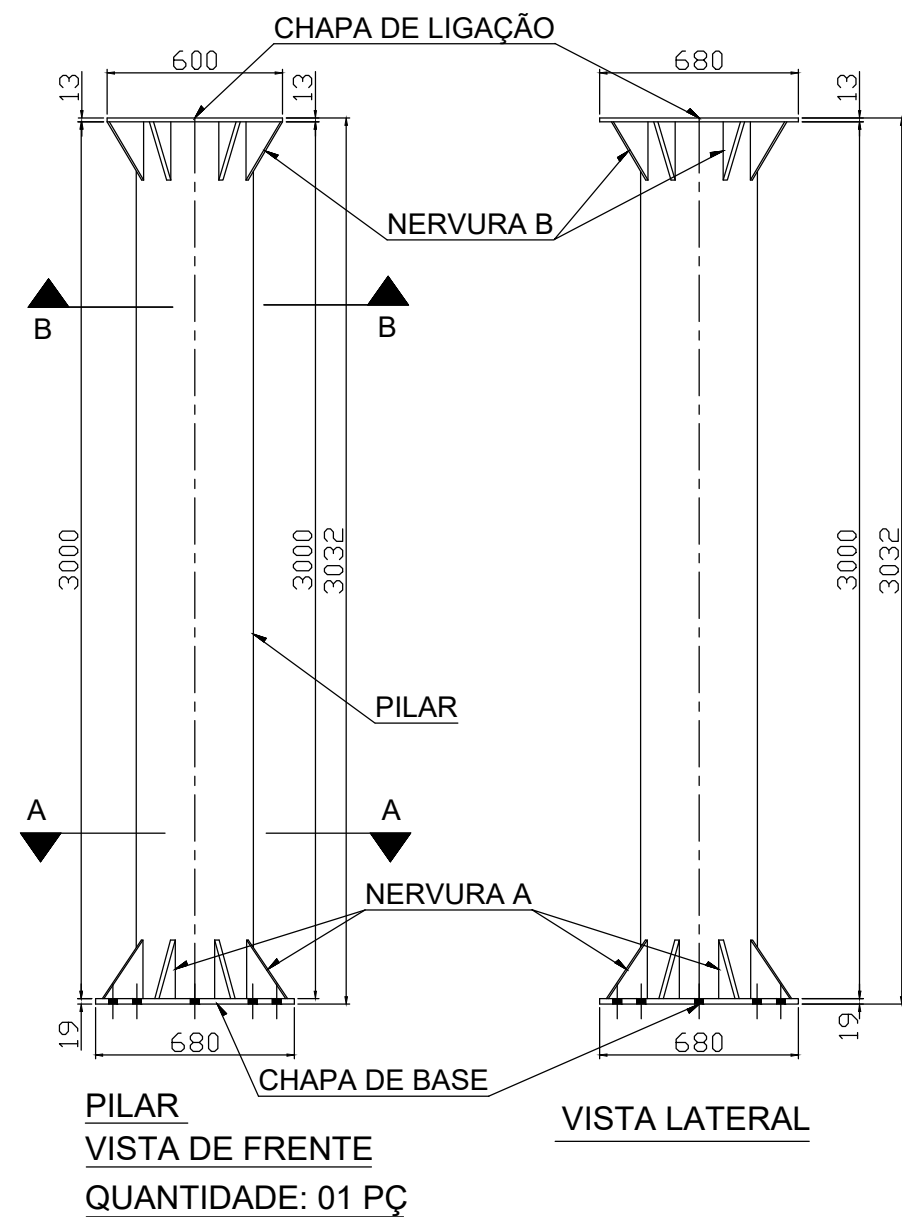

LISTA DE MATERIAIS						
Cliente: DAVID ZOVISK				DATA: 18/05/2023		
Obra: PAINEL 5x2 GB RENTAL OUTDOOR (PILAR TUBULAR)						
	ESTRUTURA METÁLICA					
	DESCRIÇÃO	COMPR.	UNID.	QUANT.	PESO UNIT.	PESO TOTAL
01	METALON 60x60x2,0mm	6000mm	PÇS	06	3,66 KG	131,76 KG
02	METALON 40x40x2,0mm	6000mm	PÇS	13	2,41 KG	187,98 KG
03	CHAPA BASE # 3/4" x ø 680mm	680mm	PÇS	01	149,00 KG/M2	54,08 KG
04	CHAPA DE LIGAÇÃO # 1/2" x 600mm	680mm	PÇS	02	98,00 KG/M2	79,96 KG
05	CHAPA # 1/2" x 140mm (NERVURA A)	250mm	PÇS	08	98,00 KG/M2	13,72 KG
06	CHAPA # 1/2" x 130mm (NERVURA B)	200mm	PÇS	08	98,00 KG/M2	10,19 KG
07	CHAPA # 3/16" x 1200mm (PILAR)	3000mm	PÇ	01	38,00 KG/M2	136,80 KG
08	CHAPA EXPANDIDA # 1/8" x 600mm(PISO 01)	4820mm	PÇS	01	4,2 KG/M2	12,14 KG
09	CHAPA # 14 x ø 680mm (GABARITO)	680mm	PÇS	01	16,00 KG/M2	6,52 KG
10	BARRA ROSQUEADA ø 3/4" (CHUMBADOR)	1000mm	PÇS	08	2,24 KG/M	17,92 KG
11	CHAPA # 3/8" x ø 100mm (PEÇA 03)	100mm	PÇS	08	74,48 KG/M2	5,95 KG
PESO TOTAL GERAL :					657,02 KG	

NOTAS: MEDIDAS EM MILIMETRO;

2				
1				
0	INICIAL	F.G.S		18/05/23
N°	DESCRIÇÃO	DES.	RESP.	DATA

LED EXPERT

PROJETO SOMENTE PARA ORÇAMENTO
NÃO UTILIZAR PARA FABRICAÇÃO

OBRA			Data:		Desenhista:	
PAINEL 5x2 GB RENTAL OUTDOOR			18-05-2023		FABIAN	
CONTÉM:						
PROJETO DE ESTRUTURA METÁLICA – PILAR TUBULAR						
ESCALA	PRANCHA	R.T.:	Nº LED EXPERT:	FORMATO:	REVISÃO	
IND.	02	--	123-2023-05-FL02	A2	0	