




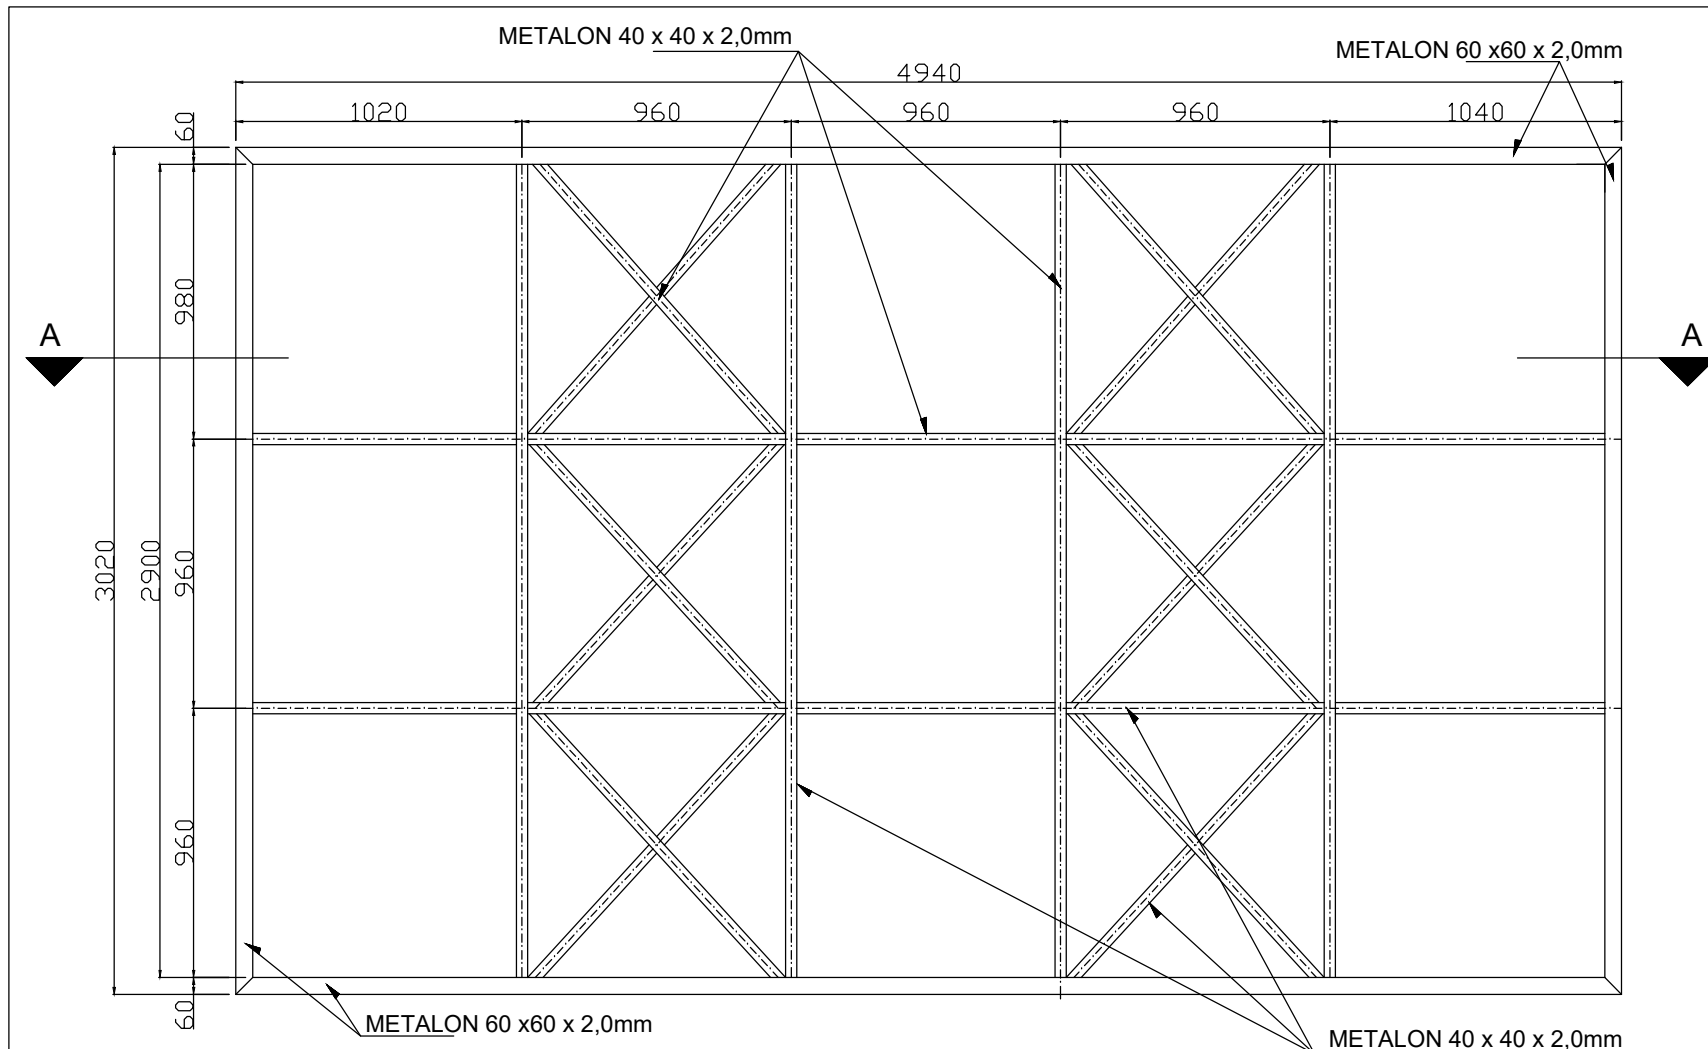


VISTA DO FUNDO

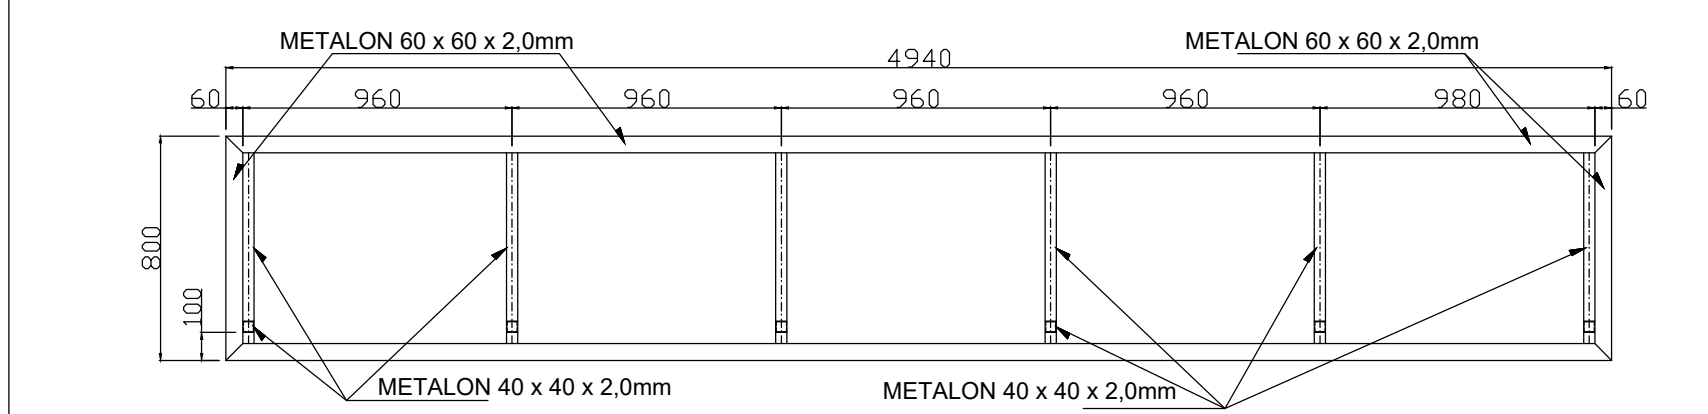


VISTA SUPERIOR

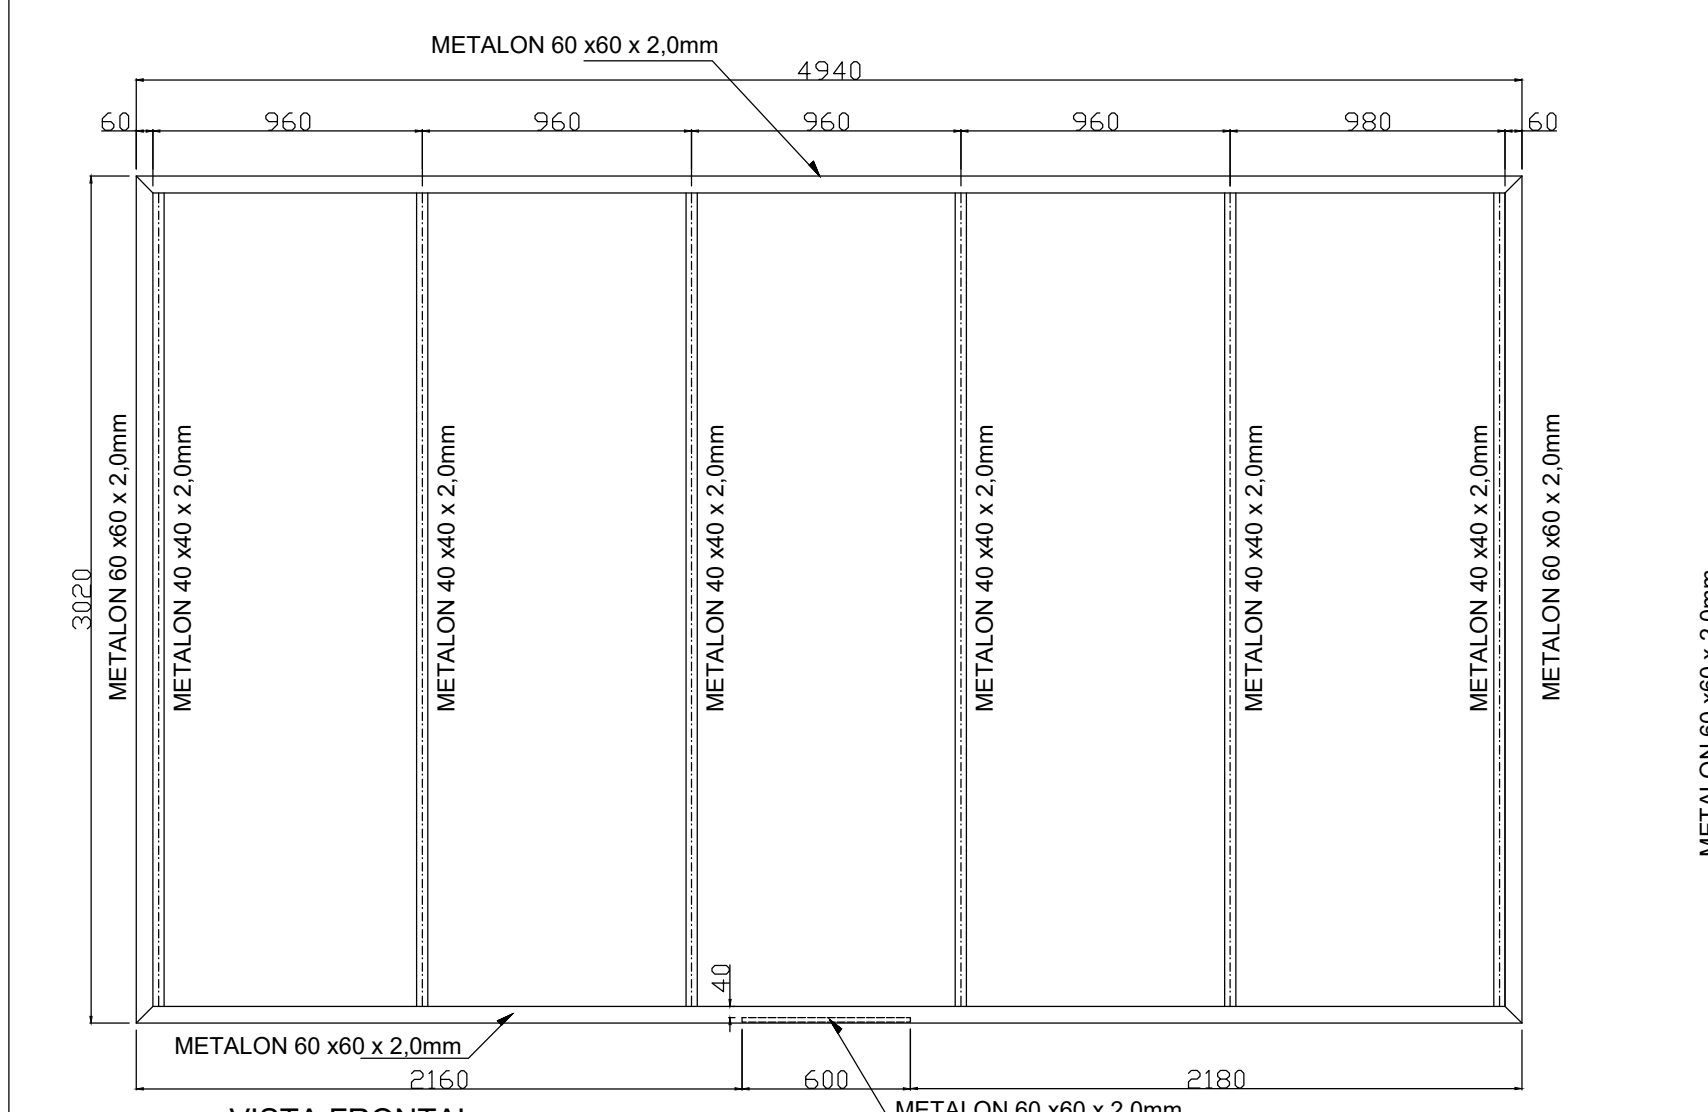


VISTA FRONTAL

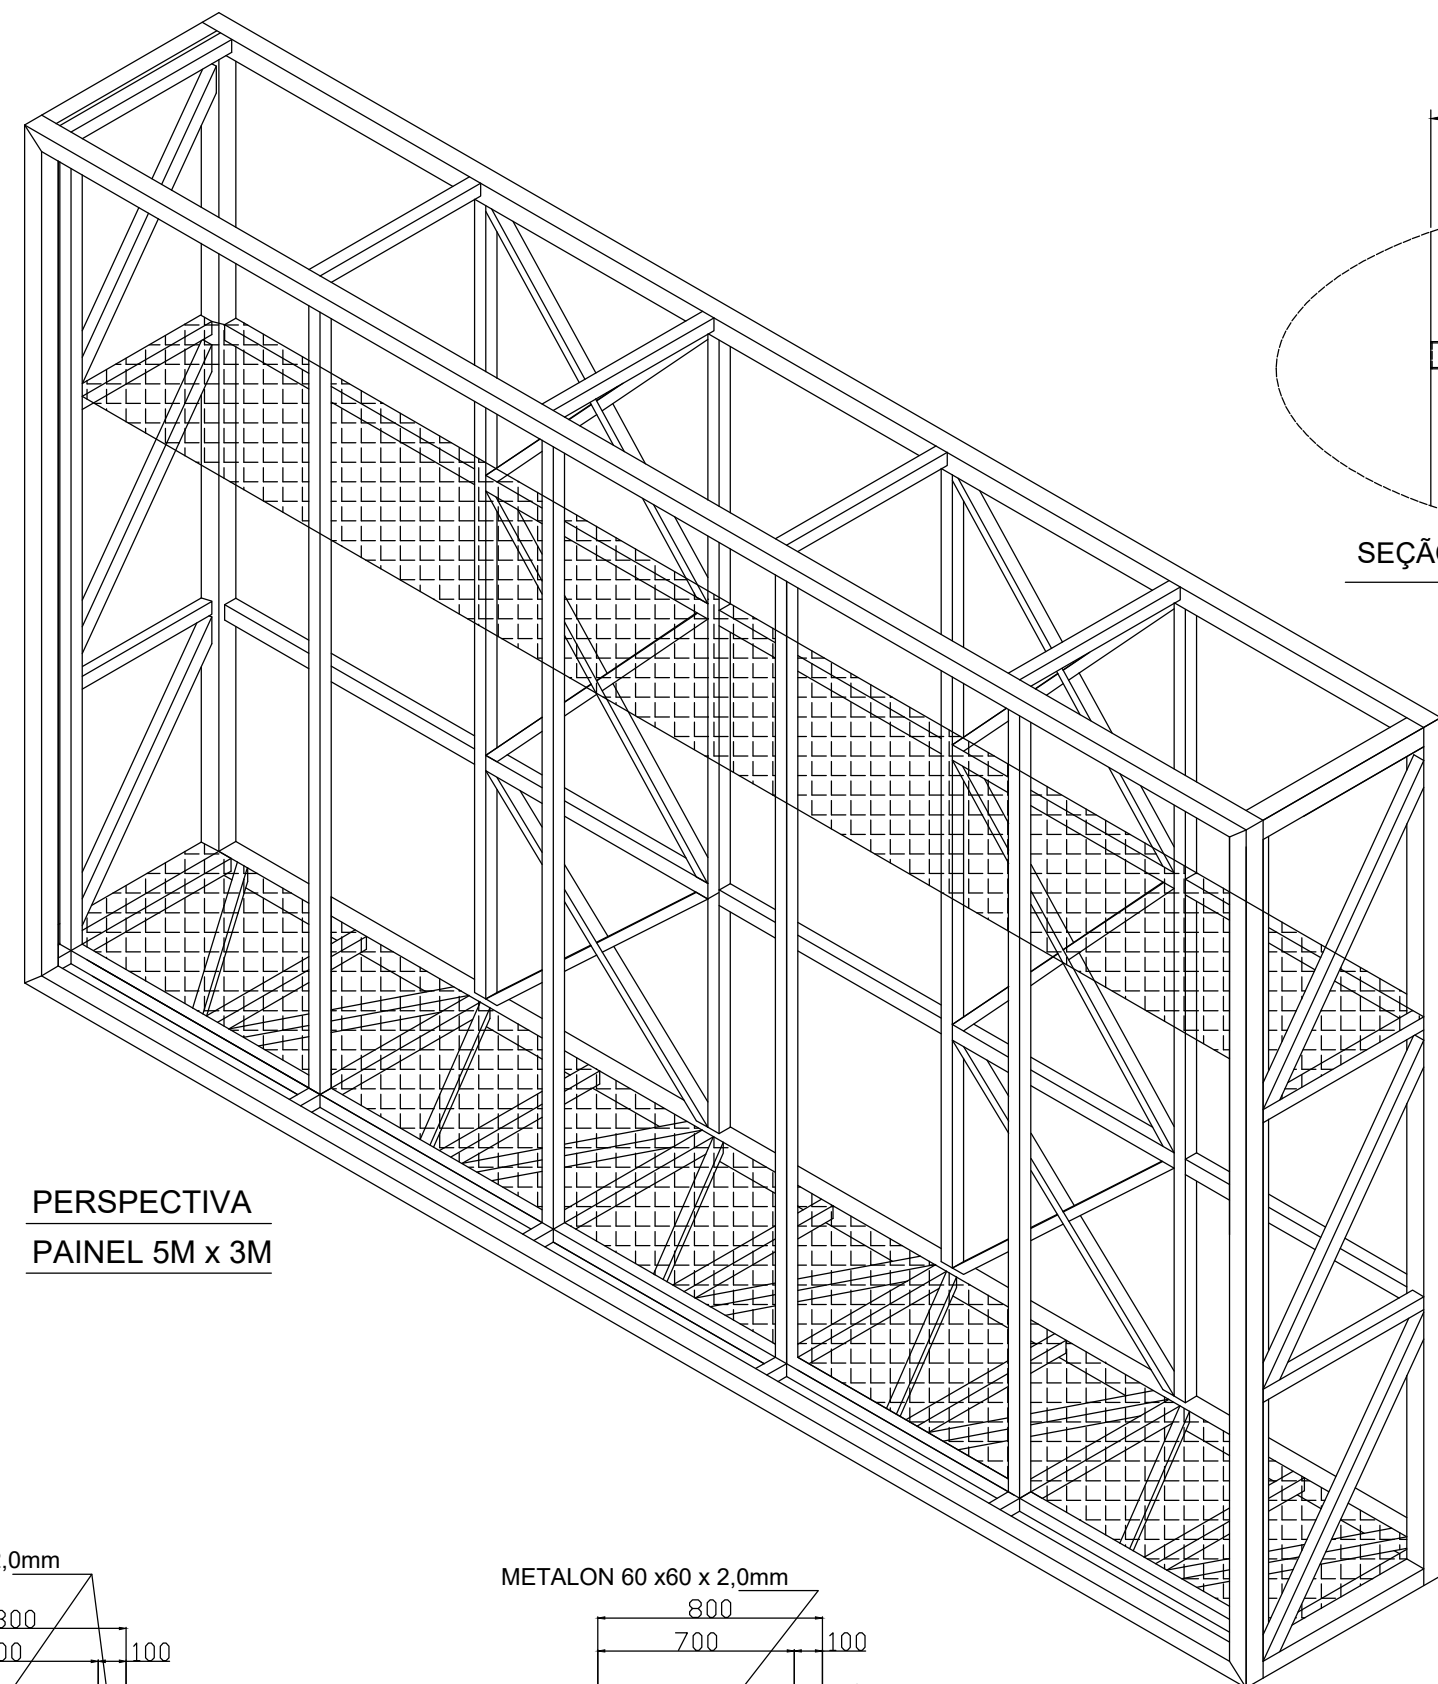


PERSPECTIVA
PAINEL 5M x 3M

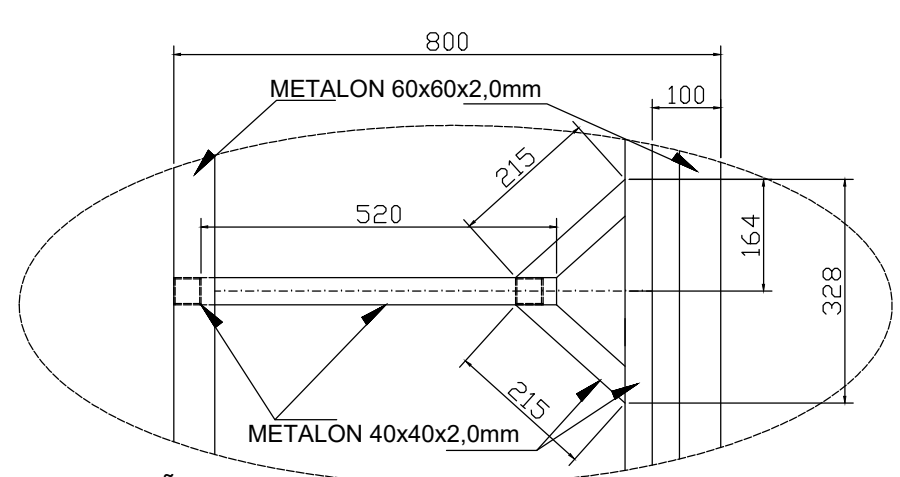

SEÇÃO BB

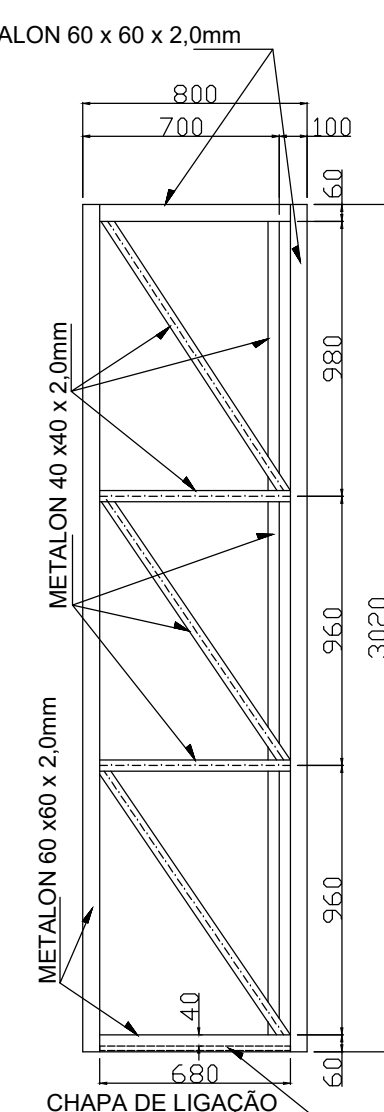

VISTA LATERAL

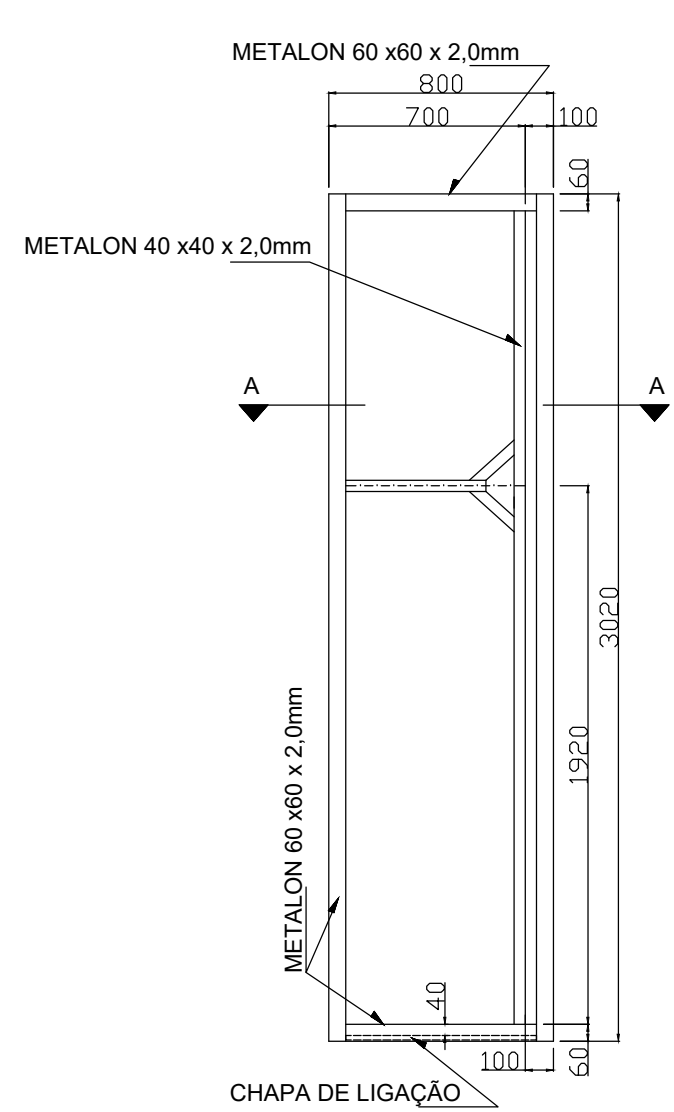

PLATAFORMAS
SECUNDÁRIAS

NOTAS: MEDIDAS EM MILIMETRO;				
4				
3				
2				
1				
0	INICIAL	F.G.S		21/11/23
N°	DESCRIÇÃO	DES.	RESP.	DATA
LED EXPERT				
PROJETO SOMENTE PARA ORÇAMENTO NÃO UTILIZAR PARA FABRICAÇÃO				
OBRA PAINEL 5x3 GB RENTAL OUTDOOR		Data: 21-11-2023	Desenhista: FABIAN	
CONTÉM: PROJETO DE ESTRUTURA METÁLICA				
ESCALA IND.	SE --	R.T.: --	N° LED EXPERT: 225-2023-11-FL-02	FORMATO: REVISÃO A2 0

OBRA PAINEL 5x3 GB RENTAL OUTDOOR			Data: 21-11-2023	Desenhista: FABIAN	
CONTÉM: PROJETO DE ESTRUTURA METÁLICA					
ESCALA IND.	SE --	R.T.: --	Nº LED EXPERT: 225-2023-11-FL-01	FORMATO: A2	REVISÃO 0

