

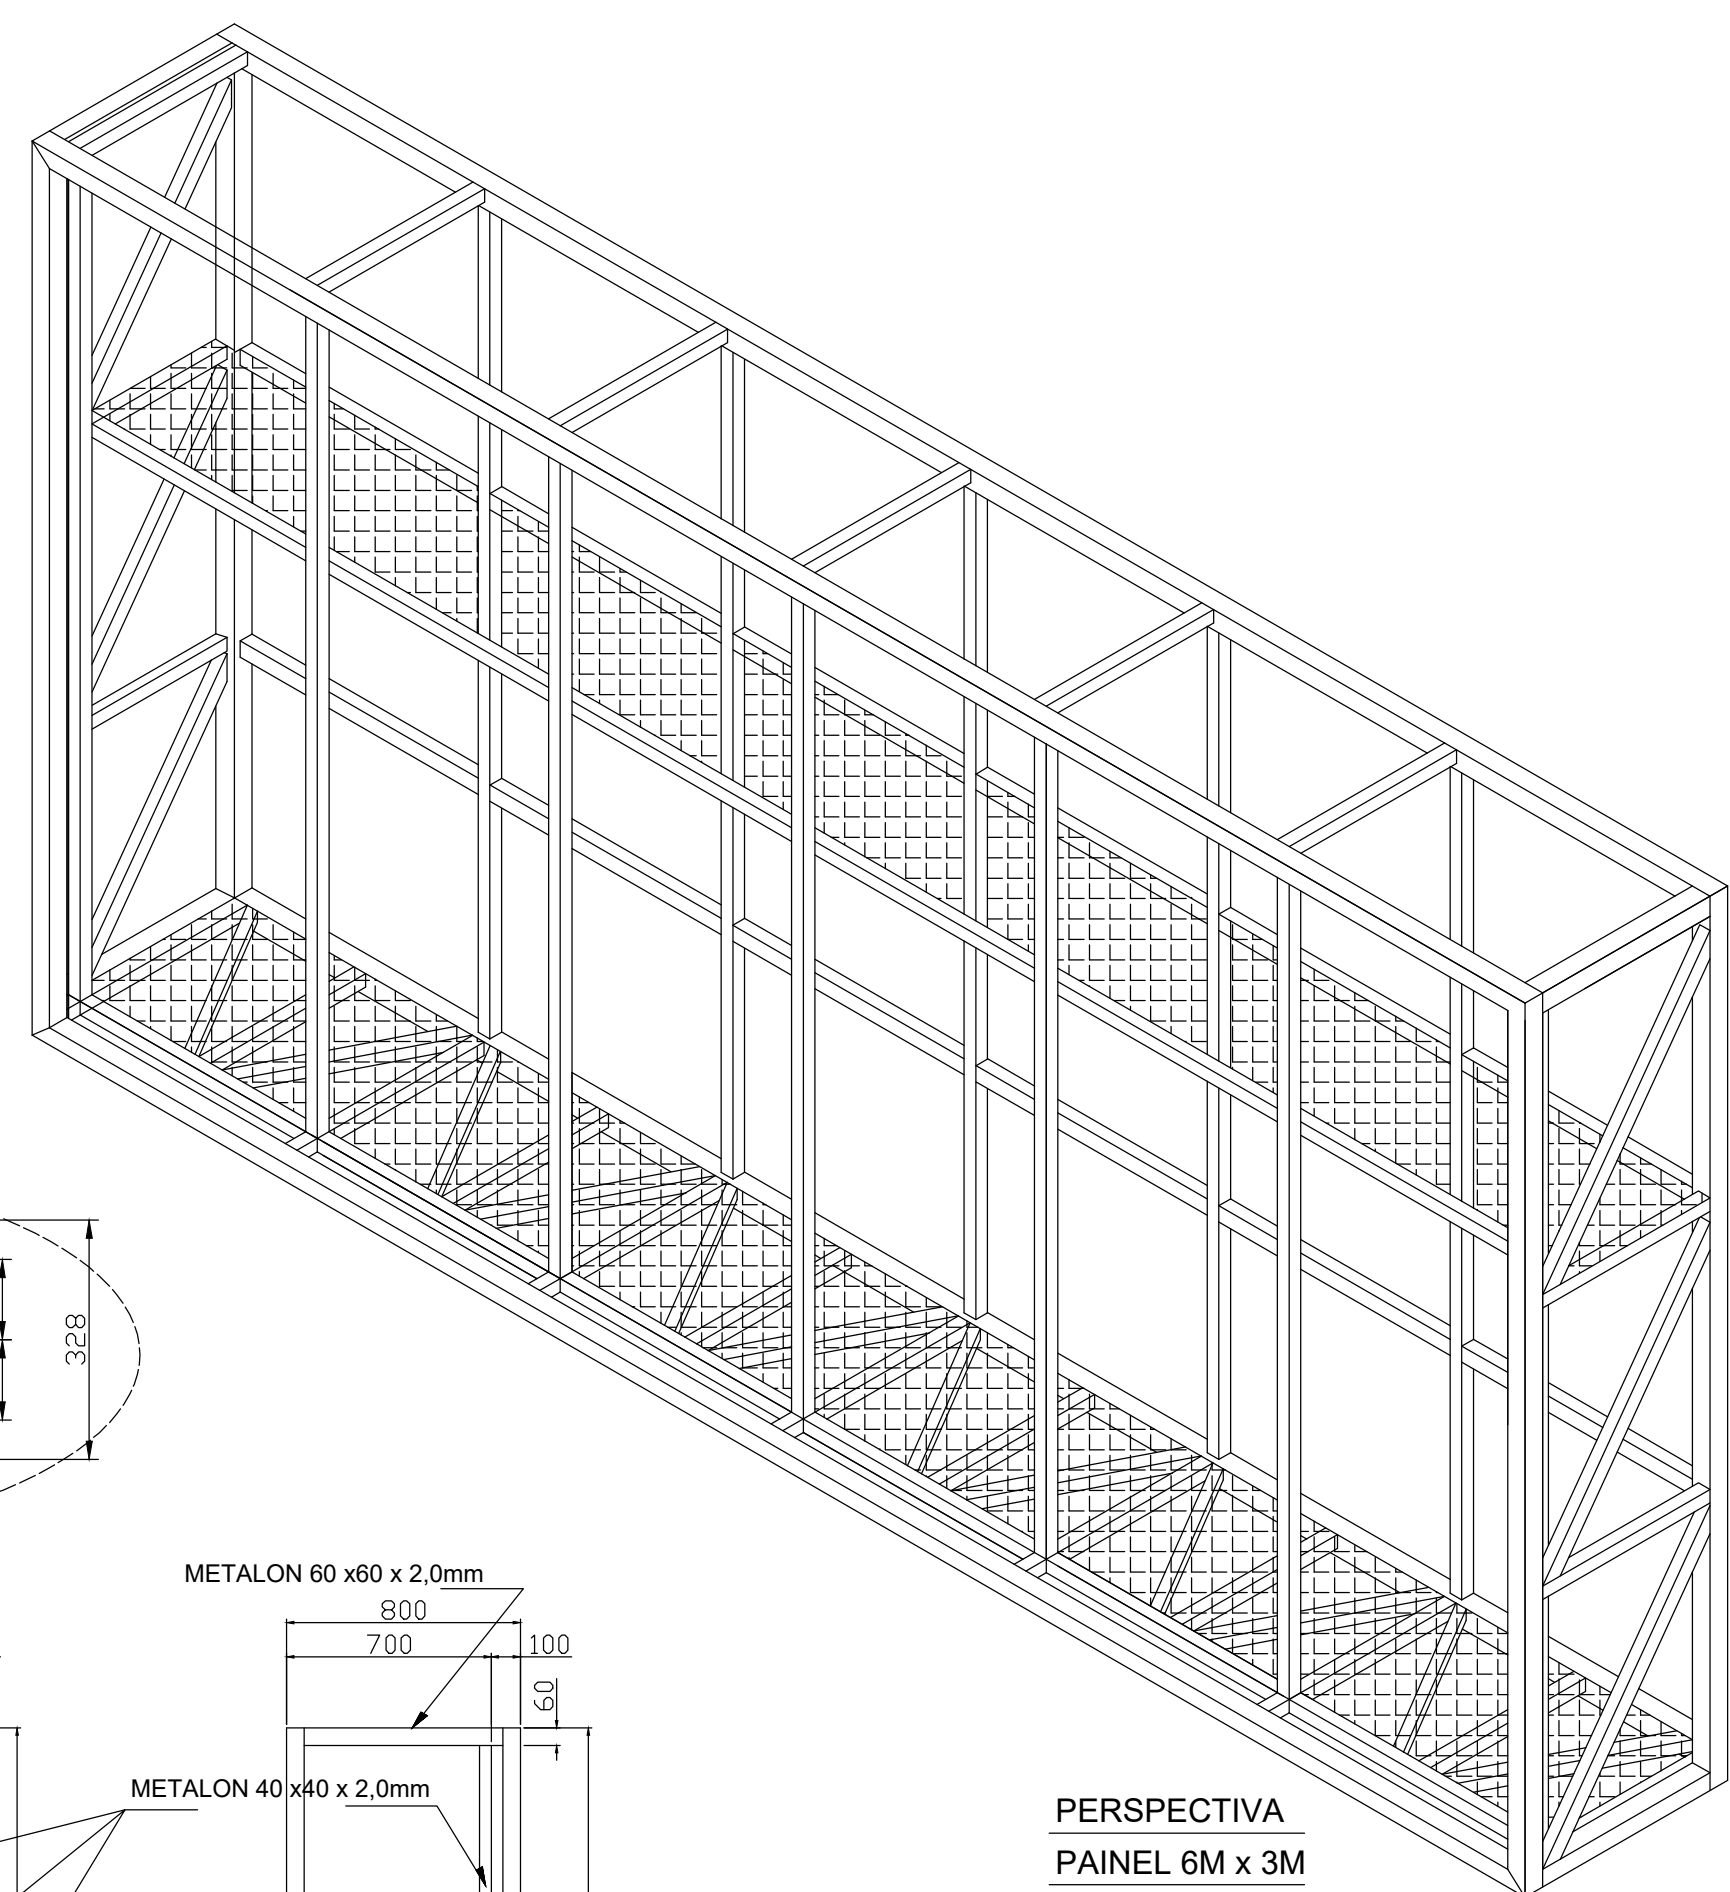
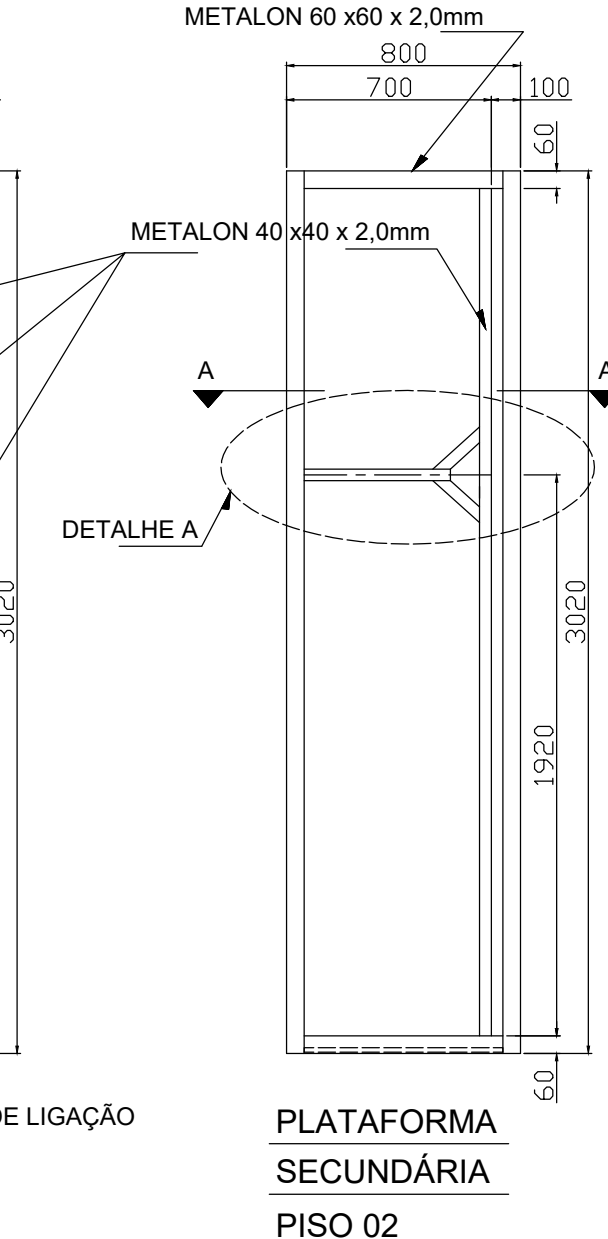
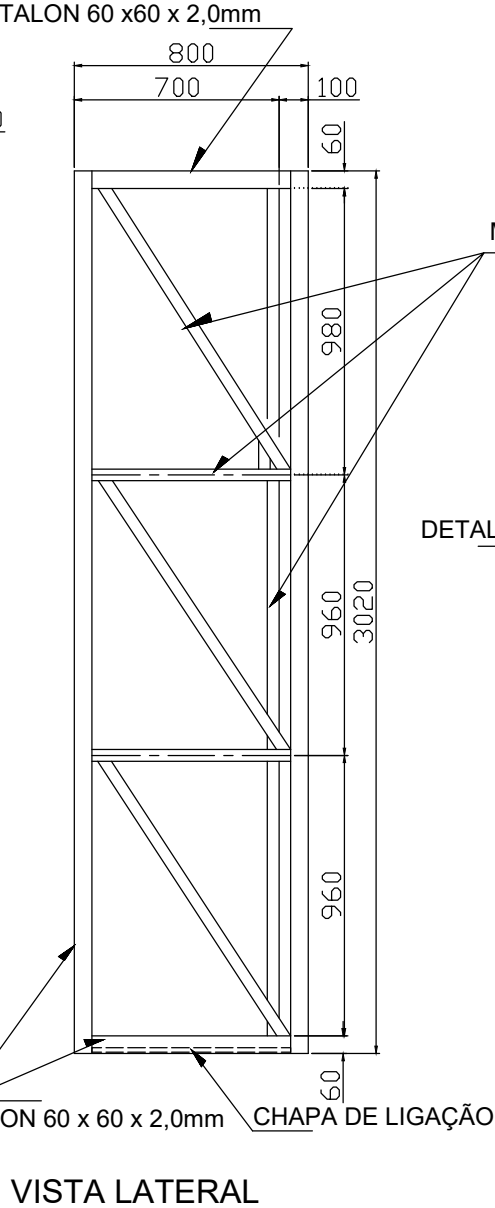
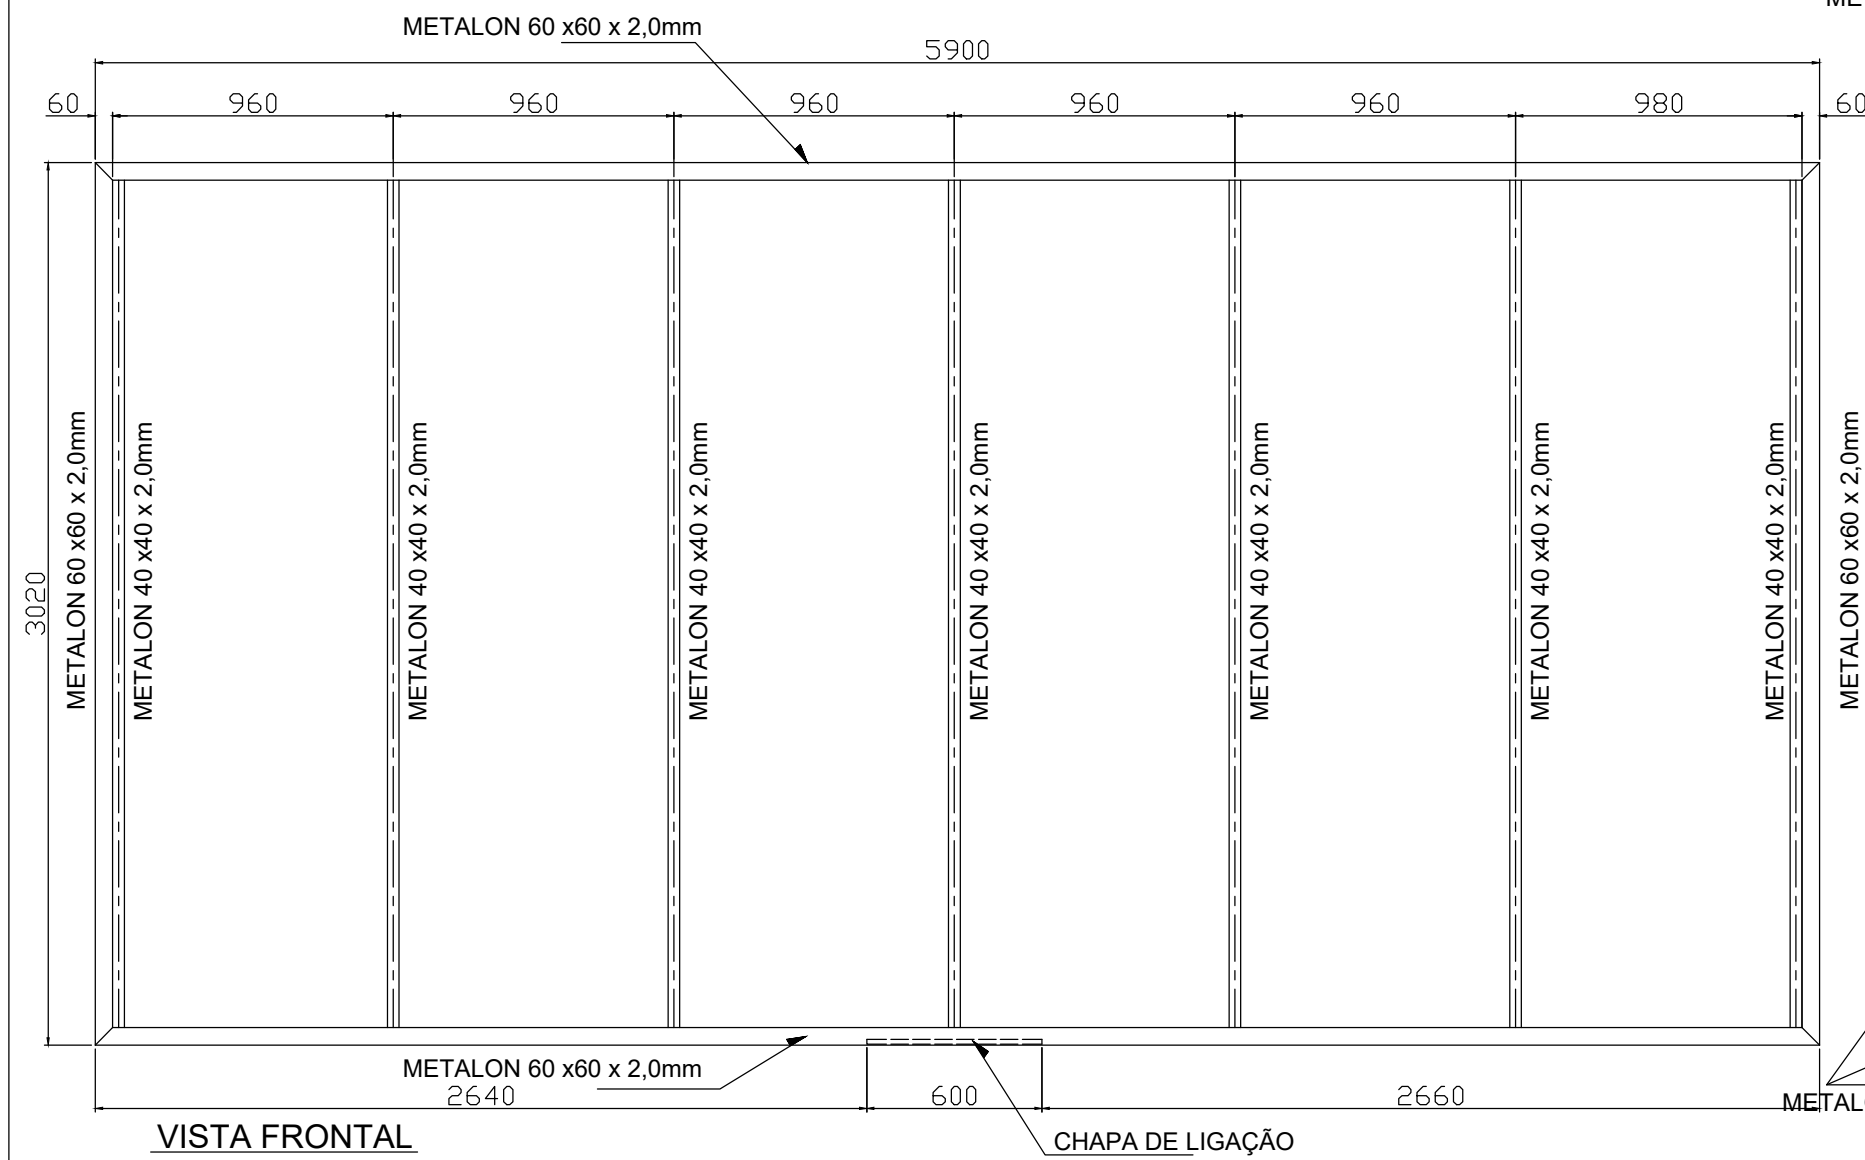
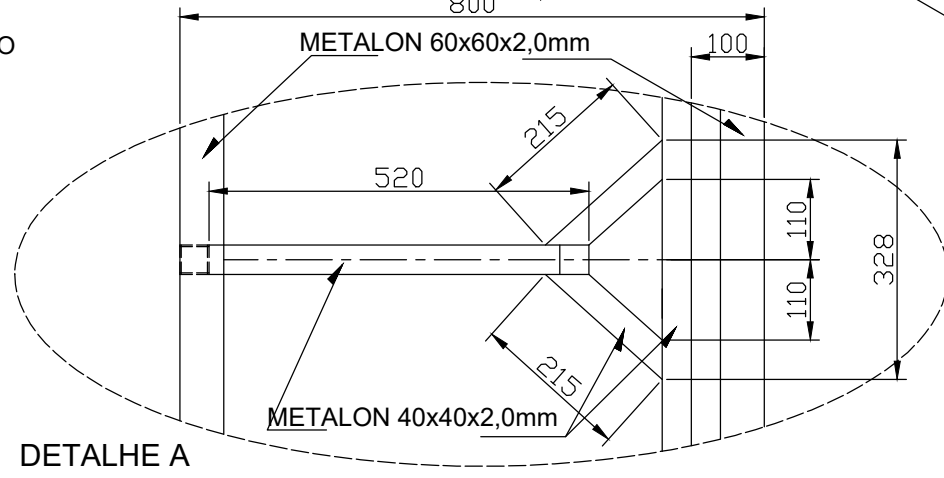
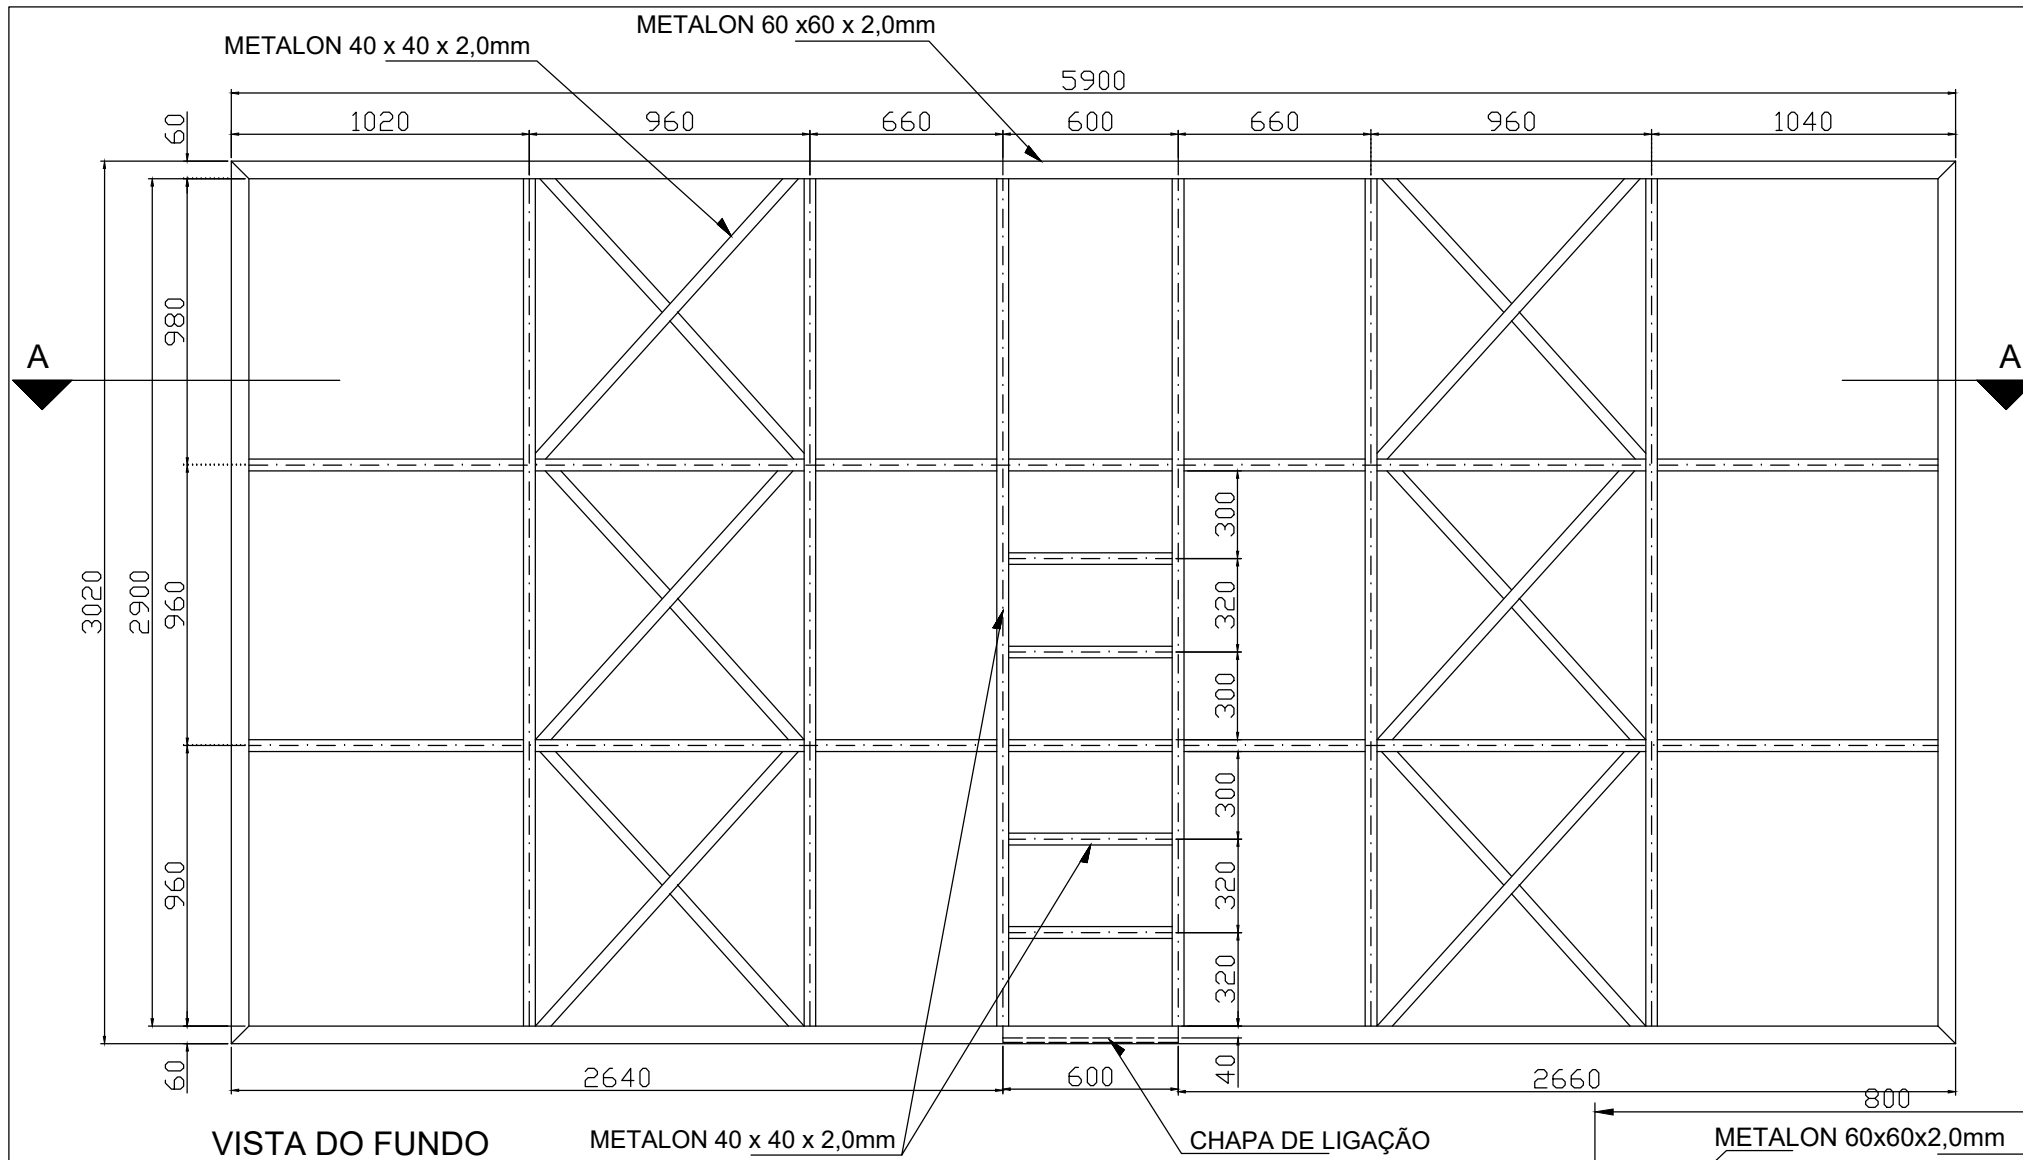
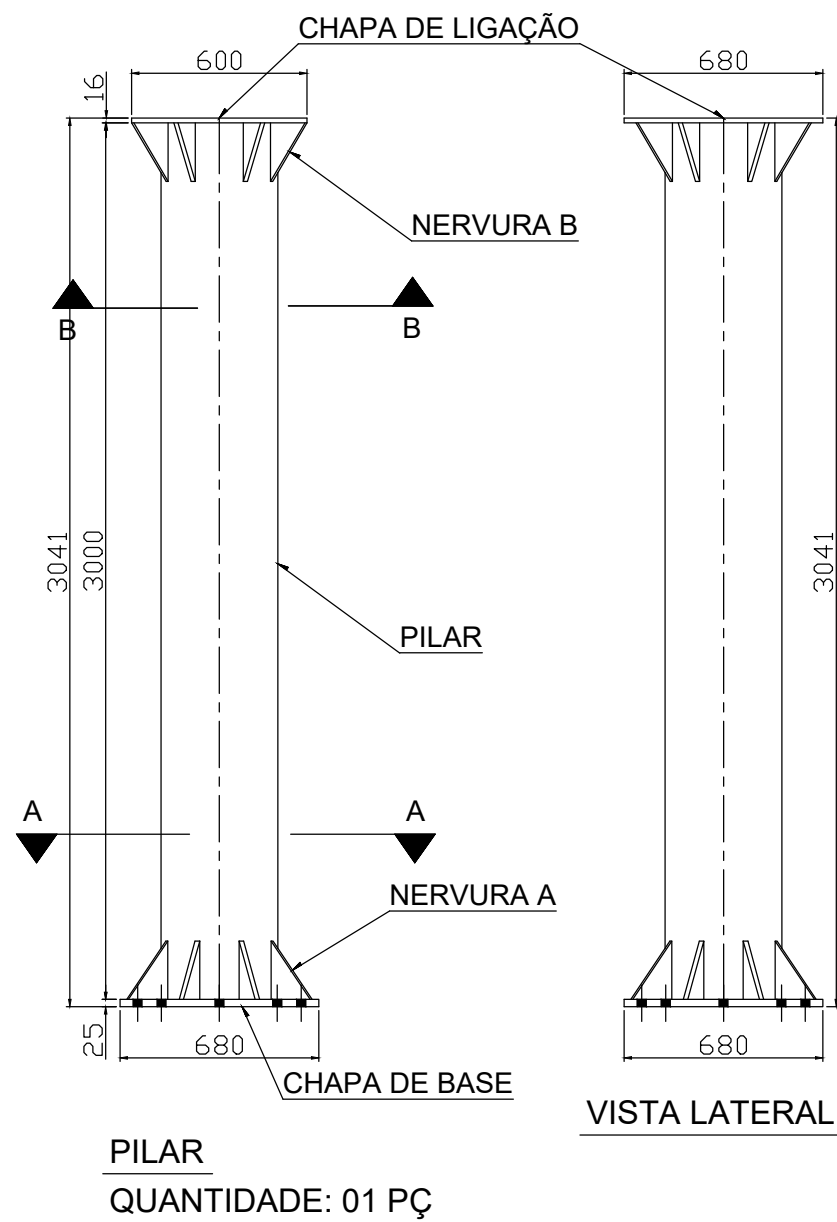
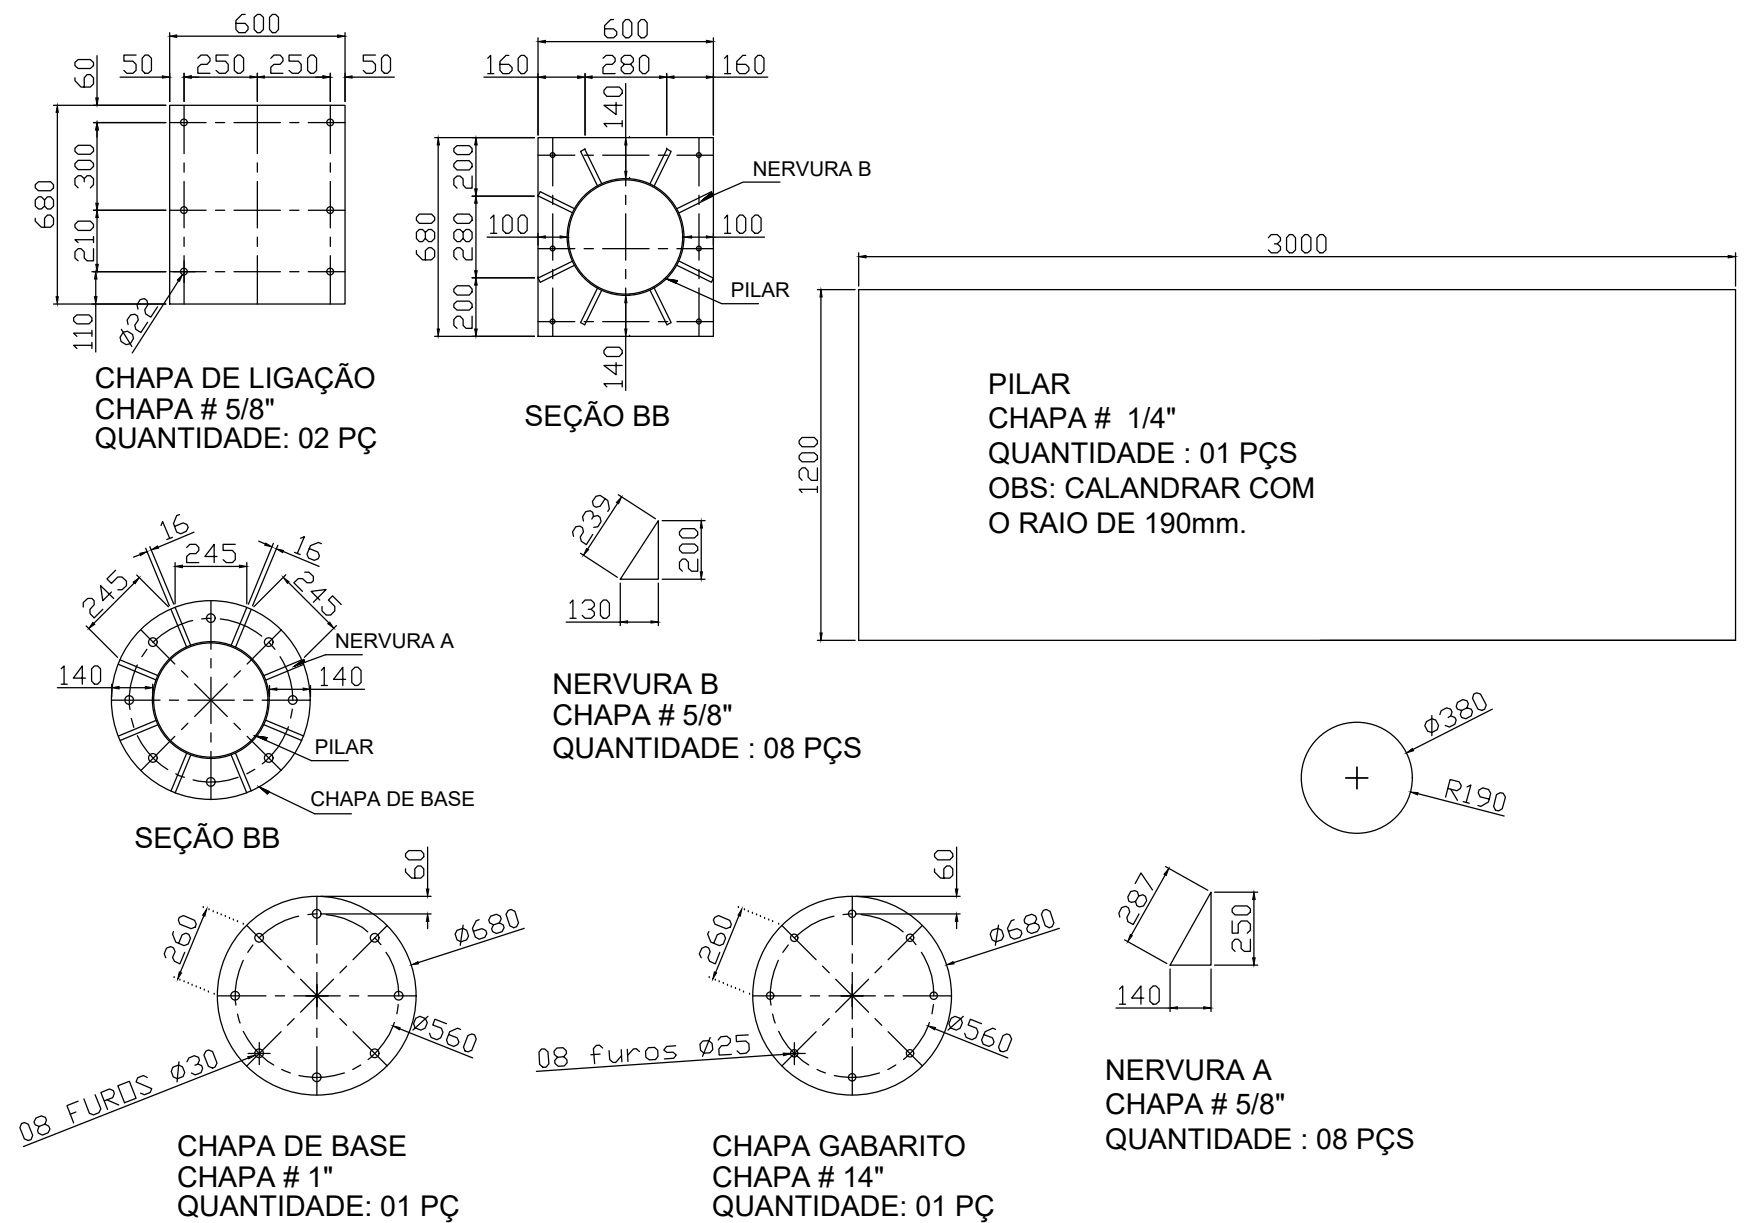
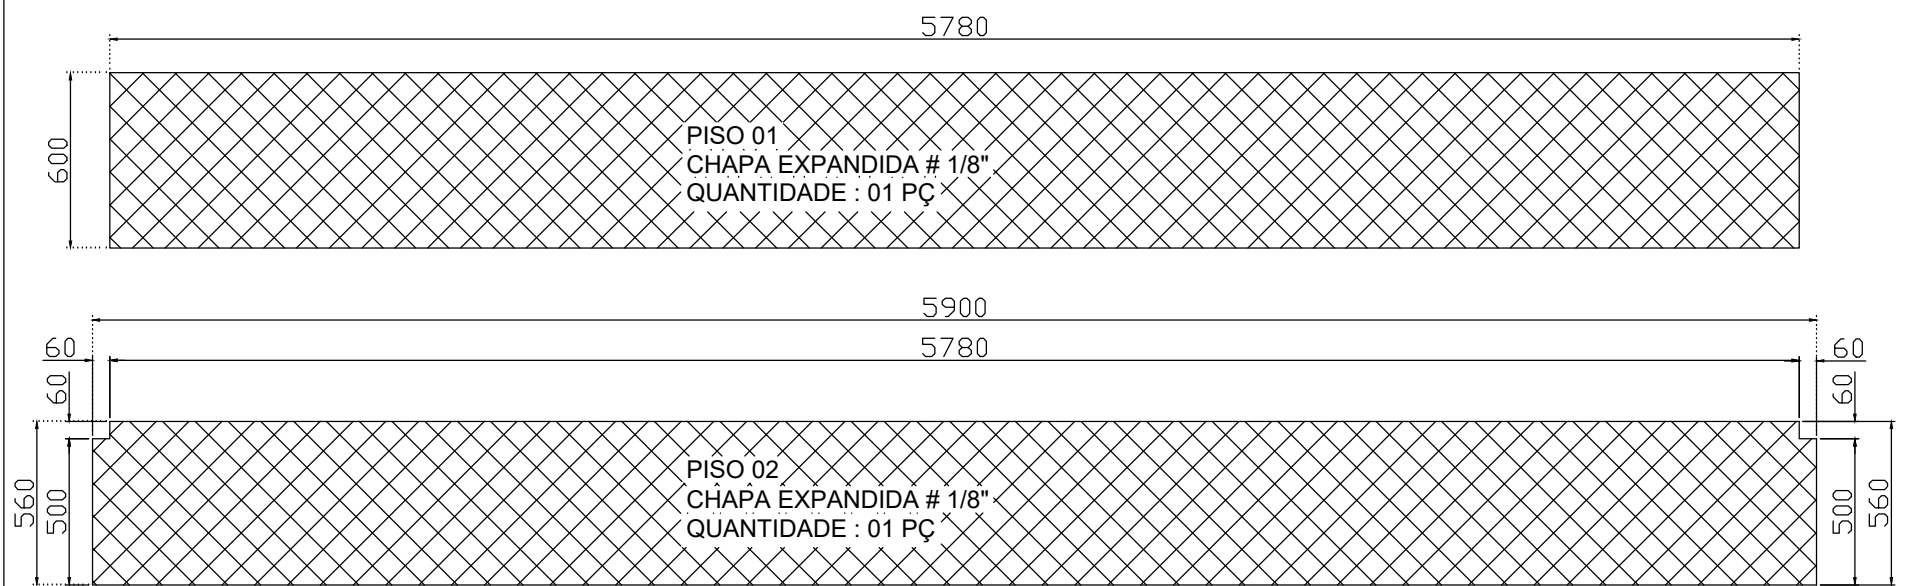


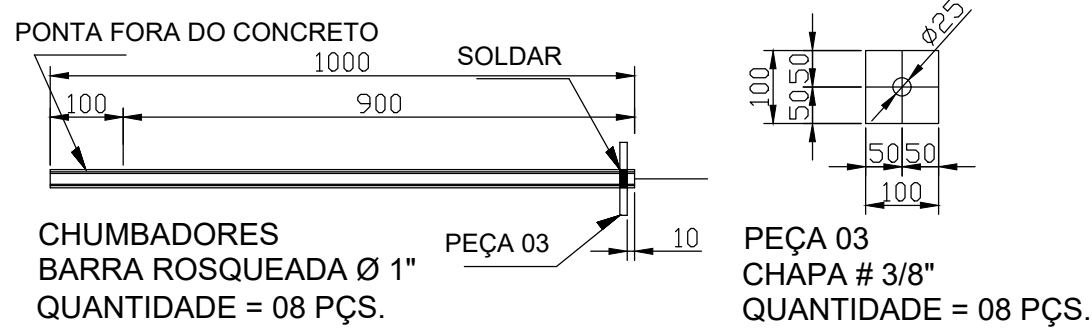

PERSPECTIVA
PAINEL 6M x 3M

NOTAS: MEDIDAS EM MILIMETRO;				
1				
0	INICIAL	F.G.S		19/07/23
N*	DESCRIÇÃO	DES.	RESP.	DATA
LED EXPERT				
PROJETO SOMENTE PARA ORÇAMENTO NÃO UTILIZAR PARA FABRICAÇÃO				
OBRA PAINEL 6x3 GB RENTAL OUTDOOR		Data: 19-07-2023		Desenhista: FABIAN
CONTÉM: PROJETO DE ESTRUTURA METÁLICA				
ESCALA IND.	PRANCHA 01	REGISTRO CREA.:	N° LED EXPERT: 148-2023-07-FL01	FORMATO: A2 REVISÃO: 0

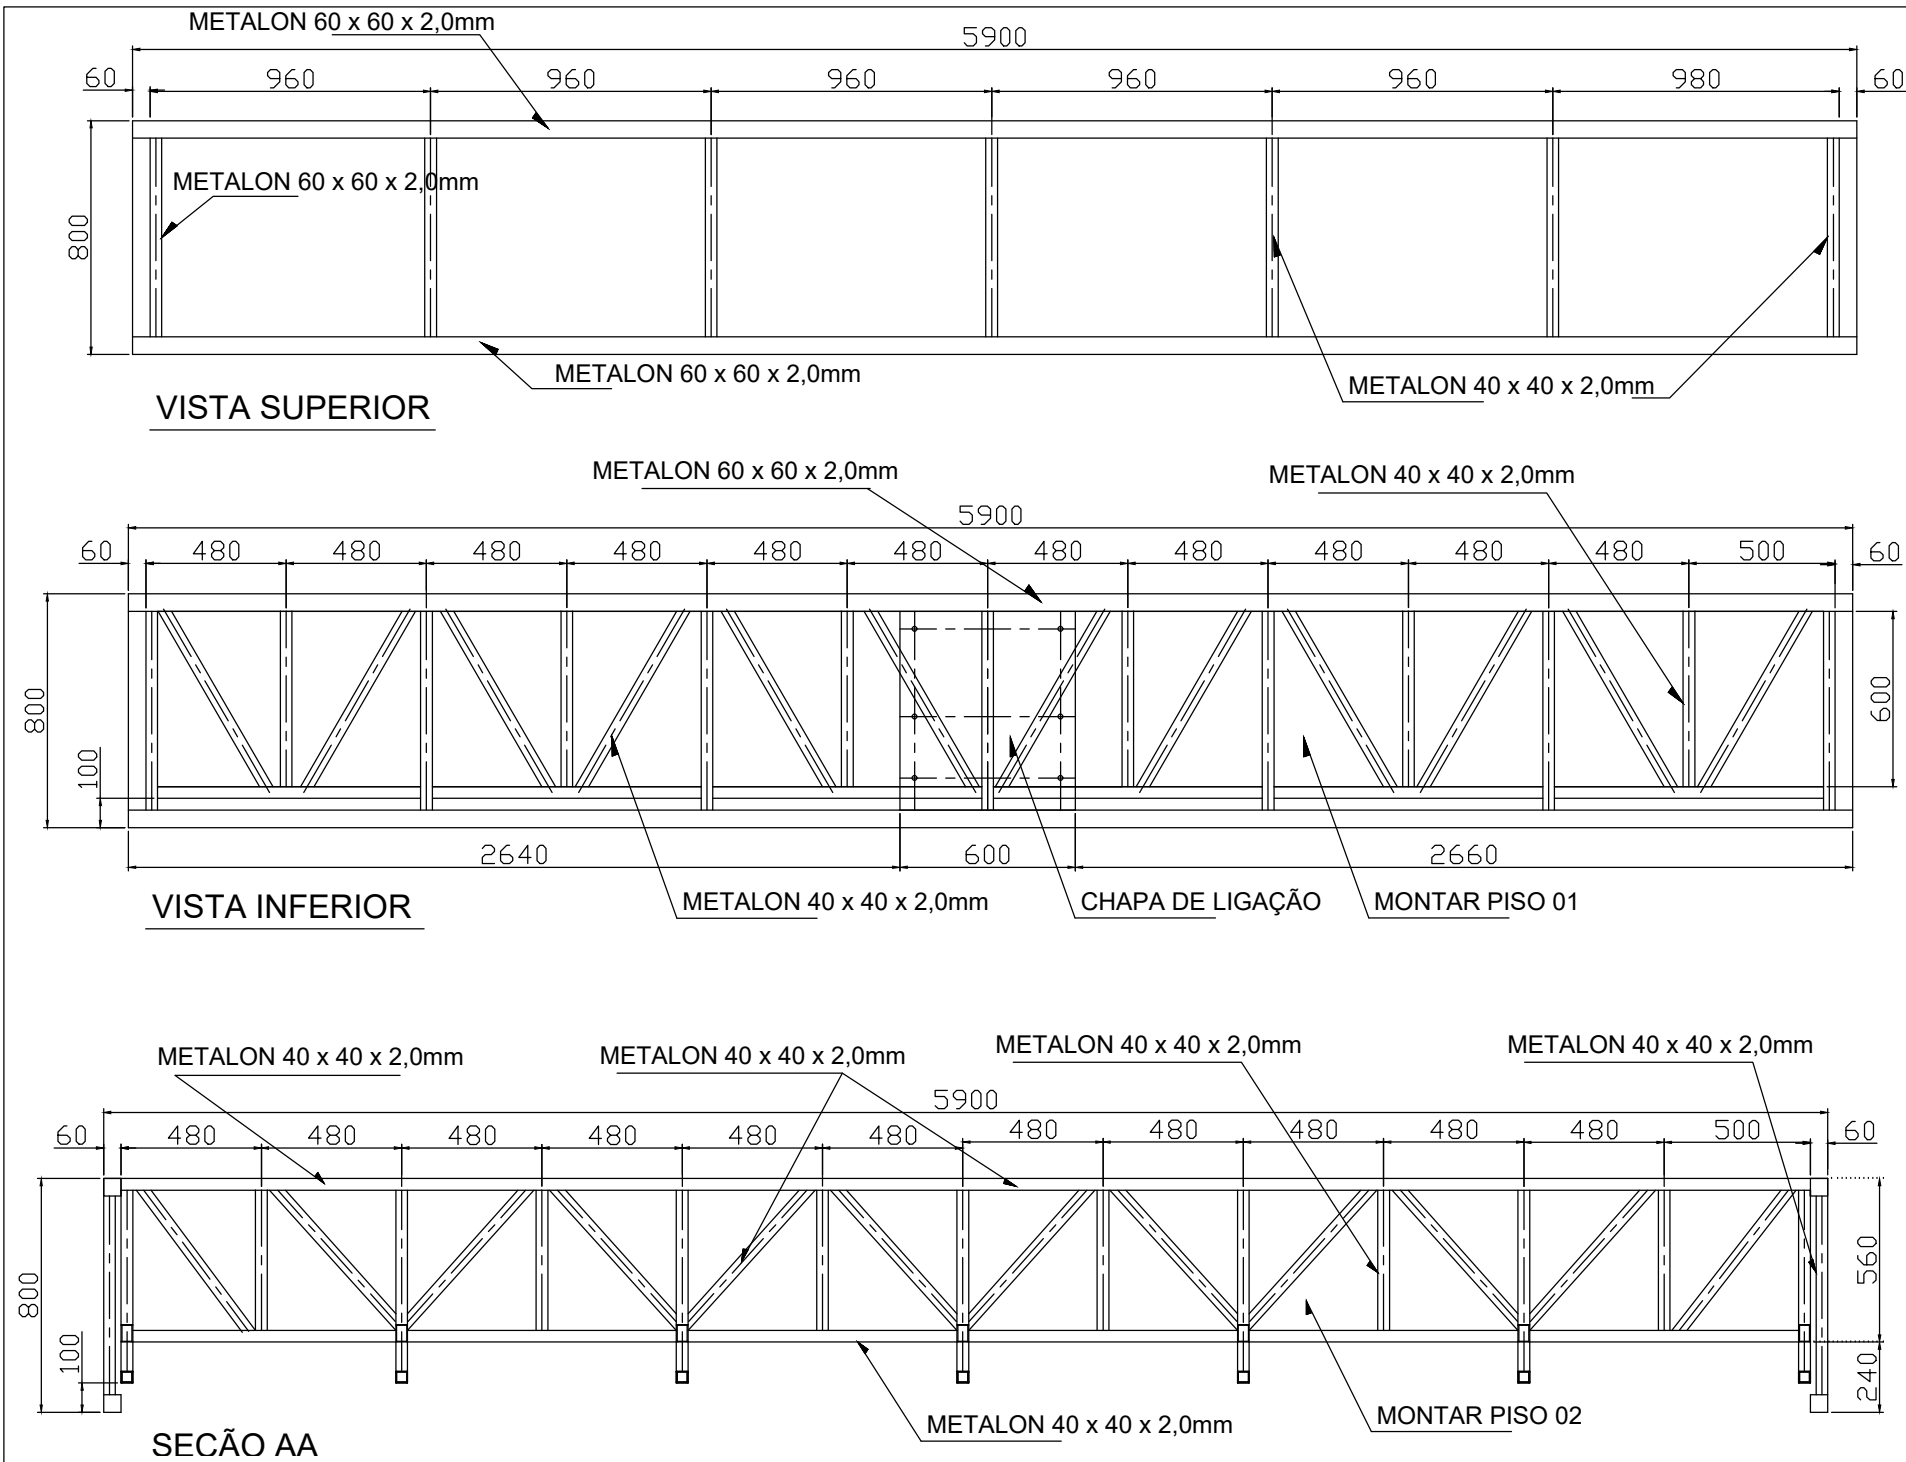

LISTA DE MATERIAIS						
Cliente: CIDADE DE CAMPINAS				DATA: 19/07/2023		
Obra: PAINEL 6x3 GB RENTAL OUTDOOR						
	ESTRUTURA METÁLICA					
	DESCRIÇÃO	COMPR.	UNID.	QUANT.	PESO UNIT.	PESO TOTAL.
01	METALON 60x60x2,0mm	6000mm	PÇS	07	21,69 KG	152,00 KG
02	METALON 40x40x2,0mm	6000mm	PÇS	22	14,5 KG	319,00 KG
03	CHAPA BASE # 1" x 680mm	680mm	PÇS	01	196,00 KG/M2	91,00 KG
04	CHAPA DE LIGAÇÃO # 5/8" x 600mm	680mm	PÇS	02	125,44 KG/M2	102,00 KG
05	CHAPA NERVURA A # 5/8" x 140mm	250mm	PÇS	08	125,50 KG/M2	35,00 KG
06	CHAPA NERVURA B # 5/8" x 130mm	200mm	PÇS	08	125,50 KG/M2	26,00 KG
07	CHAPA PILAR # 1/4" x 1200mm	3000mm	PÇS	01	49,39 KG/M2	177,80 KG
08	CHAPA EXPANDIDA # 1/8" x 600mm (PISO 01)	5780mm	PÇS	01	4,2 KG/M2	14,00 KG
09	CHAPA EXPANDIDA # 1/8" x 560mm (PISO 02)	5900mm	PÇS	01	4,2 KG/M2	15,00 KG
10	CHAPA # 14 x 680mm (GABARITO)	680mm	PÇS	01	16,00 KG/M2	7,40 KG
11	BARRA ROSQUEADA Ø 1"	1000mm	PÇS	08	3,98 KG	31,84 KG
12	CHAPA # 3/8" x 100mm (PEÇA 03)	100mm	PÇS	08	74,48 KG/M2	6,00 KG
				PESO TOTAL GERAL : 977,04 KG		

NOTAS: MEDIDAS EM MILIMETRO;					
0	INICIAL	F.G.S		19/07/23	
N°	DESCRIÇÃO	DES.	RESP.	DATA	
LED EXPERT					
PROJETO SOMENTE PARA ORÇAMENTO NÃO UTILIZAR PARA FABRICAÇÃO					
OBRA PAINEL 6x3 GB RENTAL OUTDOOR		Data: 19-07-2023	Desenhista: FABIAN		
CONTÉM: PROJETO DE ESTRUTURA METÁLICA					
ESCALA IND.	PRANCHA 02	REGISTRO CREA.:	N° LED EXPERT: 148-2023-07-FL02	FORMATO: A2	REVISÃO 0