




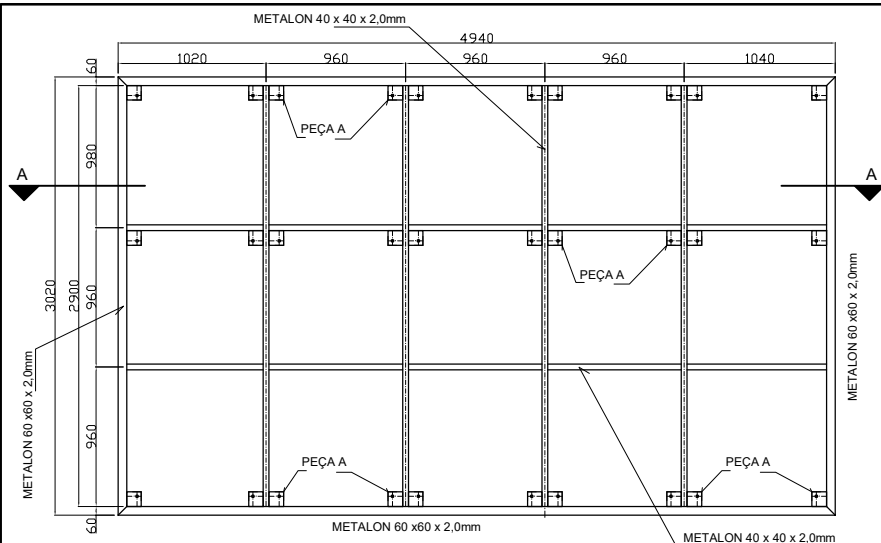


VISTA DO FUNDO

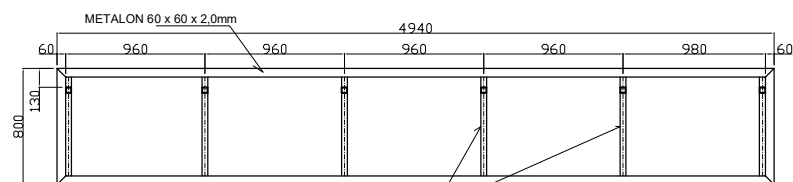

VISTA SUPERIOR


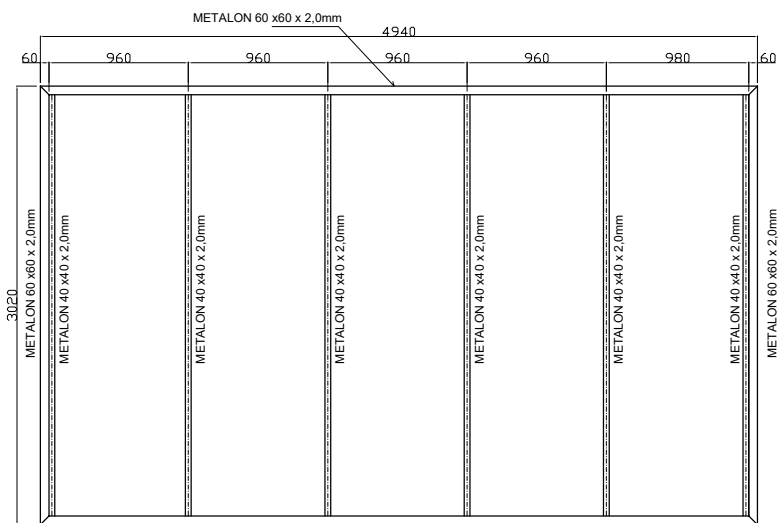


VISTA FRONTAL

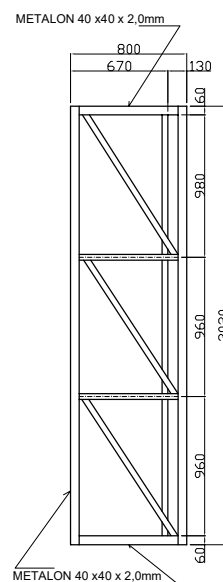


VISTA LATERAL

PERSPECTIVA
PAINEL 5M x 3M

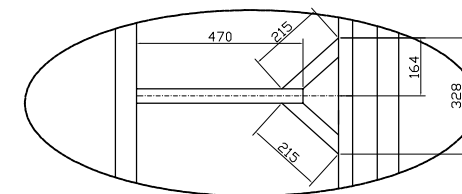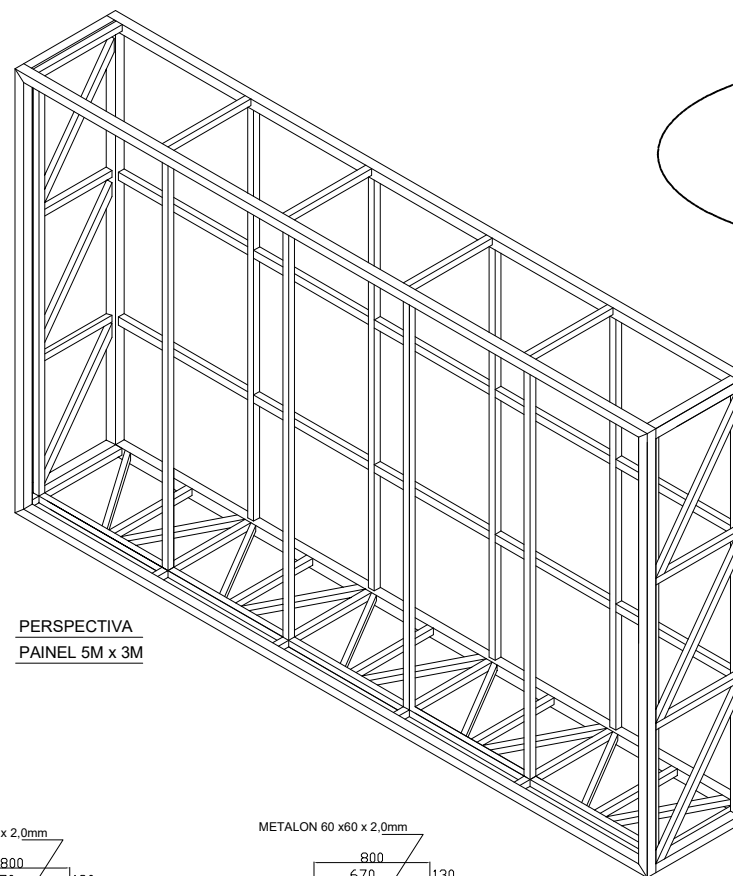

SEÇÃO BB

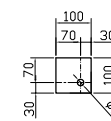


PEÇA A
CHAPA # 3/8"
QUANTIDADE : 30 PÇS

NOTAS: MEDIDAS EM MILIMETRO;



4				
3				
2				
1				
0	INICIAL	F.G.S		30/06/22
N°	DESCRIÇÃO	DES.	RESP.	DATA

LED EXPERT

PROPRIETÁRIO HENRIQUE				
ENDEREÇO: RUA RUI MANOEL FRANCO AMARAL N 433 BAIRRO CIDADE JARDIM IGARAPÉ MG				
RESPONSÁVEL: HENRIQUE				
OBRA	PAINEL 5 x 3	Data:	30-06-2022	Desenhista: FABIAN
CONTÉM: PROJETO DE ESTRUTURA METÁLICA				
ESCALA	SE	RT.:	N° LED EXPERT:	FORMATO: REVISÃO
IND.	--	--	05-2022-06-FL-01	A2 0

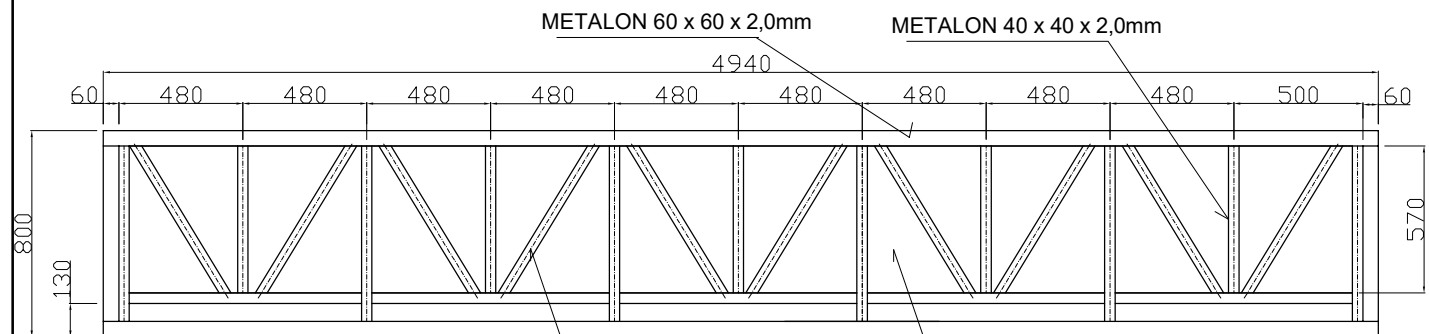

VISTA INFERIOR

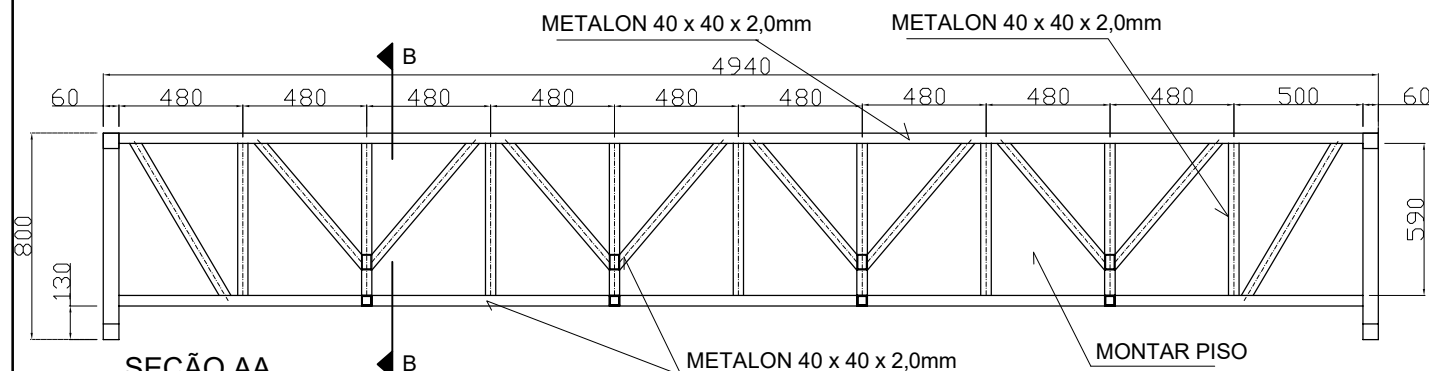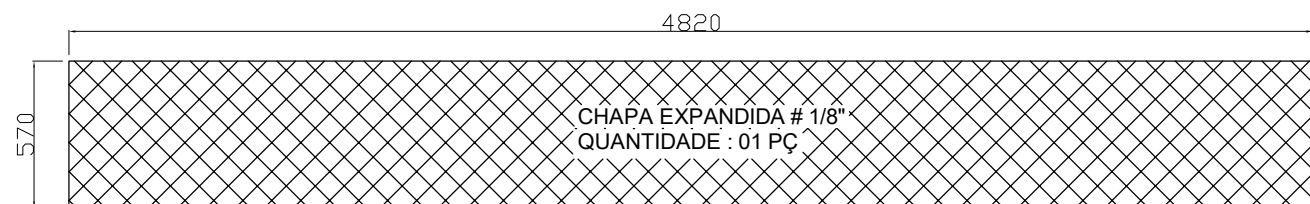

SEÇÃO AA


LISTA DE MATERIAIS						
Cliente: HENRIQUE				DATA: 29/06/2022		
Obra: PAINEL 5x3 GB AÇO OUTDOOR						
ESTRUTURA METÁLICA						
	DESCRIÇÃO	COMPR.	UNID.	QUANT.	PESO UNIT.	PESO TOTAL
01	METALON 60x60x2,0mm	6000mm	PÇS	06	21,69 KG	130,00 KG
02	METALON 40x40x2,0mm	6000mm	PÇS	14	14,5 KG	203,00 KG
03	CHAPA # 3/8" x 100 (PEÇA A)	100mm	PÇS	24	74,48 KG/M2	18,00 KG
04	CHAPA EXPANDIDA # 1/8" x 590mm(PISO)	4820mm	PÇS	01	4,2 KG/M2	12,00 KG
05	CHAPA EXPANDIDA # 1/8" x 570mm(PISO)	4820mm	PÇS	01	4,2 KG/M2	11,50 KG
06	PERFIL UE 100x50x17x2,0mm	6000mm	PÇS	14	19,62 KG	275,00 KG
07	CHAPA # 3/8" x 60 (PEÇA C)	60mm	PÇS	06	74,48 KG/M2	1,60 KG
08	CHAPA # 3/8" x 60 (PEÇA E)	70mm	PÇS	24	74,48 KG/M2	7,50 KG
09	CANTONEIRA L 3" x 3" x 3/8" (PEÇA B)	2000mm	PÇS	01	10,80 KG/M2	21,60 KG
				PESO TOTAL GERAL : 680,20 KG		

NOTAS: MEDIDAS EM MILIMETRO;


4				
3				
2				
1				
0	INICIAL	F.G.S		30/06/22
Nº	DESCRIÇÃO	DES.	RESP.	DATA

LED EXPERT


PROPRIETÁRIO HENRIQUE				
ENDEREÇO: RUA RUI MANOEL FRANCO AMARAL N 433 BAIRRO CIDADE JARDIM IGARAPÉ MG				
RESPONSÁVEL: HENRIQUE				
OBRA	PAINEL 5 x 3	Data:	30-06-2022	Desenhista: FABIAN
CONTÉM: PROJETO DE ESTRUTURA METÁLICA				
ESCALA	SE	R.T.:	Nº LED EXPERT:	FORMATO: REVISÃO
IND.	--	--	05-2022-06-FL-02	A2 0

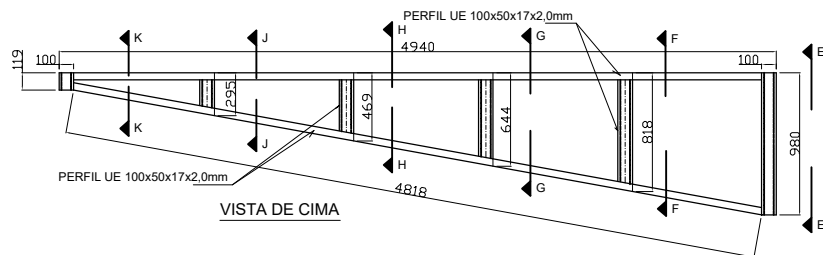


VISTA DE CIMA

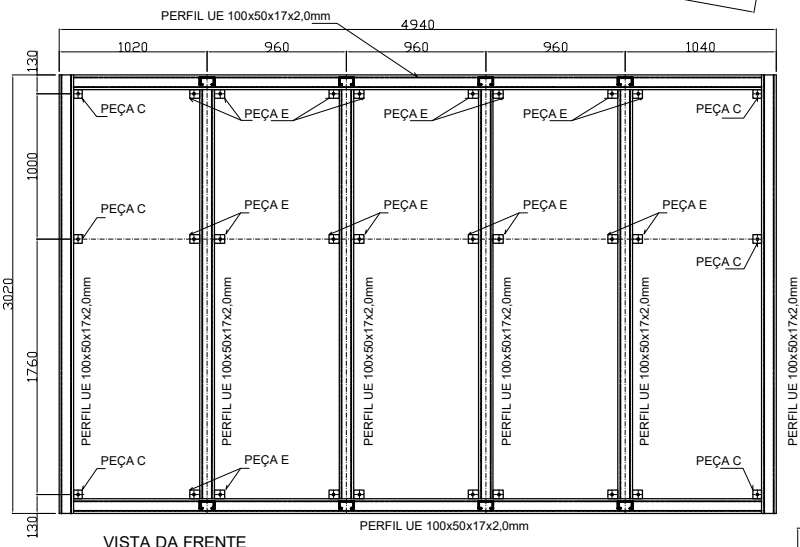


VISTA DA FRENTE

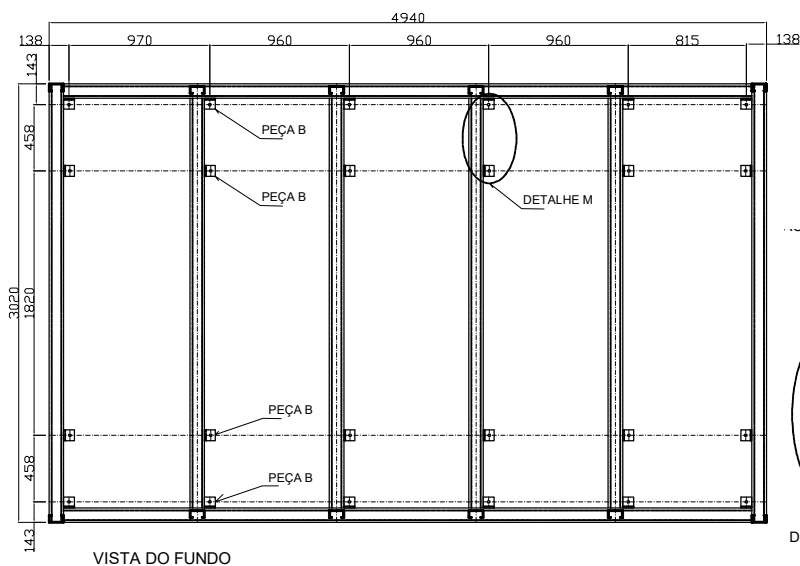

VISTA DO FUNDO

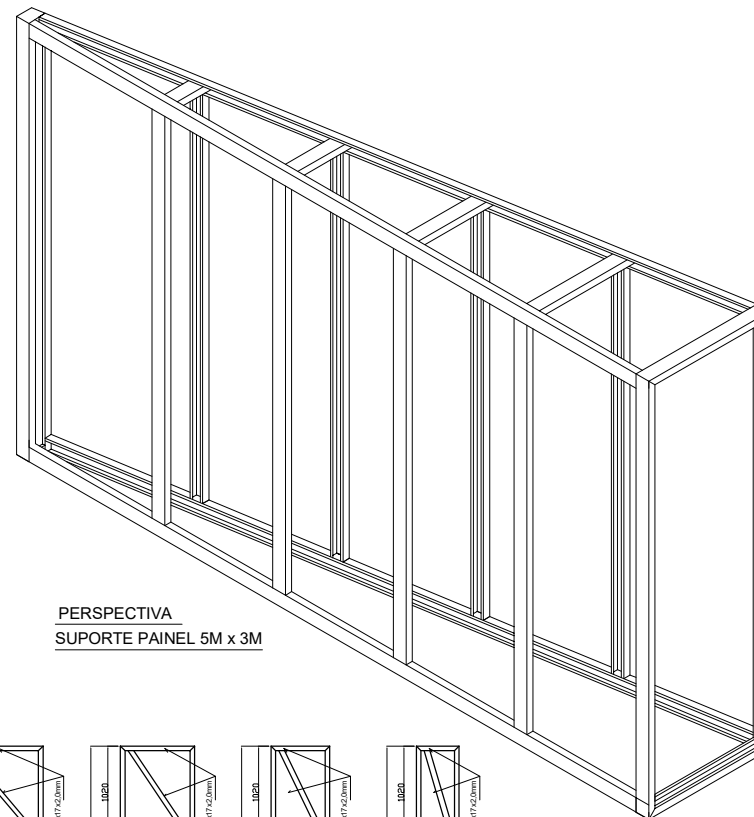

PERSPECTIVA
SUPORTE PAINEL 5M x 3M

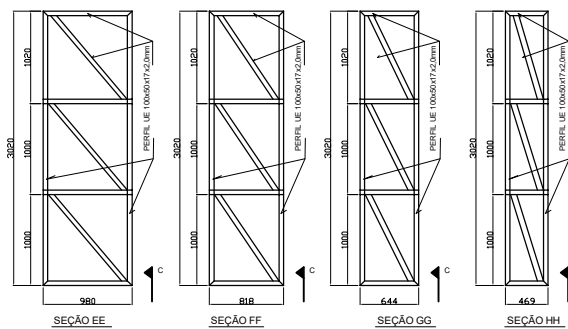


SEÇÃO EE


SEÇÃO FF

SEÇÃO GG

SEÇÃO HH

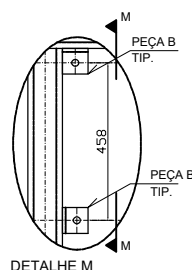


DETALHE M

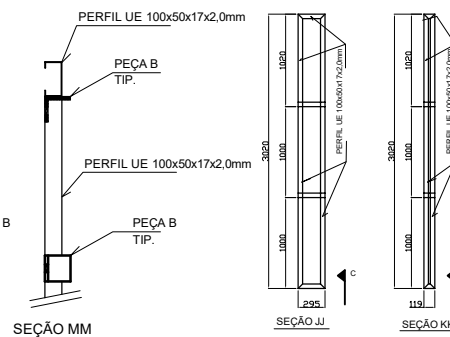


SEÇÃO MM

SEÇÃO JJ


SEÇÃO KK

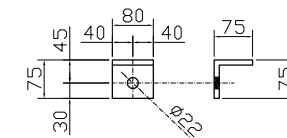

PEÇA B
CANTONEIRA L 3"x3" x 3/8"
QUANTIDADE : 24 PÇS

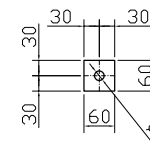

PEÇA C
CHAPA # 3/8"
QUANTIDADE : 06 PÇS

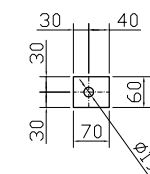

PEÇA E
CHAPA # 3/8"
QUANTIDADE : 24 PÇS

NOTAS: MEDIDAS EM MILIMETRO;

4				
3				
2				
1				
0	INICIAL	F.G.S		30/06/22
N°	DESCRIÇÃO	DES.	RESP.	DATA

LED EXPERT

PROPRIETÁRIO	HENRIQUE			
ENDEREÇO:	RUA RUI MANOEL FRANCO AMARAL N 433 BAIRRO CIDADE JARDIM IGARAPÉ MG			
RESPONSÁVEL:	HENRIQUE			
OBRA	SUPORTE PAINEL 5 x 3	Data:	30-06-2022	Desenhista:
				FABIAN
CONTÉM:	PROJETO DE ESTRUTURA METÁLICA			
ESCALA	SE	RT.	N° LED EXPERT:	FORMATO:
IND.	--	--	05-2022-06-FL-03	A2
				REVISÃO
				0