
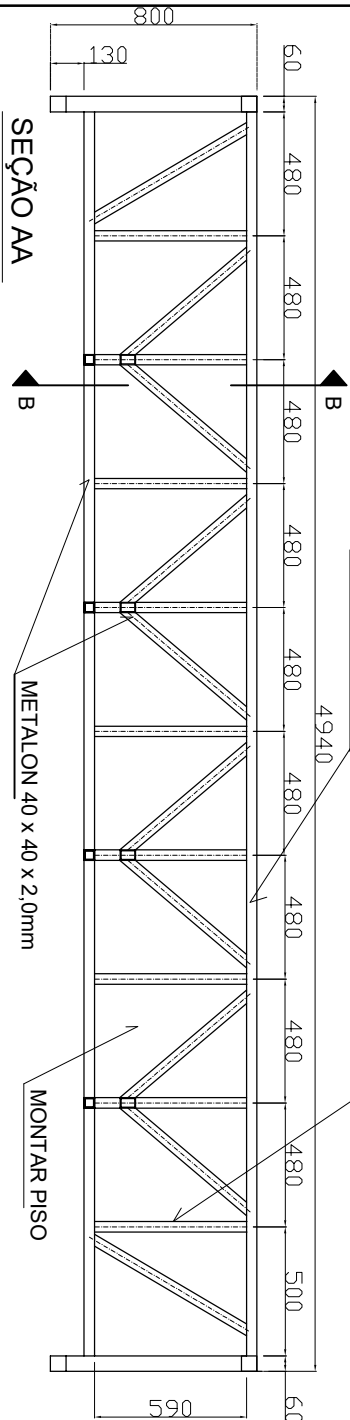
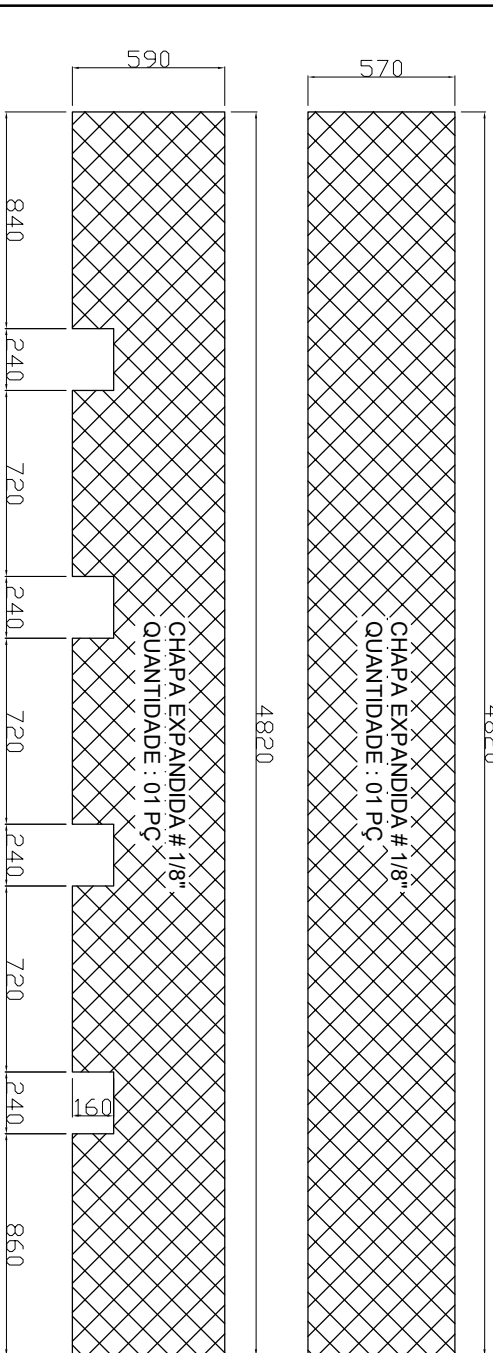


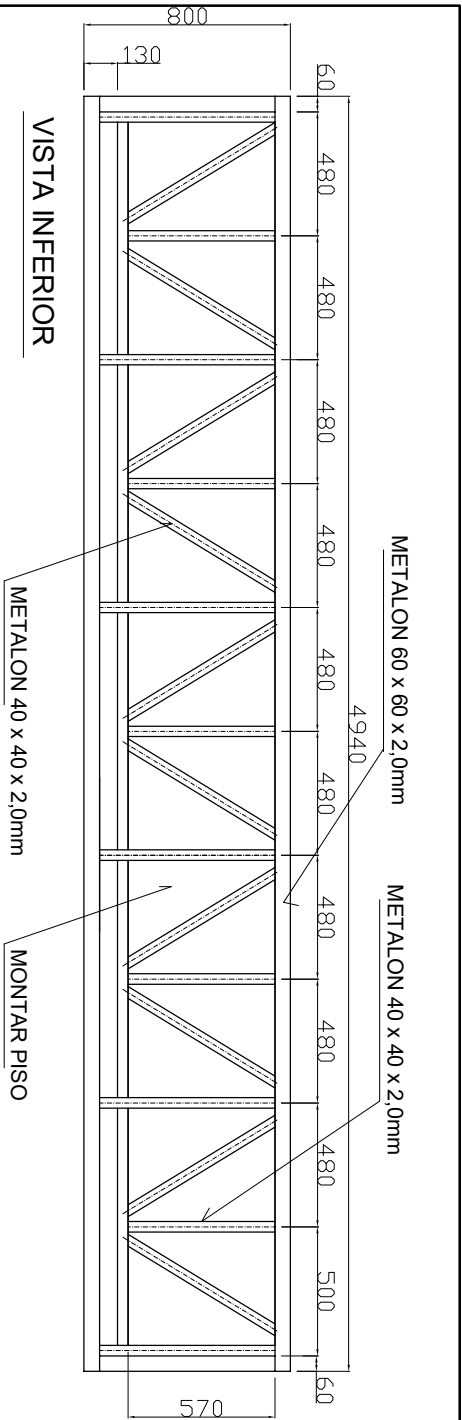

CLIENTE: HENRIQUE				
LISTA DE MATERIAIS				
Obra: PAINEL 5x3 GB AÇO OUTDOOR				
DATA: 29/06/2022				
ESTRUTURA METÁLICA				
UNID.	QUANT.	PESO UNIT.	PESO TOTAL	
01	6000mm	06	21,69 KG	130,00 KG
02	6000mm	14	14,5 KG	203,00 KG
03	100mm	24	74,48 KG/M2	18,00 KG
04	4820mm	01	4,2 KG/M2	12,00 KG
05	6000mm	14	19,62 KG	275,00 KG
06	60mm	06	74,48 KG/M2	1,60 KG
07	70mm	24	74,48 KG/M2	7,50 KG
08	2000mm	01	10,80 KG/M2	21,60 KG
PESO TOTAL GERAL : 680,20 KG				

NOTAS: MEDIDAS EM MILÍMETRO;

4				
3				
2				
1				
0	INICIAL	F.G.S		30/06/22
Nº	DESCRIÇÃO	DES.	RESP.	DATA
LED EXPERT				
PROPRIETARIO				
HENRIQUE				
ENDERECO:				
RUA RUI MANOEL FRANCO AMARAL N 433 BAIRRO CIDADE JARDIM IGARAPÉ MG				
RESPONSÁVEL:				
HENRIQUE				
OBRA				
PAINEL 5 x 3				
Data:				
30-06-2022				
Desenhista:				
FABIAN				
CONTEN:				
PROJETO DE ESTRUTURA METÁLICA				
ESCALA	SE	RT:	Nº LED EXPERT	FORMATO
IND.	--	--	05-2022-06-FL-02	A2
				0