

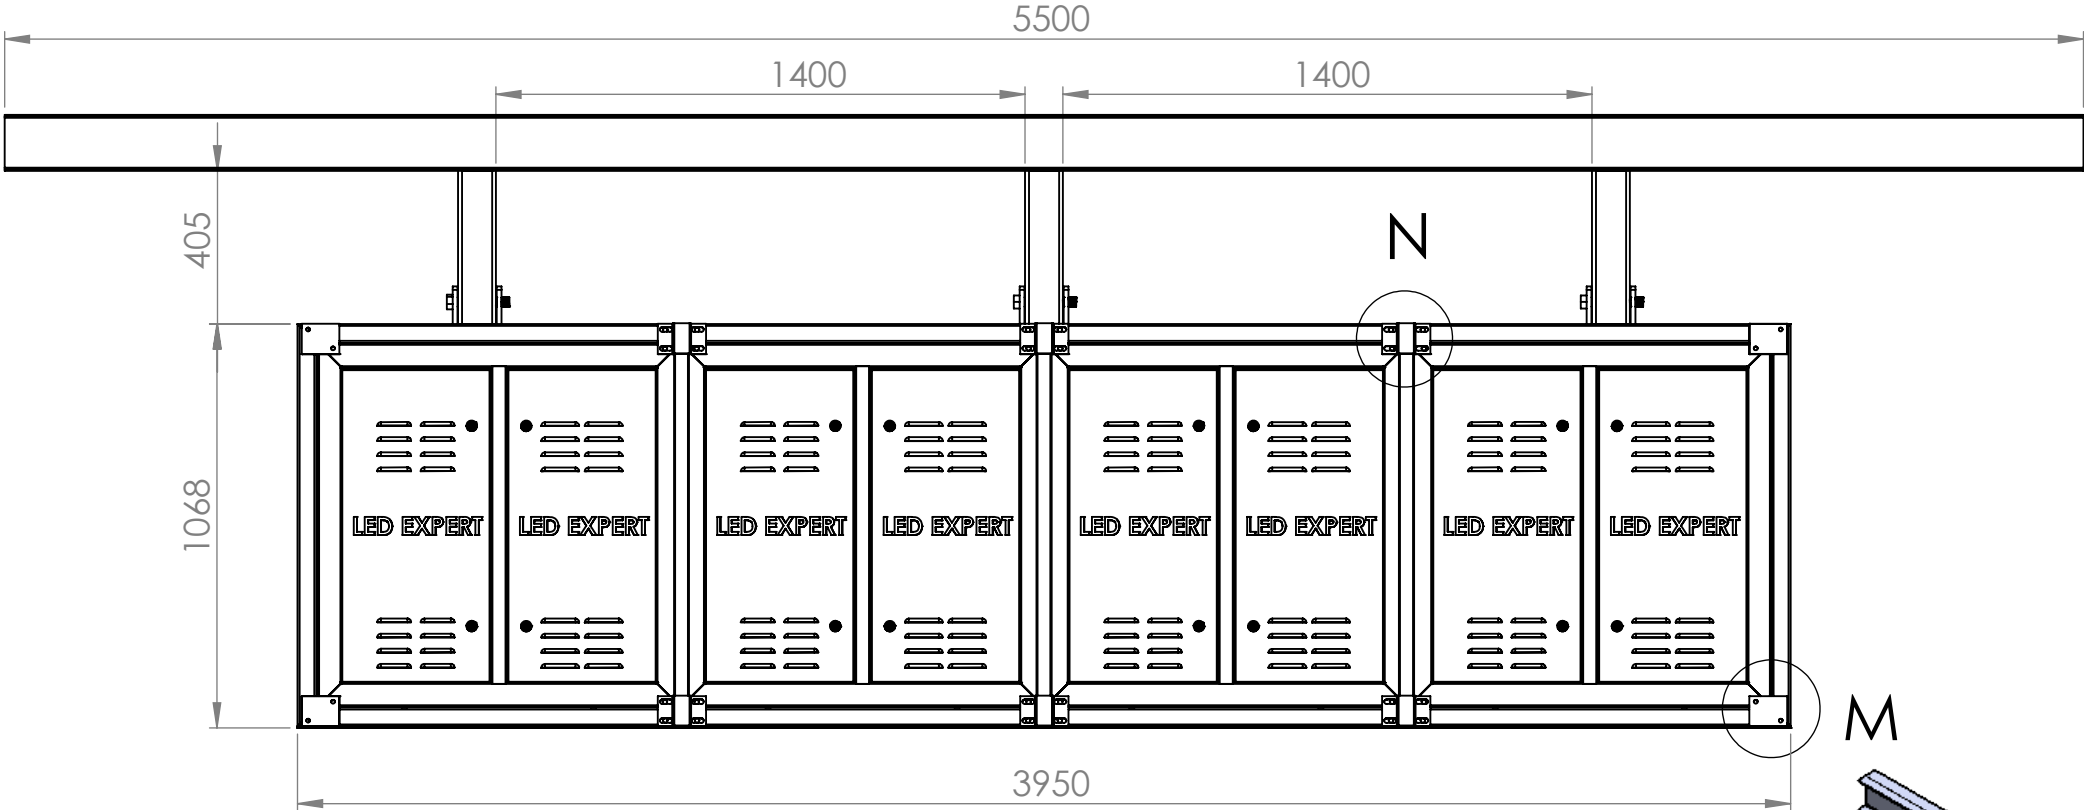


DETALHE M
ESCALA 1 : 5

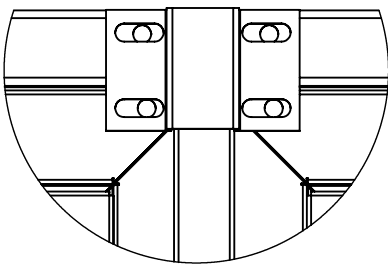

DETALHE N
ESCALA 1 : 5

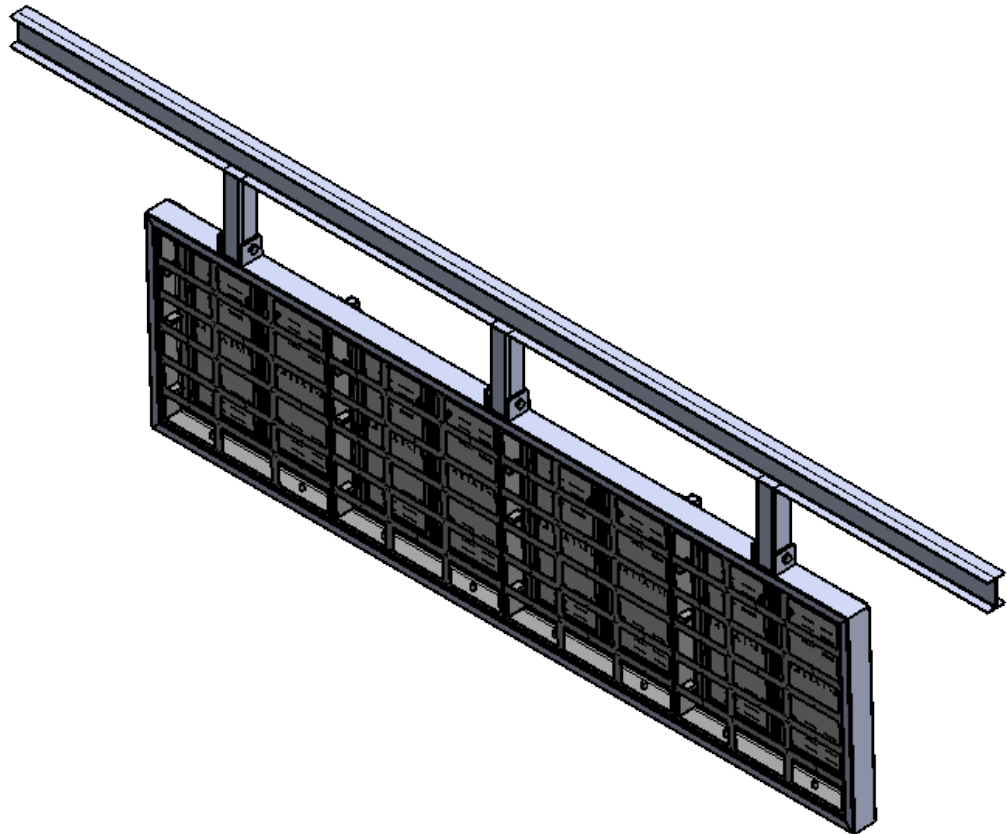

Nº DO ITEM	Nº DA PEÇA	DESCRIÇÃO	QTD.
1	p0031-00	Estrutura	1
3	p0032-00	Suporte de fixar os gabinetes 1	6
4	parafuso	parafuso m25x120	3
5	Gabinetes	Gabinetes	3
9	p0033-00	Suporte de fixar os gabintes 2	4
10	p0036-00	Base para fixar o Painel	1

SE NÃO ESPECIFICADO: DIMENSÕES EM MILÍMETROS ACABAM. SUPERFÍCIE: TOLERÂNCIAS: LINEAR: ANGULAR:			ACABAMENTO: -			REBARBAR E QUEBRAR ARESTAS AGUDAS			NÃO MUDAR ESCALA DO DESENHO			LED EXPERT			
									Quant: 01						
TÍTULO: estrutura Posto de combustivel												DES. Nº P0026-00 A3			
NOME			ASSINATURA			DATA			MATERIAL: Aço carbono						
DESEN.			WilliamM												
VERIF.															
APROV.															
MANUF.															
QUALID															
PESO DO PAINEL: 38kg						ESCALA: 1:20			FOLHA 1 DE 1						