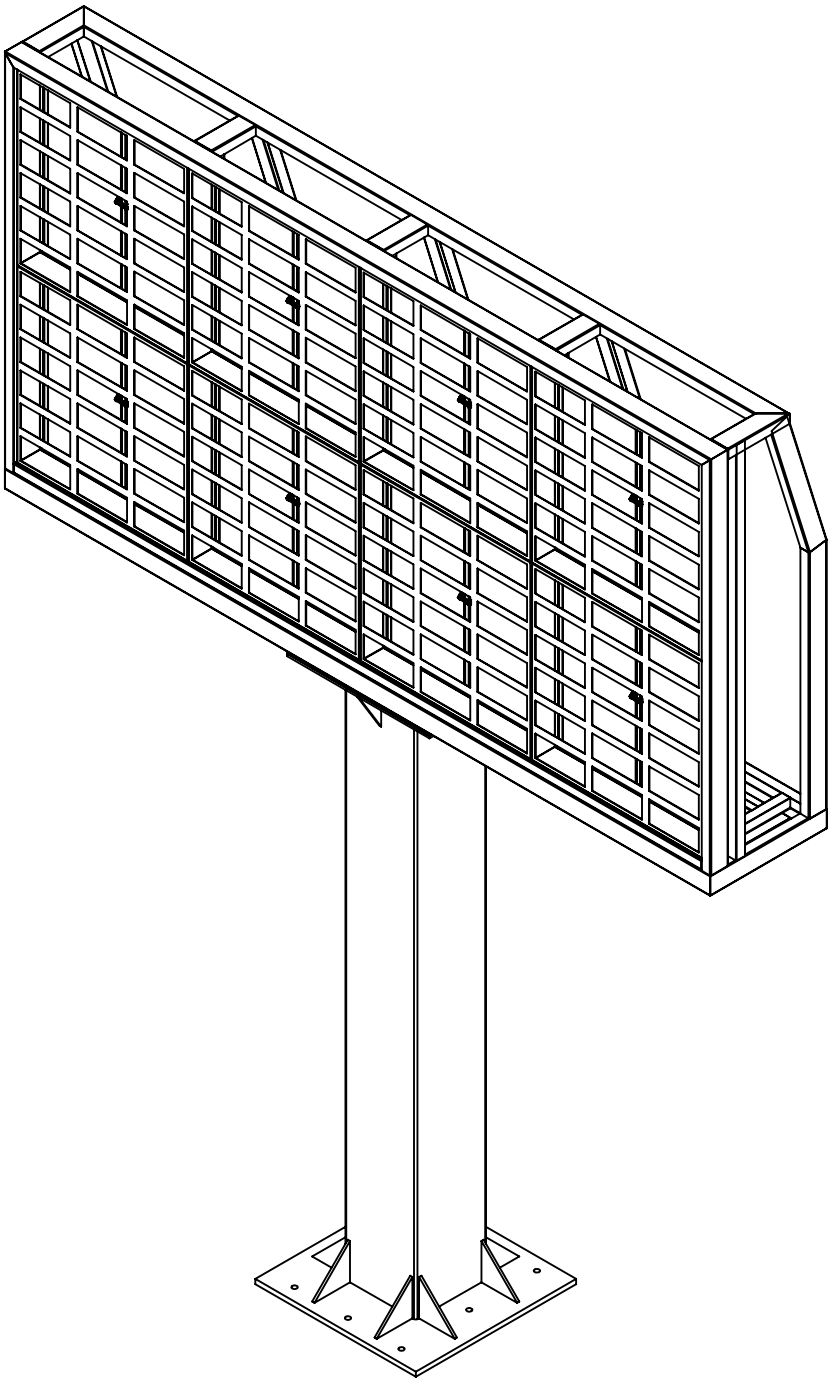
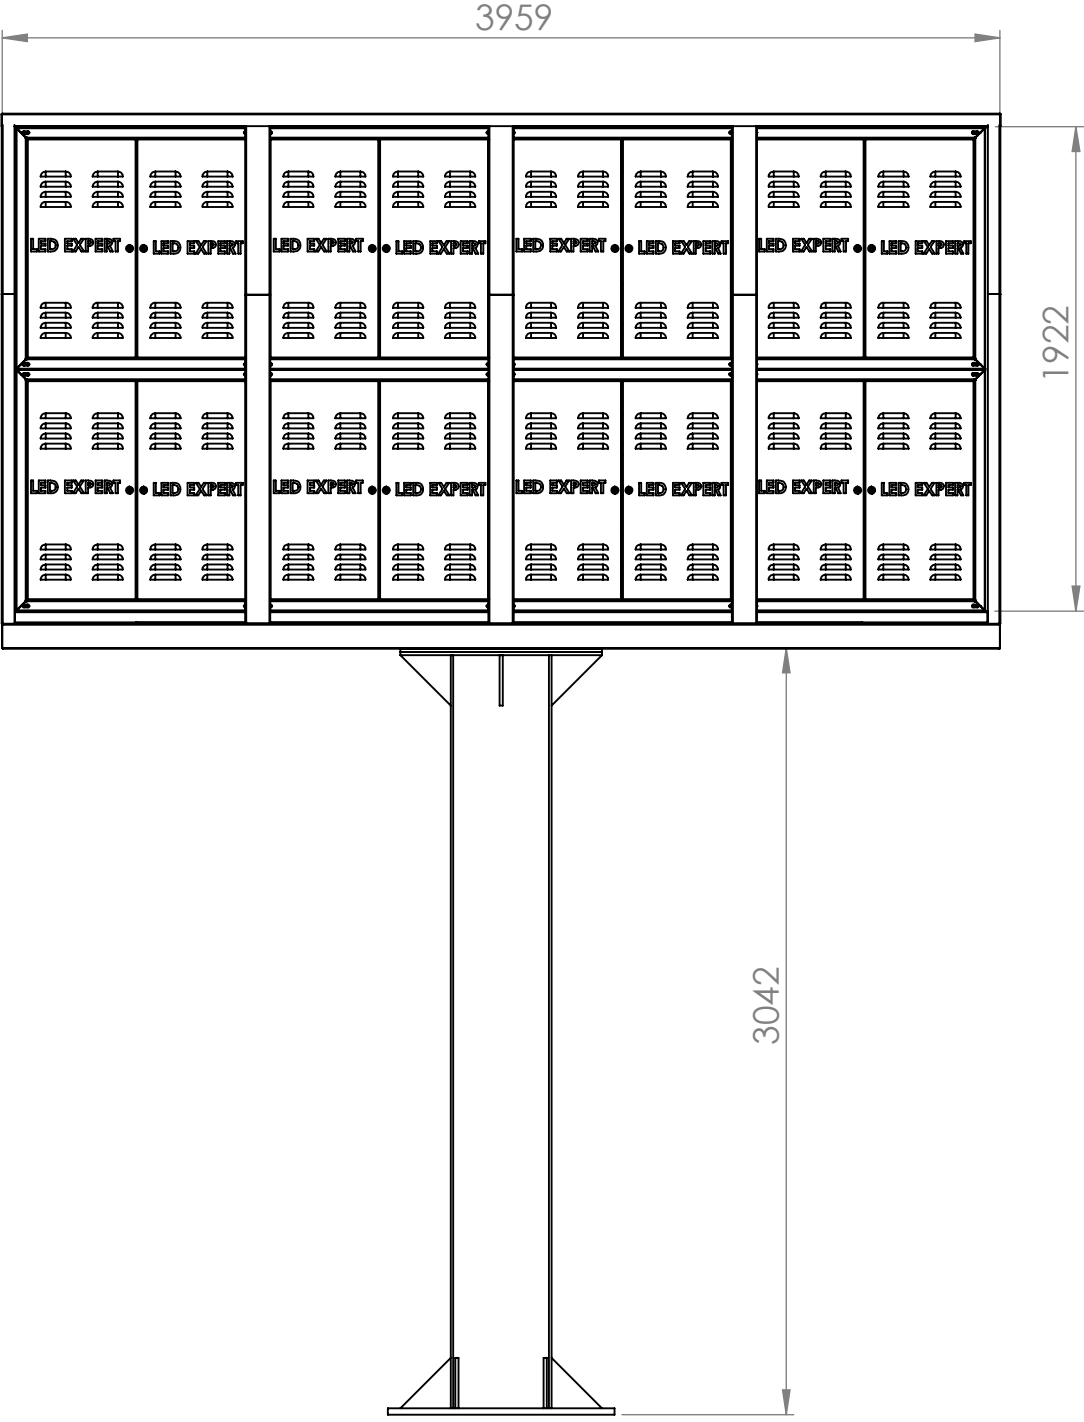


SE NÃO ESPECIFICADO: DIMENSÕES EM MILÍMETROS ACABAM. SUPERFÍCIE: TOLERÂNCIAS: LINEAR: ANGULAR:			ACABAMENTO: -			REBARBAR E QUEBRAR ARESTAS AGUDAS			NÃO MUDAR ESCALA DO DESENHO					
									Quant: 01					
	NOME	ASSINATURA	DATA				TÍTULO: estrutura outdoor							
DESEN.	WilliamM													
VERIF.														
APROV.														
MANUF.														
QUALID				MATERIAL: Aço carbono			DES. Nº			P0026-00			A3	
				PESO DO PAINEL: 304kg			ESCALA: 1:20			FOLHA 1 DE 1				