


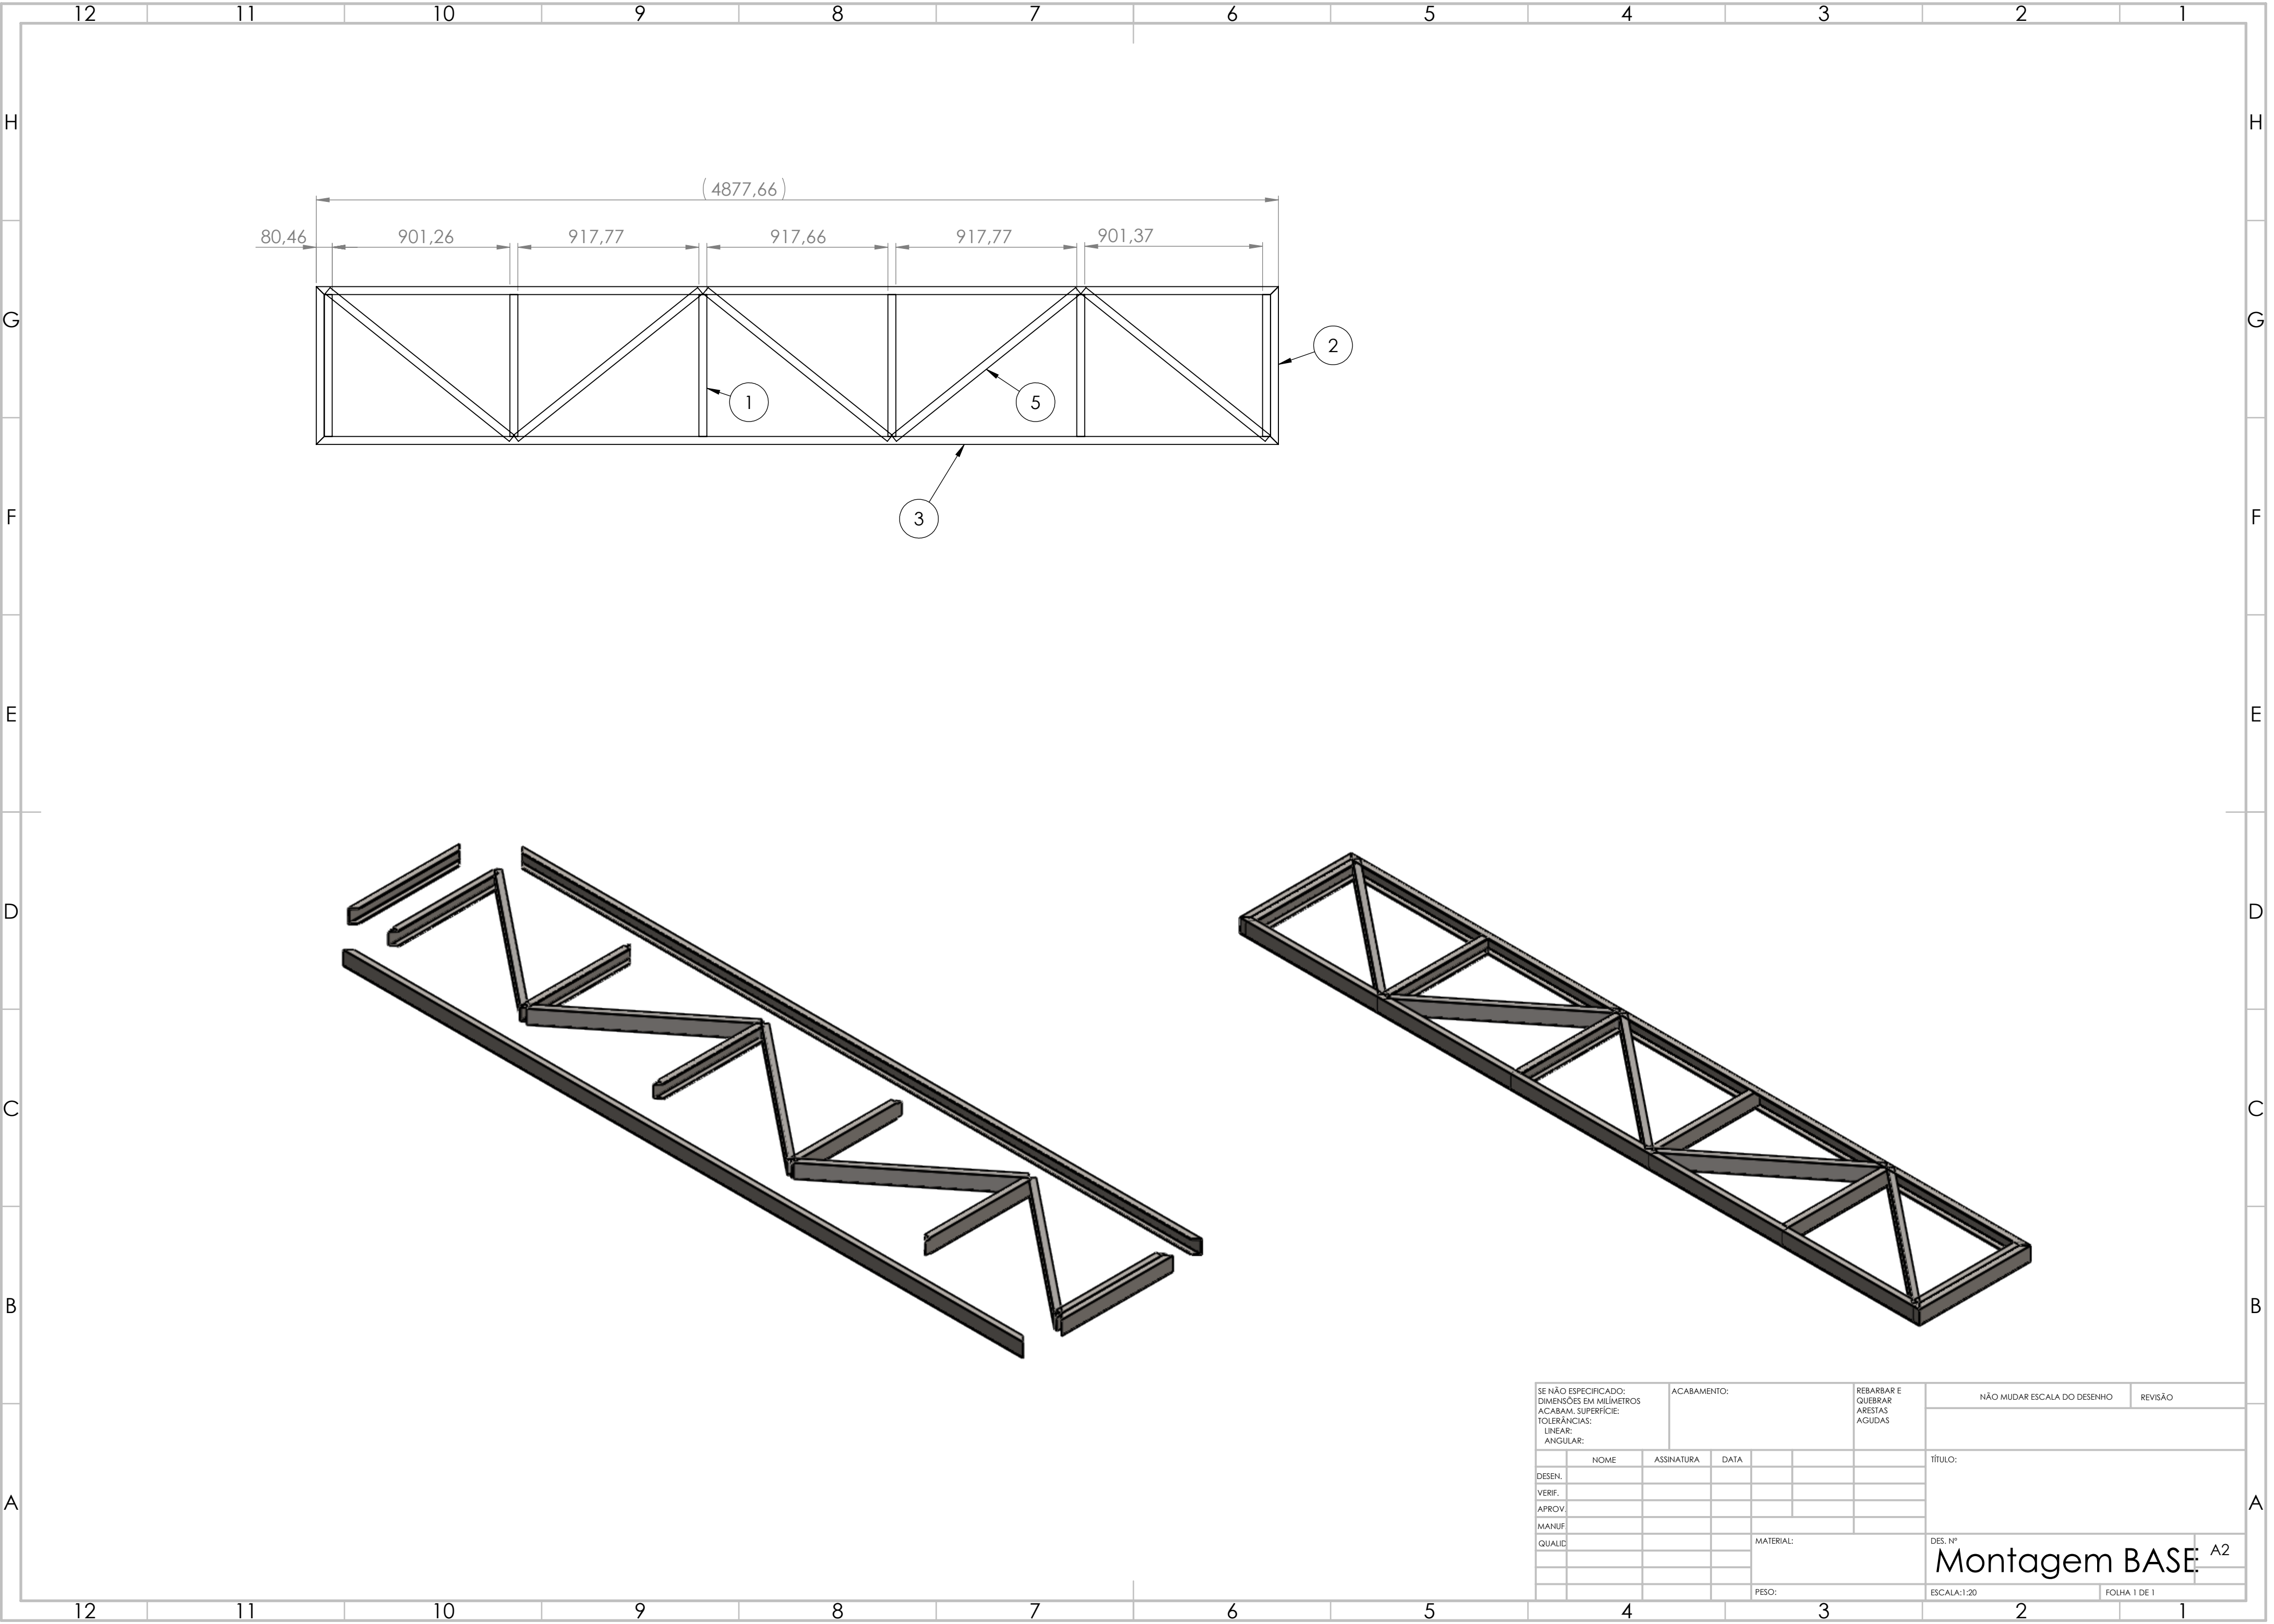

SE NÃO ESPECIFICADO: DIMENSÕES EM MILÍMETROS ACABAM. SUPERFÍCIE: TOLERÂNCIAS: LINEAR: ANGULAR:				ACABAMENTO:			REBARBAR E QUEBRAR ARESTAS AGUDAS	NÃO MUDAR ESCALA DO DESENHO		REVISÃO	
	NOME	ASSINATURA	DATA				TÍTULO:				
DESEN.							DES. Nº Montagem BASE A2				
VERIF.											
APROV.											
MANUF.											
QUALID											
						MATERIAL:					
						PESO:	ESCALA:1:20			FOLHA 1 DE 1	